
Ensuite 3D and Plan

J1122 - 235 Esplanade



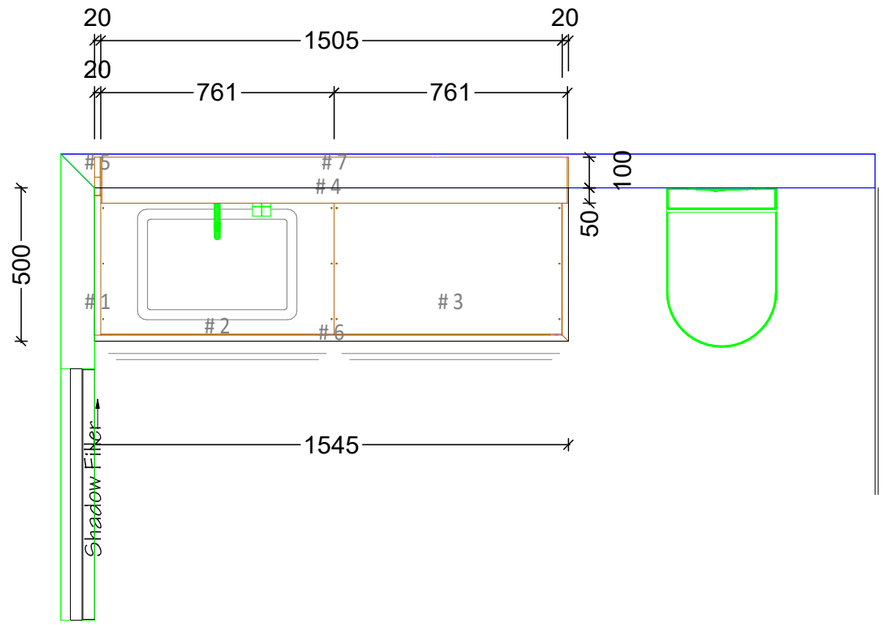

Approved CN Drawings Supersede All Other Drawings and Specs

CODE	DESCRIPTION
JO2	Doors and Panels - 18mm Chifley Profile 2Pac Flannel Flower 13/65 Bauwerk Zero Gloss
JPULL	Rebated For J-Pull Fingerpull Handle
HO2	Handle - Beslag Thread - Toniton Greige
LED	Rebated LED Profile - LED by others
ST1	20mm Stone by Others

Name: Grace Lewin

Address:
235 Esplanade East
Port Melbourne

Sheet # 1 of 6

Date: 11/11/26

Drawn By: AF

JOB STANDARD MATERIALS

UNLESS STATED OTHERWISE
INTERNAL CARCASSES TO BE:
* 16mm White - 1mm
ALL ADJ SHELF HOLES 5X 5MM HOLES 32MM SPACINGS
ALL DRAWERS TO BE *Blum Legrabox Drawer
ALL HINGES TO BE 110* BLUM SOFTCLOSE


CN FITOUTS PTY LTD
CUSTOM MADE JOINERY


P 03 9761 6994
E info@cnfitouts.com.au
www.cnfitouts.com.au

6 Stephenson rd.
Bayswater North 3153

Ensuite Elevation and section

J1122 - 235 Esplanade

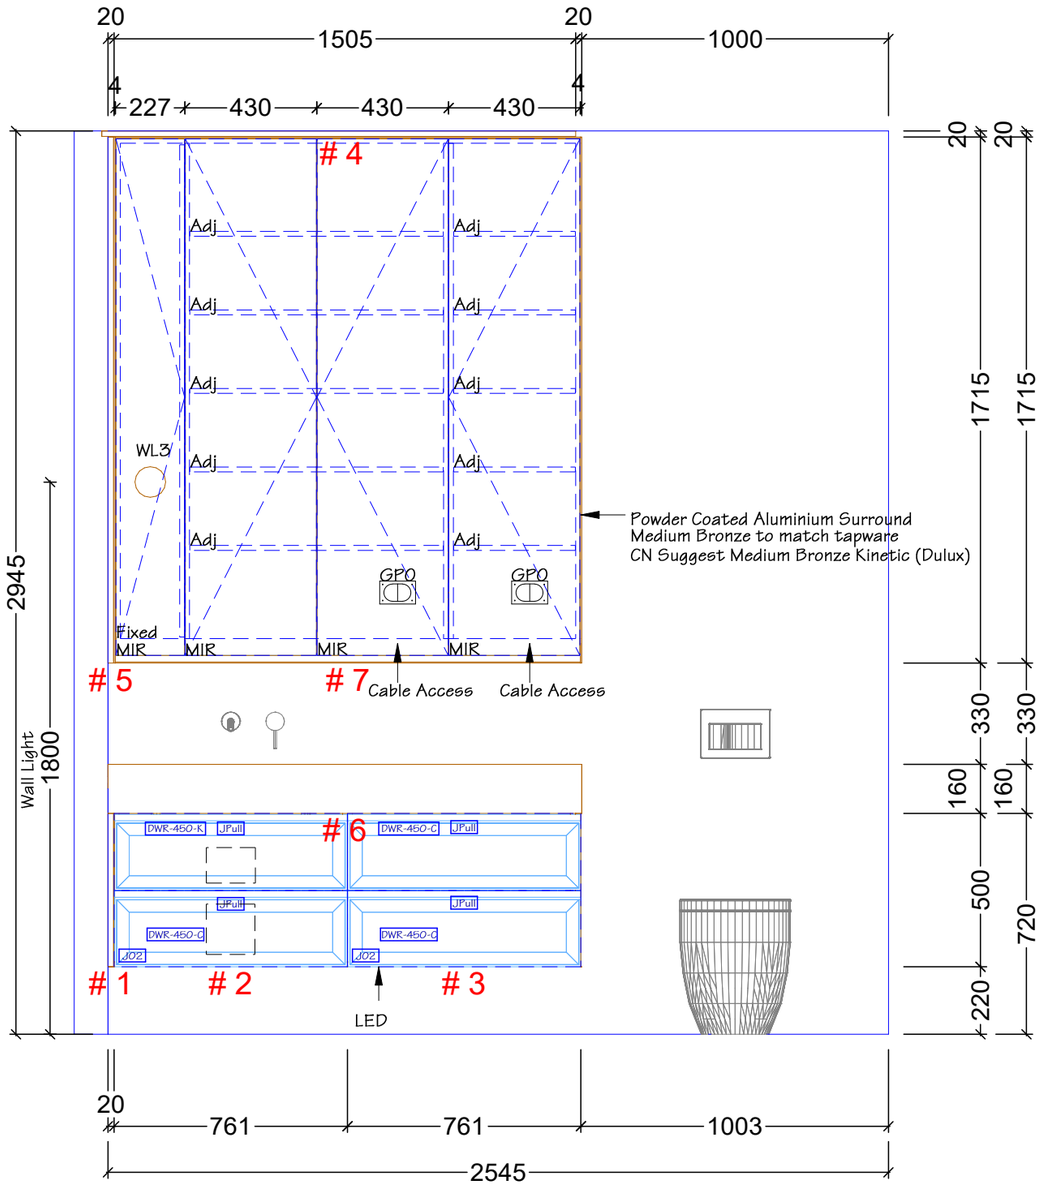

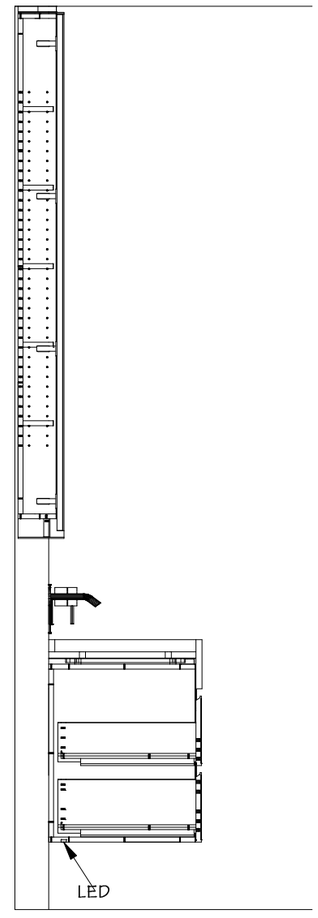

Approved CN Drawings Supersede All Other Drawings and Specs

CODE	DESCRIPTION
JO2	Doors and Panels - 18mm Chifley Profile 2Pac Flannel Flower 13/65 Bauwerk Zero Gloss
JPULL	Rebated For J-Pull Fingerpull Handle
HO2	Handle - Beslag Thread - Toniton Greige
LED	Rebated LED Profile - LED by others
ST1	20mm Stone by Others

Name: Grace Lewin

Address:
235 Esplanade East
Port Melbourne

Sheet # 2 of 6

Date: 11/11/26

Drawn By: AF

JOB STANDARD MATERIALS

UNLESS STATED OTHERWISE
INTERNAL CARCASSES TO BE:
* 16mm White - 1mm
ALL ADJ SHELF HOLES 5X 5MM HOLES 32MM SPACINGS
ALL DRAWERS TO BE *Blum Legrabox Drawer
ALL HINGES TO BE 110° BLUM SOFTCLOSE


CN FITOUTS PTY LTD
CUSTOM MADE JOINERY

P 03 9761 6994
E info@cnfitouts.com.au
www.cnfitouts.com.au

6 Stephenson rd.
Bayswater North 3153

Bathroom 3D and Plan



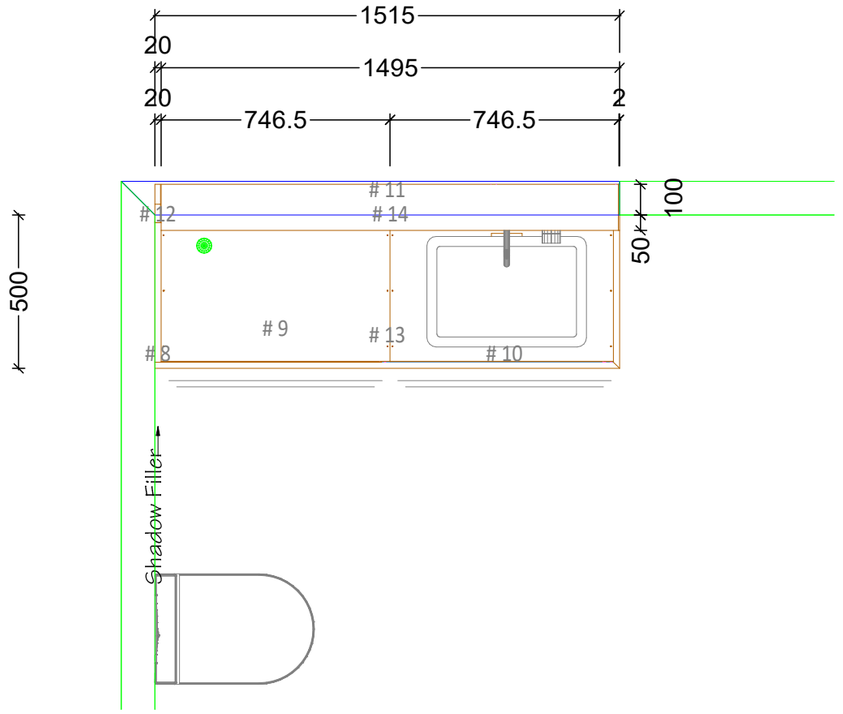

Approved CN Drawings Supersede All Other Drawings and Specs

CODE	DESCRIPTION
JO2	Doors and Panels - 18mm Chifley Profile 2Pac Flannel Flower 13/65 Bauwerk Zero Gloss
JPULL	Rebated For J-Pull Fingerpull Handle
HO2	Handle - Beslag Thread - Toniton Greige
LED	Rebated LED Profile - LED by others
ST1	20mm Stone by Others

Name: Grace Lewin

Address:

235 Esplanade East

Port Melbourne

Sheet # 3 of 6

Date: 11/11/26

Drawn By: AF

JOB STANDARD MATERIALS

UNLESS STATED OTHERWISE
INTERNAL CARCASSES TO BE:
* 16mm White - 1mm
ALL ADJ SHELF HOLES 5X 5MM HOLES 32MM SPACINGS
ALL DRAWERS TO BE *Blum Legrabox Drawer
ALL HINGES TO BE 110* BLUM SOFTCLOSE


CN FITOUTS PTY LTD
CUSTOM MADE JOINERY

P 03 9761 6994
E info@cnfitouts.com.au
www.cnfitouts.com.au


6 Stephenson rd.
Bayswater North 3153

Bathroom Elevation and Section


J1122 - 235 Esplanade

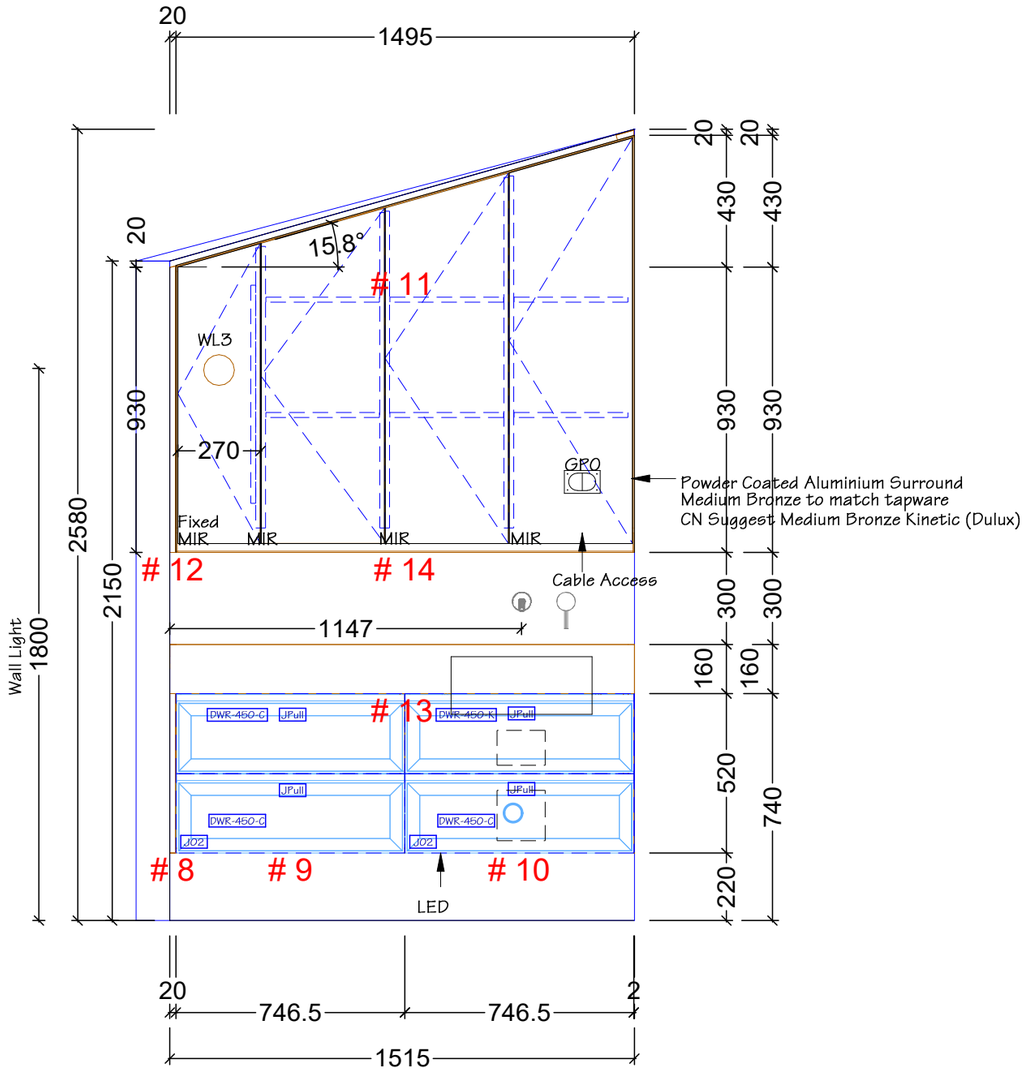

S1 2 Section - Bathroom
Scale: 1:20

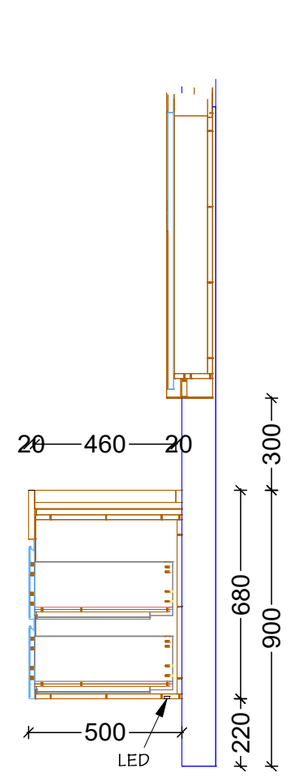

S2 2 Section - Bathroom
Scale: 1:20

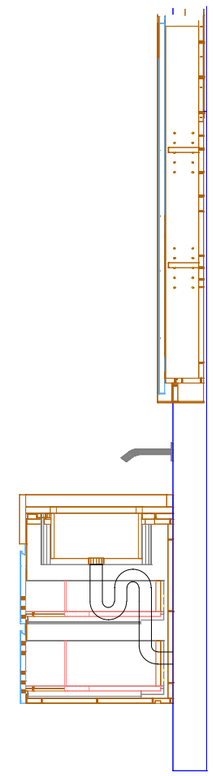

Approved CN Drawings Supersede All Other Drawings and Specs

CODE	DESCRIPTION
JO2	Doors and Panels - 18mm Chifley Profile 2Pac Flannel Flower 13/65 Bauwerk Zero Gloss
JPULL	Rebated For J-Pull Fingerpull Handle
HO2	Handle - Beslag Thread - Toniton Greige
LED	Rebated LED Profile - LED by others
ST1	20mm Stone by Others

Name: Grace Lewin

Address:
235 Esplanade East
Port Melbourne

Sheet # 4 of 6

Date: 11/11/26

Drawn By: AF

JOB STANDARD MATERIALS

UNLESS STATED OTHERWISE
INTERNAL CARCASSES TO BE:
* 16mm White - 1mm
ALL ADJ SHELF HOLES 5X 5MM HOLES 32MM SPACINGS
ALL DRAWERS TO BE *Blum Legrabox Drawer
ALL HINGES TO BE 110* BLUM SOFTCLOSE


CN FITOUTS PTY LTD
CUSTOM MADE JOINERY


P 03 9761 6994
E info@cnfitouts.com.au
www.cnfitouts.com.au

6 Stephenson rd.
Bayswater North 3153

60 x 3mm Powdercoated Frames

J1122 - 235 Esplanade

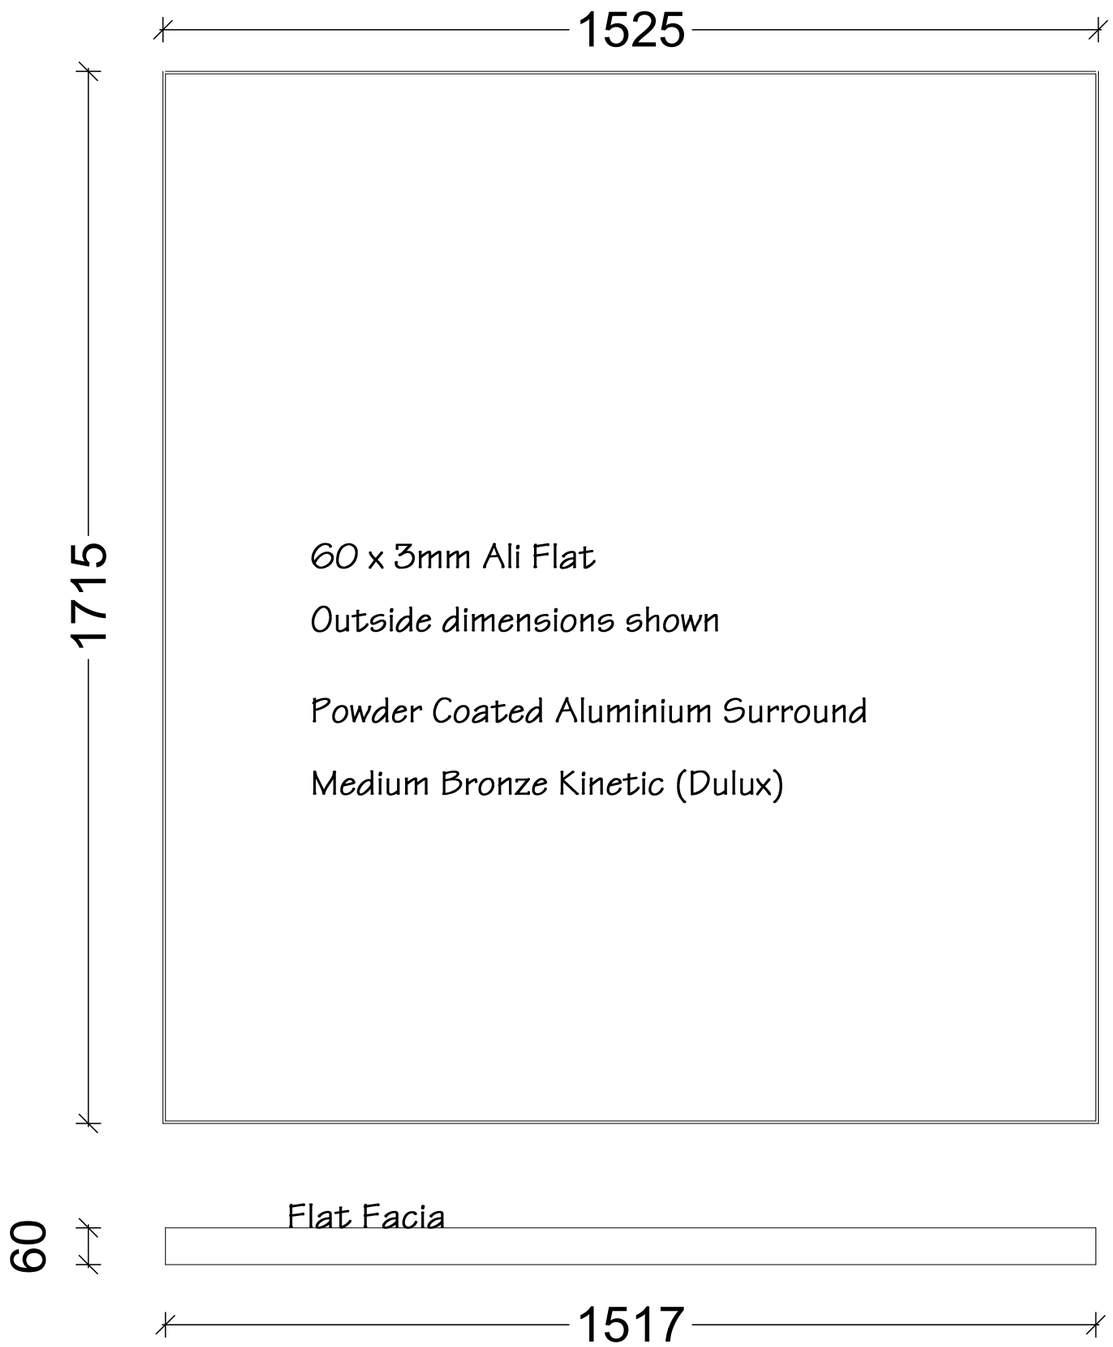

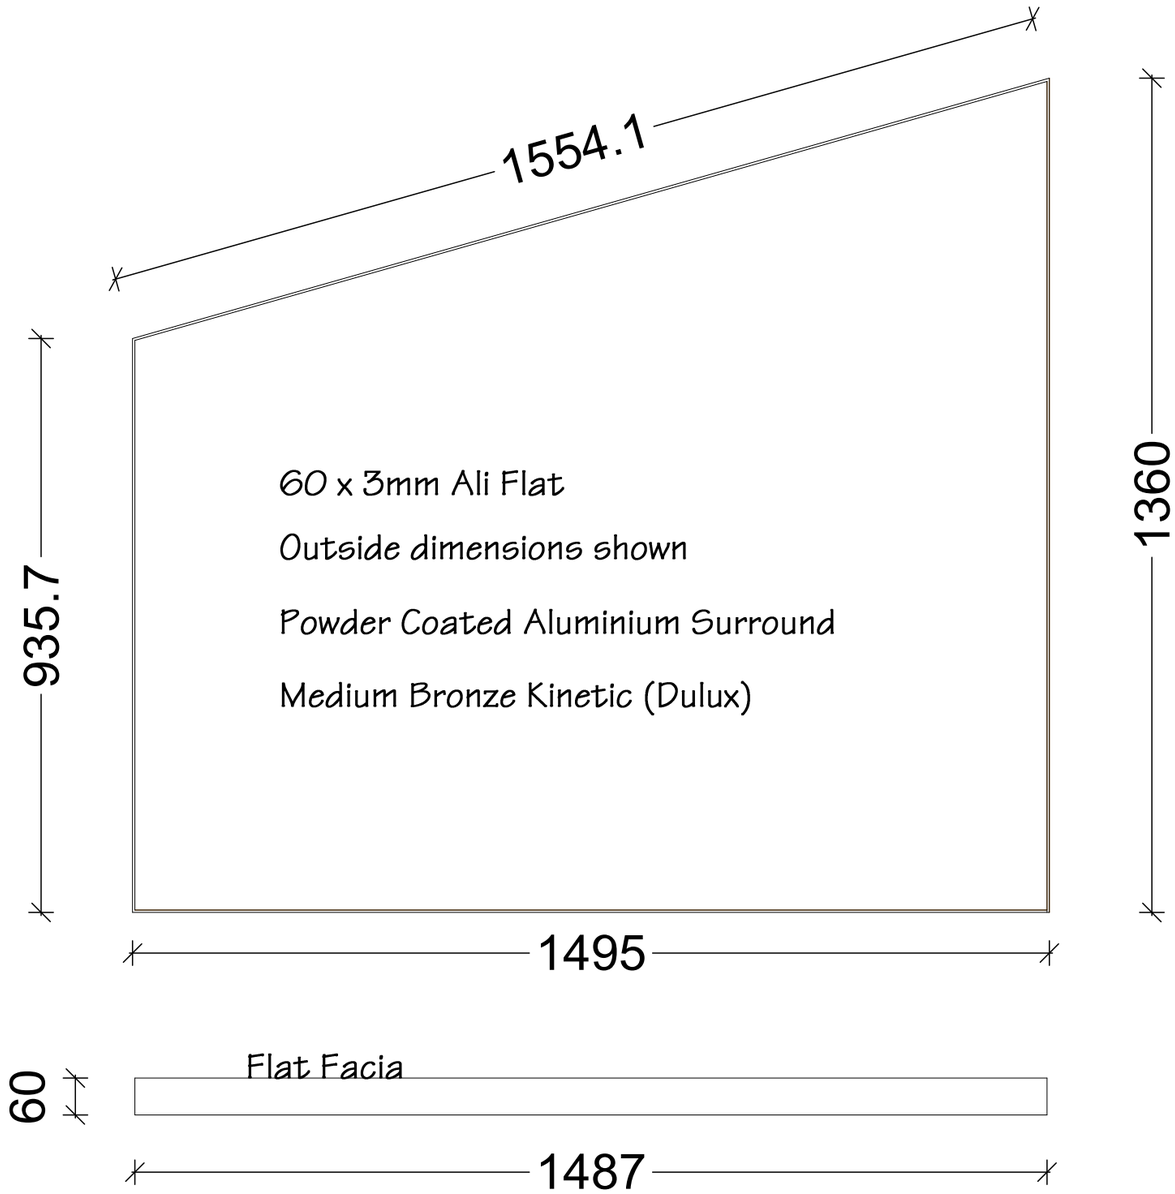

Approved CN Drawings Supersede All Other Drawings and Specs

CODE	DESCRIPTION
JO2	Doors and Panels - 18mm Chifley Profile 2Pac Flannel Flower 13/65 Bauwerk Zero Gloss
JPULL	Rebated For J-Pull Fingerpull Handle
HO2	Handle - Beslag Thread - Toniton Greige
LED	Rebated LED Profile - LED by others
ST1	20mm Stone by Others

Name: Grace Lewin

Address:
235 Esplanade East
Port Melbourne

Sheet # 5 of 6

Date: 11/11/26

Drawn By: AF


JOB STANDARD MATERIALS

UNLESS STATED OTHERWISE
INTERNAL CARCASSES TO BE:
* 16mm White - 1mm
ALL ADJ SHELF HOLES 5X 5MM HOLES 32MM SPACINGS
ALL DRAWERS TO BE *Blum Legrabox Drawer
ALL HINGES TO BE 110* BLUM SOFTCLOSE

CN FITOUTS PTY LTD
CUSTOM MADE JOINERY

P 03 9761 6994
E info@cnfitouts.com.au
www.cnfitouts.com.au

6 Stephenson rd.
Bayswater North 3153

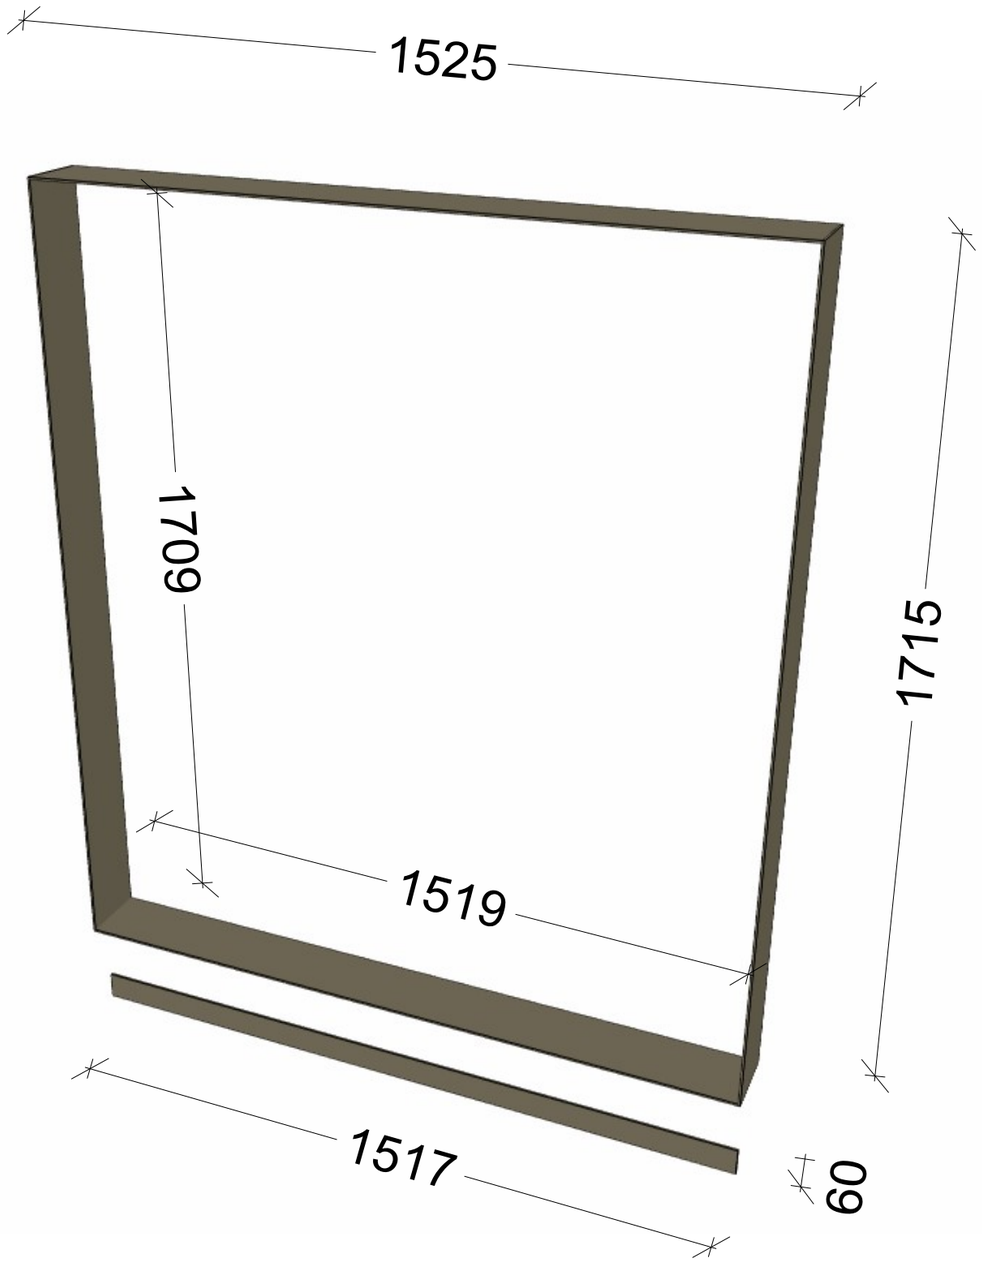

Approved CN Drawings Supersede All Other Drawings and Specs

CODE	DESCRIPTION
JO2	Doors and Panels - 18mm Chifley Profile 2Pac Flannel Flower 13/65 Bauwerk Zero Gloss
JPULL	Rebated For J-Pull Fingerpull Handle
HO2	Handle - Beslag Thread - Toniton Greige
LED	Rebated LED Profile - LED by others
ST1	20mm Stone by Others

Name: Grace Lewin

Address:
235 Esplanade East
Port Melbourne

Sheet # 6 of 6

Date: 11/11/26

Drawn By: AF

JOB STANDARD MATERIALS

UNLESS STATED OTHERWISE
INTERNAL CARCASSES TO BE:
* 16mm White - 1mm
ALL ADJ SHELF HOLES 5X 5MM HOLES 32MM SPACINGS
ALL DRAWERS TO BE *Blum Legrabox Drawer
ALL HINGES TO BE 110* BLUM SOFTCLOSE

CN FITOUTS PTY LTD
CUSTOM MADE JOINERY

P 03 9761 6994
E info@cnfitouts.com.au
www.cnfitouts.com.au

6 Stephenson rd.
Bayswater North 3153