
Master WIR 3Ds

J1122 - 235 Esplanade

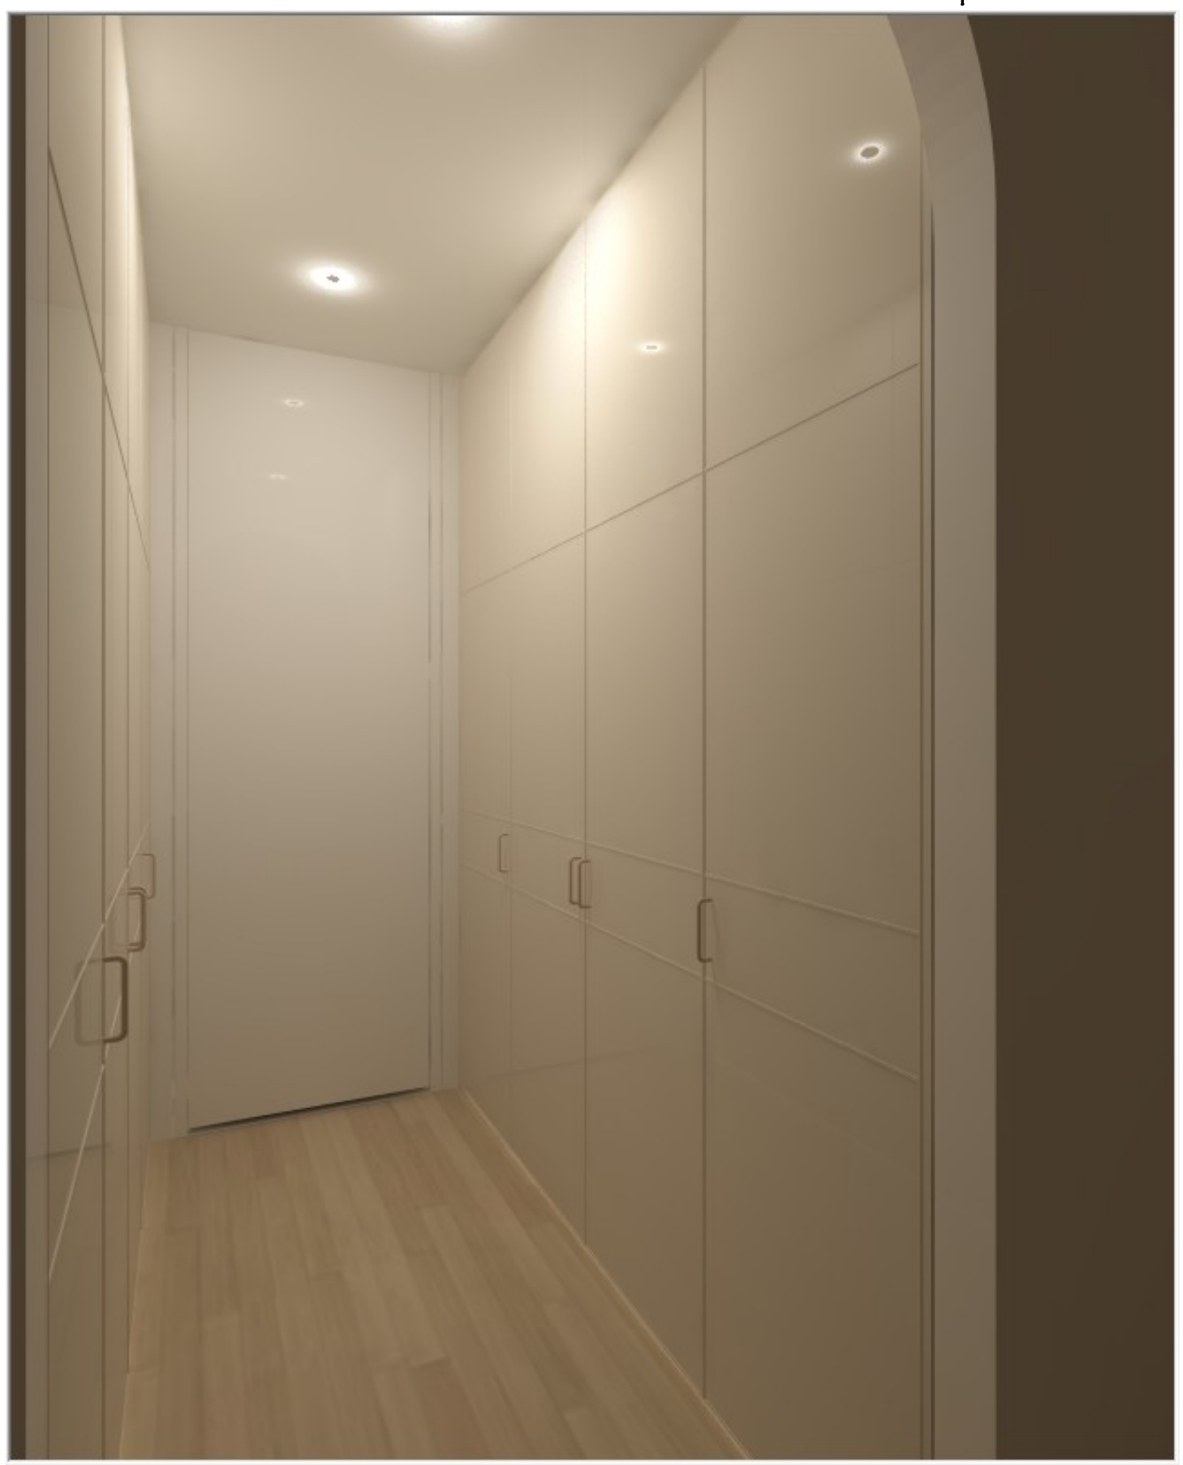



Approved CN Drawings Supersede All Other Drawings and Specs

CODE	DESCRIPTION
JO2	18mm Chifley Profile 2Pac Flannel Flower 13/65 Bauwerk Zero Gloss
HO2	Handle - Beslag Thread - Toniton Greige
HR1	Hanging Rail - White Oval
LED2	Surface Mounted LED and Profile by Others

Name: Grace Lewin

Address:

235 Esplanade East

Port Melbourne

Sheet # 1 of 13

Date: 26/10/26

Drawn By: AF

JOB STANDARD MATERIALS

UNLESS STATED OTHERWISE
INTERNAL CARCASSES TO BE:
* 16mm White - 1mm
ALL ADJ SHELF HOLES 5X 5MM HOLES 32MM SPACINGS
ALL DRAWERS TO BE *Blum Legrabox Drawer
ALL HINGES TO BE 110* BLUM SOFTCLOSE


CN FITOUTS PTY LTD
CUSTOM MADE JOINERY


P 03 9761 6994
E info@cnfitouts.com.au
www.cnfitouts.com.au

6 Stephenson rd.
Bayswater North 3153

Master WIR Plan and Kicks

J1122 - 235 Esplanade

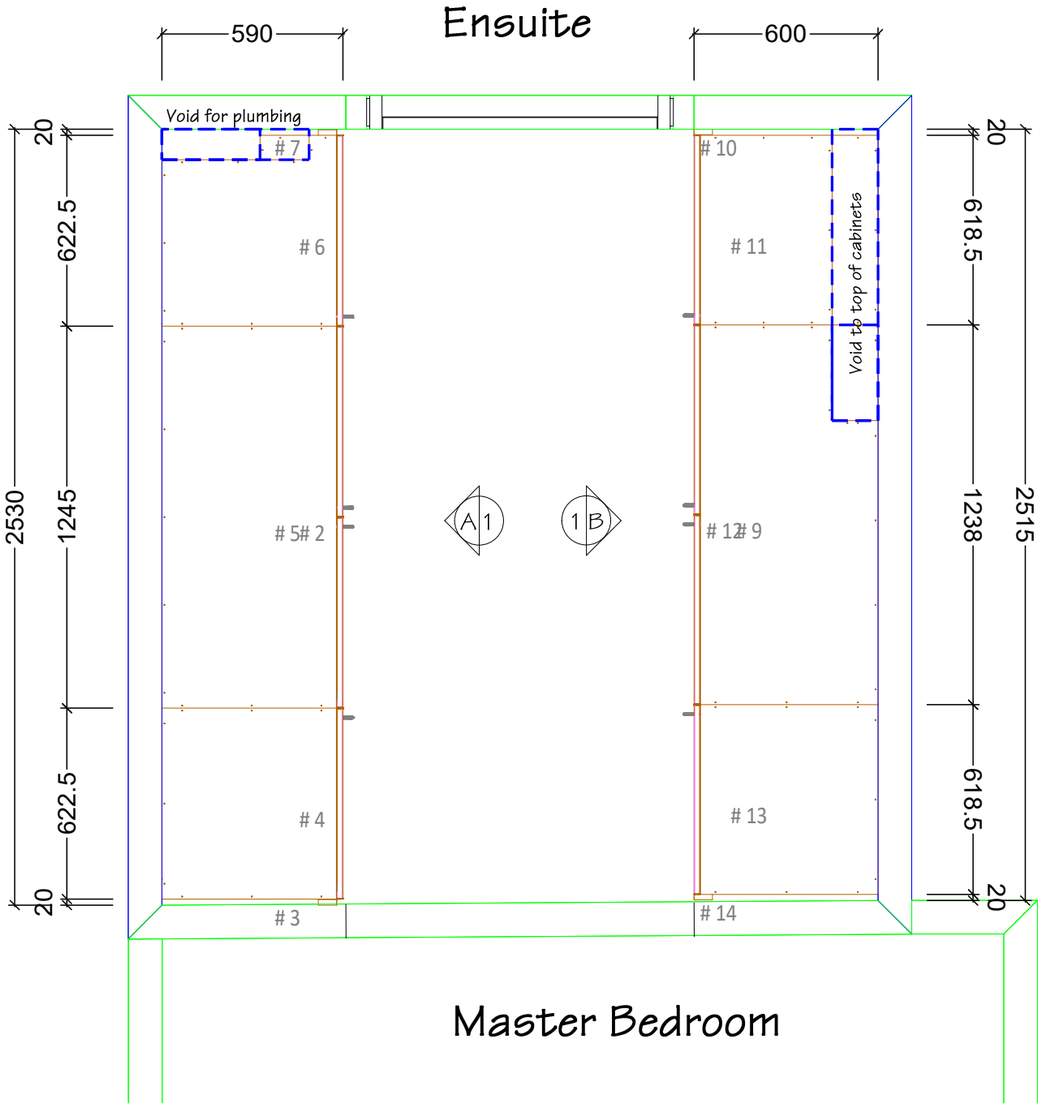

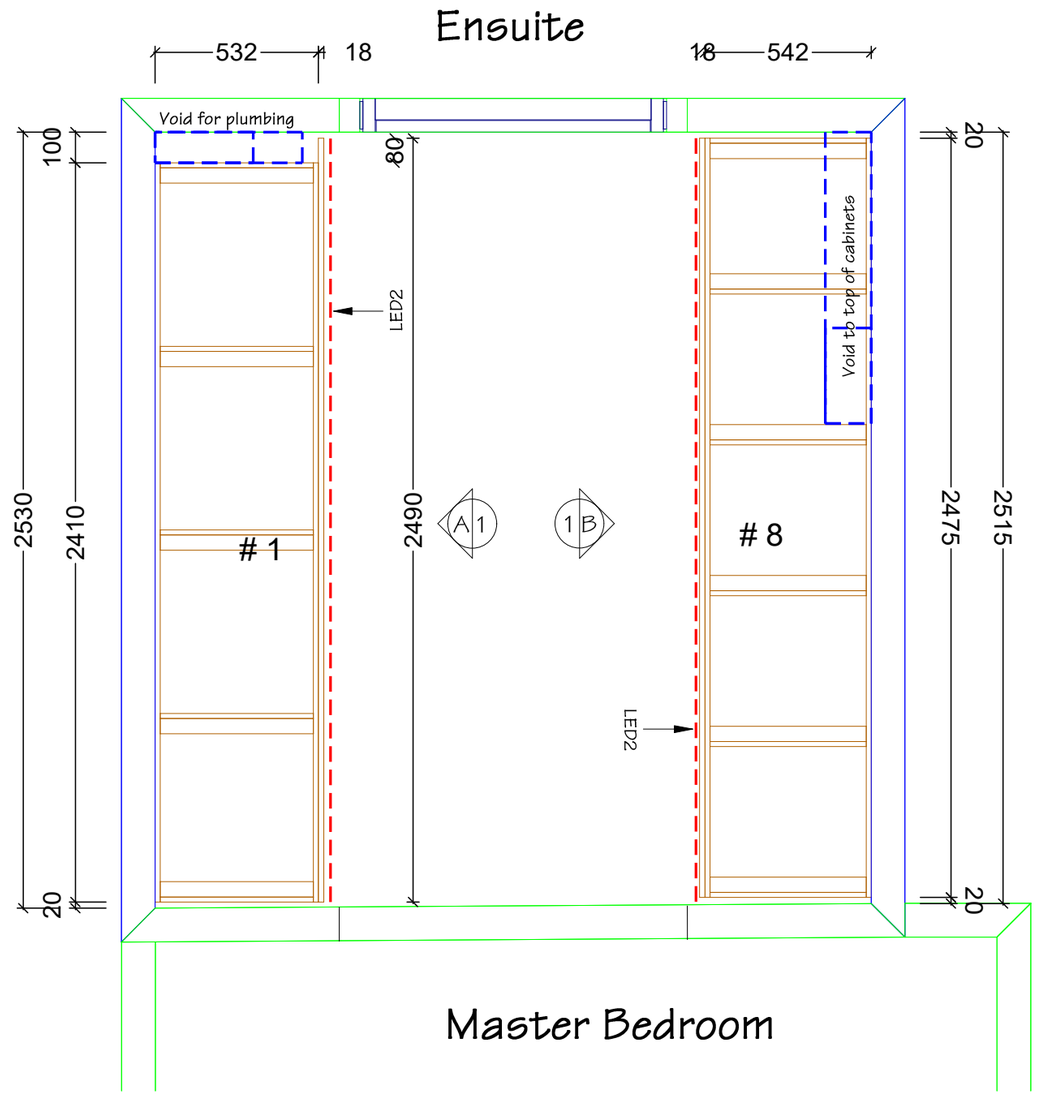

Approved CN Drawings Supersede All Other Drawings and Specs

CODE	DESCRIPTION
JO2	18mm Chifley Profile 2Pac Flannel Flower 13/65 Bauwerk Zero Gloss
HO2	Handle - Beslag Thread - Toniton Greige
HR1	Hanging Rail - White Oval
LED2	Surface Mounted LED and Profile by Others

Name: Grace Lewin

Address:

235 Esplanade East

Port Melbourne

Sheet # 2 of 13

Date: 26/10/26

Drawn By: AF

JOB STANDARD MATERIALS

UNLESS STATED OTHERWISE
INTERNAL CARCASSES TO BE:
* 16mm White - 1mm
ALL ADJ SHELF HOLES 5X 5MM HOLES 32MM SPACINGS
ALL DRAWERS TO BE *Blum Legrabox Drawer
ALL HINGES TO BE 110* BLUM SOFTCLOSE

CN FITOUTS PTY LTD
CUSTOM MADE JOINERY


P 03 9761 6994
E info@cnfitouts.com.au
www.cnfitouts.com.au

6 Stephenson rd.
Bayswater North 3153


Master WIR Elevations

J1122 - 235 Esplanade

Shadow Fillers to this room Only

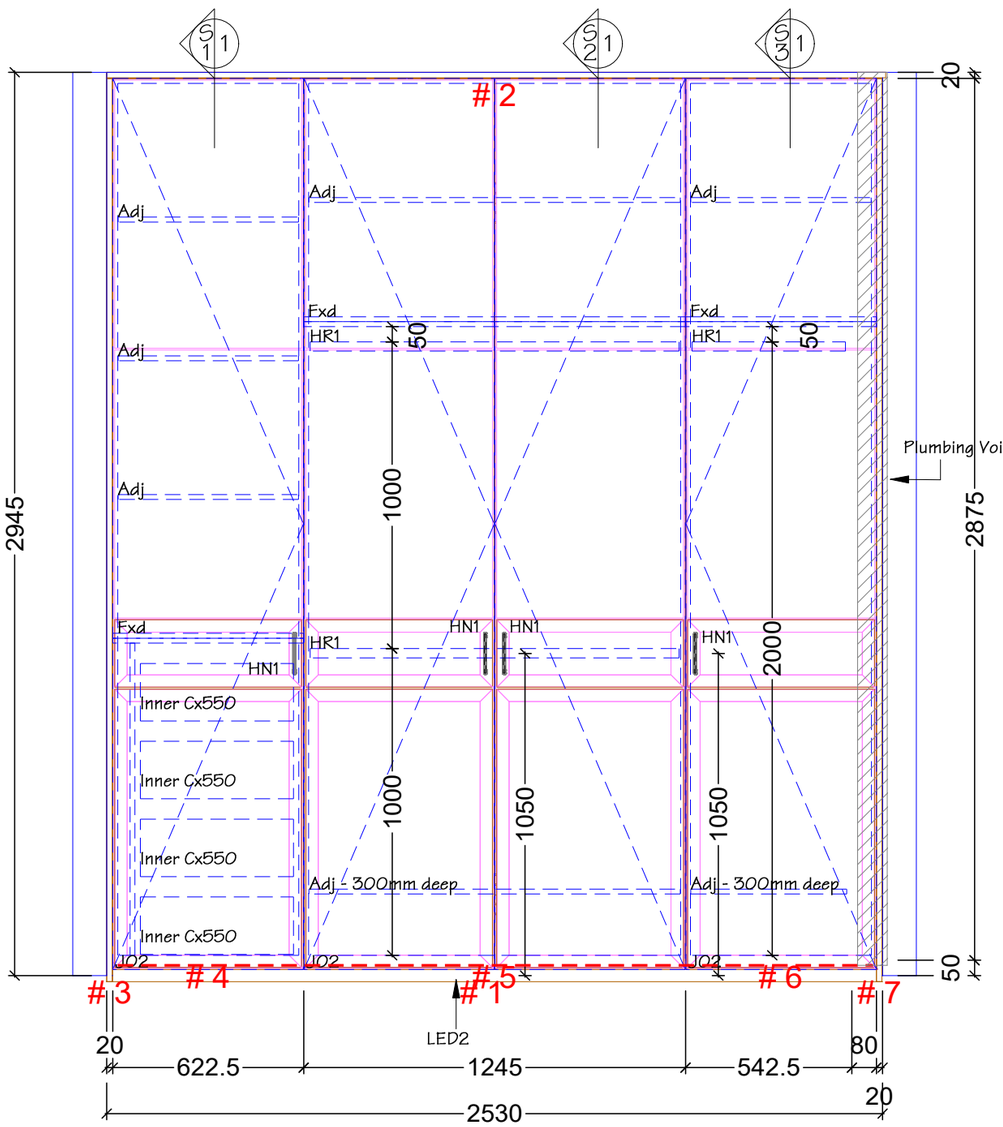

A 1 Elevation - Master WIR
Scale: 1:20

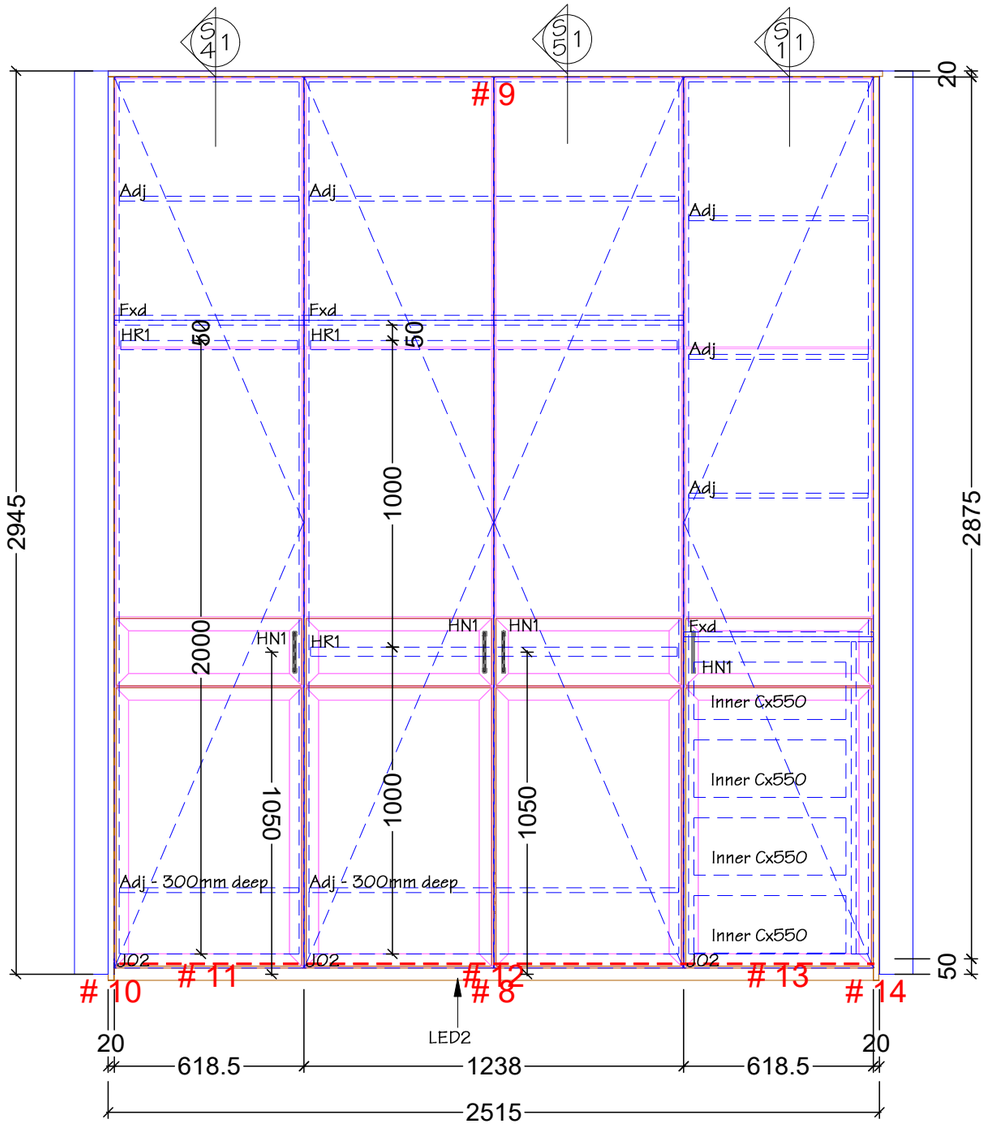

B 1 Elevation - Master WIR
Scale: 1:20

Approved CN Drawings Supersede All Other Drawings and Specs

CODE	DESCRIPTION
JO2	18mm Chifley Profile 2Pac Flannel Flower 13/65 Bauwerk Zero Gloss
HO2	Handle - Beslag Thread - Toniton Greige
HR1	Hanging Rail - White Oval
LED2	Surface Mounted LED and Profile by Others

Name: Grace Lewin

Address:
235 Esplanade East
Port Melbourne

Sheet # 3 of 13

Date: 26/10/26

Drawn By: AF

JOB STANDARD MATERIALS

UNLESS STATED OTHERWISE
INTERNAL CARCASSES TO BE:
* 16mm White - 1mm
ALL ADJ SHELF HOLES 5X 5MM HOLES 32MM SPACINGS
ALL DRAWERS TO BE *Blum Legrabox Drawer
ALL HINGES TO BE 110* BLUM SOFTCLOSE


CN FITOUTS PTY LTD
CUSTOM MADE JOINERY

P 03 9761 6994
E info@cnfitouts.com.au
www.cnfitouts.com.au


6 Stephenson rd.
Bayswater North 3153

Master WIR Sections


J1122 - 235 Esplanade

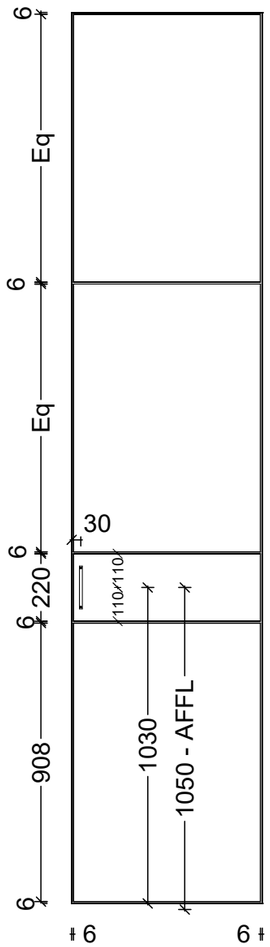


Door Typical Layout
Scale: 1:20

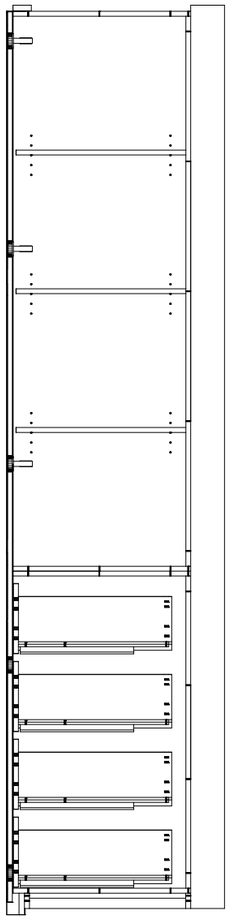


S1 Section - Master WIR
Scale: 1:20

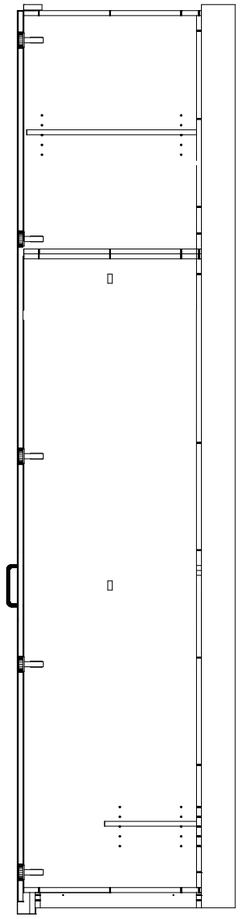


S2 Section - Master WIR
Scale: 1:20

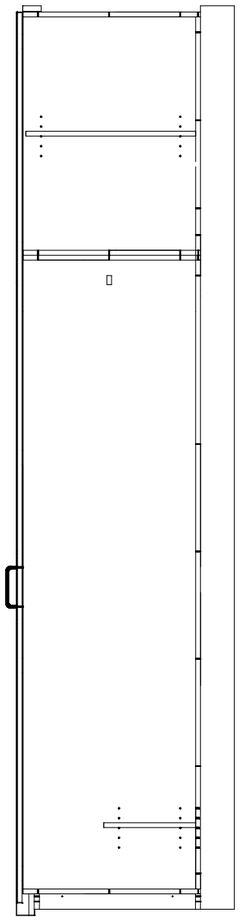

S3 Section - Master WIR
Scale: 1:20

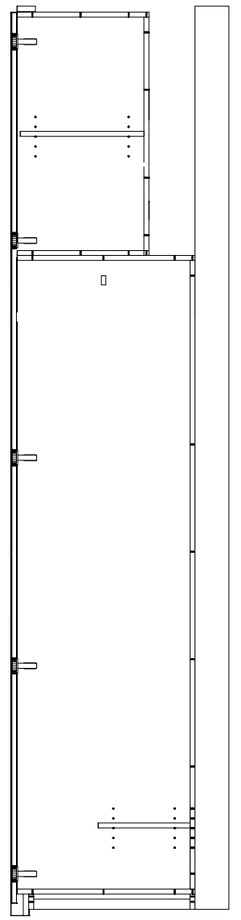

S4 Section - Master WIR
Scale: 1:20

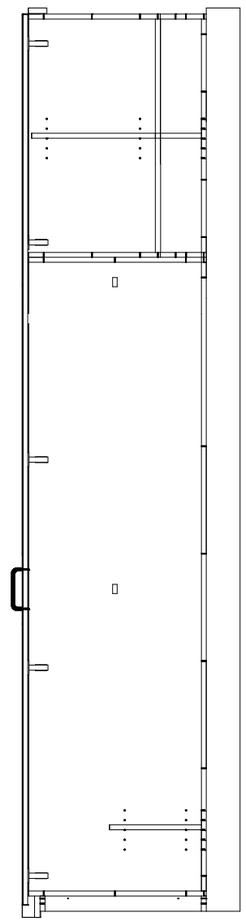

S5 Section - Master WIR
Scale: 1:20

Approved CN Drawings Supersede All Other Drawings and Specs

CODE	DESCRIPTION
JO2	18mm Chifley Profile 2Pac Flannel Flower 13/65 Bauwerk Zero Gloss
HO2	Handle - Beslag Thread - Toniton Greige
HR1	Hanging Rail - White Oval
LED2	Surface Mounted LED and Profile by Others

Name: Grace Lewin
Address:
235 Esplanade East
Port Melbourne
Sheet # 4 of 13
Date: 26/10/26
Drawn By: AF

JOB STANDARD MATERIALS
UNLESS STATED OTHERWISE
INTERNAL CARCASSES TO BE:
* 16mm White - 1mm
ALL ADJ SHELF HOLES 5X 5MM HOLES 32MM SPACINGS
ALL DRAWERS TO BE *Blum Legrabox Drawer
ALL HINGES TO BE 110* BLUM SOFTCLOSE

CN FITOUTS PTY LTD
CUSTOM MADE JOINERY
P 03 9761 6994
E info@cnfitouts.com.au
www.cnfitouts.com.au
6 Stephenson rd.
Bayswater North 3153

Bed 2 3D

J1122 - 235 Esplanade



Approved CN Drawings Supersede All Other Drawings and Specs

CODE	DESCRIPTION
JO2	18mm Chifley Profile 2Pac Flannel Flower 13/65 Bauwerk Zero Gloss
HO2	Handle - Beslag Thread - Toniton Greige
HR1	Hanging Rail - White Oval
LED2	Surface Mounted LED and Profile by Others

Name: Grace Lewin

Address:
235 Esplanade East
Port Melbourne

Sheet # 5 of 13

Date: 26/10/26

Drawn By: AF

JOB STANDARD MATERIALS

UNLESS STATED OTHERWISE
INTERNAL CARCASSES TO BE:
* 16mm White - 1mm
ALL ADJ SHELF HOLES 5X 5MM HOLES 32MM SPACINGS
ALL DRAWERS TO BE *Blum Legrabox Drawer
ALL HINGES TO BE 110* BLUM SOFTCLOSE


CN FITOUTS PTY LTD
CUSTOM MADE JOINERY


P 03 9761 6994
E info@cnfitouts.com.au
www.cnfitouts.com.au


6 Stephenson rd.
Bayswater North 3153

Bed 2 Plan and Elevations

J1122 - 235 Esplanade

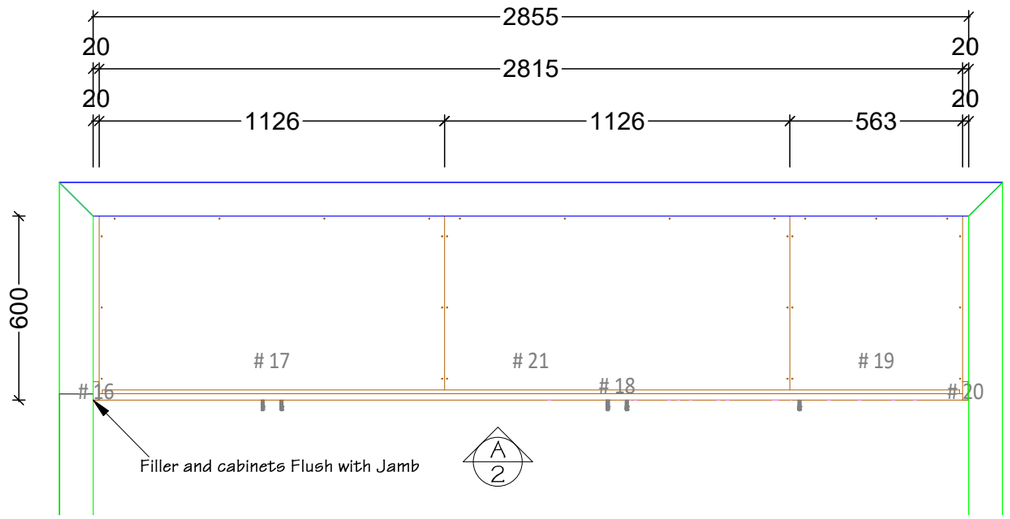

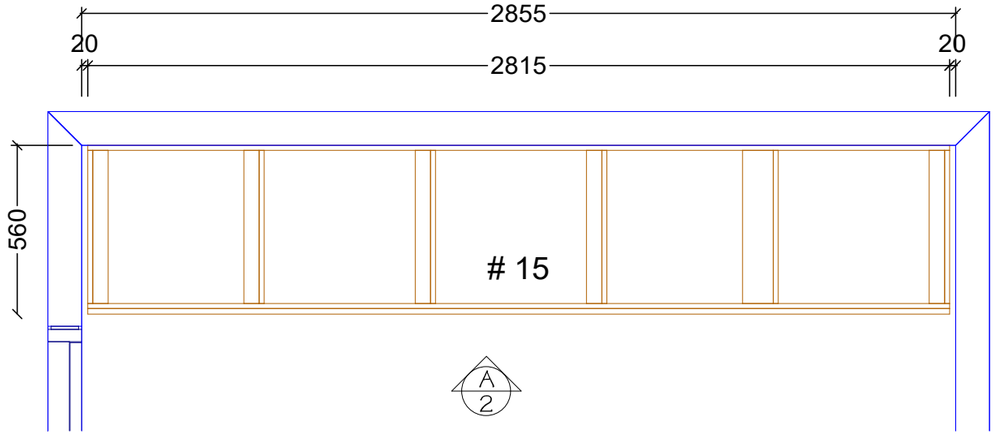

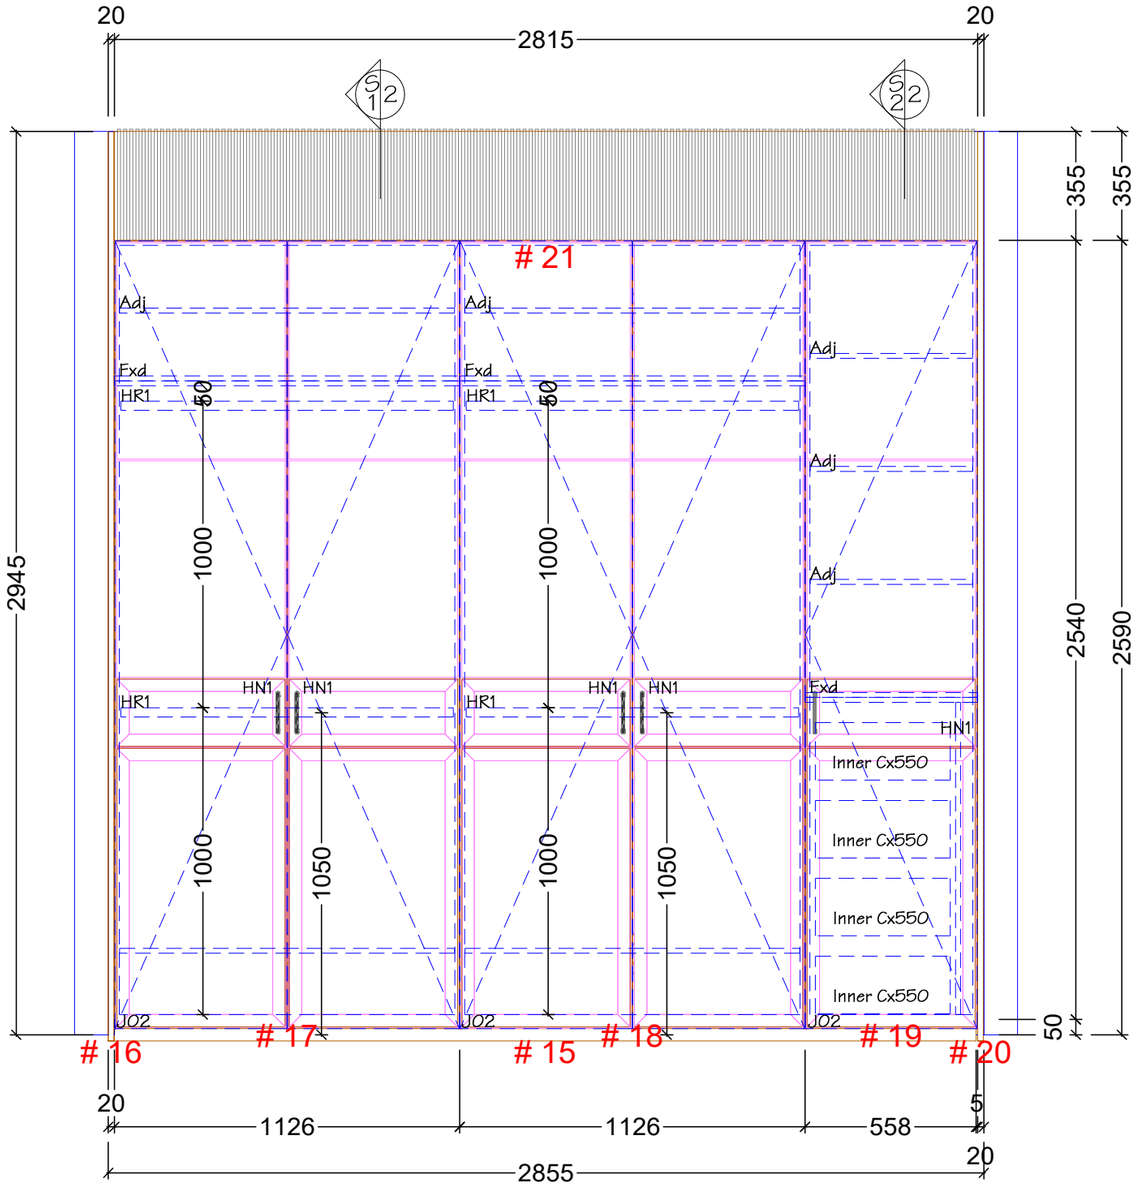

A
2 Elevation - Bed 2 Robe
Scale: 1:20

Approved CN Drawings Supersede All Other Drawings and Specs

CODE	DESCRIPTION
JO2	18mm Chifley Profile 2Pac Flannel Flower 13/65 Bauwerk Zero Gloss
HO2	Handle - Beslag Thread - Toniton Greige
HR1	Hanging Rail - White Oval
LED2	Surface Mounted LED and Profile by Others

Name: Grace Lewin

Address:

235 Esplanade East

Port Melbourne

Sheet # 6 of 13

Date: 26/10/26

Drawn By: AF

JOB STANDARD MATERIALS

UNLESS STATED OTHERWISE
INTERNAL CARCASSES TO BE:
* 16mm White - 1mm
ALL ADJ SHELF HOLES 5X 5MM HOLES 32MM SPACINGS
ALL DRAWERS TO BE *Blum Legrabox Drawer
ALL HINGES TO BE 110* BLUM SOFTCLOSE


CN FITOUTS PTY LTD
CUSTOM MADE JOINERY

P 03 9761 6994
E info@cnfitouts.com.au
www.cnfitouts.com.au


6 Stephenson rd.
Bayswater North 3153

Bed 2 Sections


J1122 - 235 Esplanade

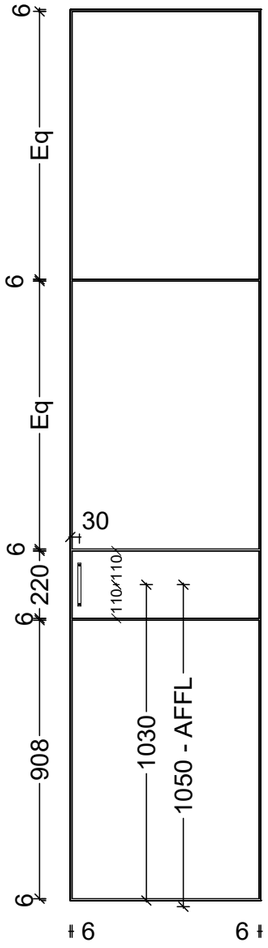

Door Typical Layout
Scale: 1:20

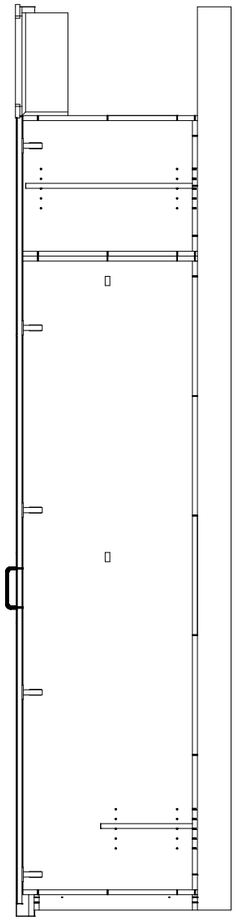

S1/2 Section - Bed 2 Robe
Scale: 1:20

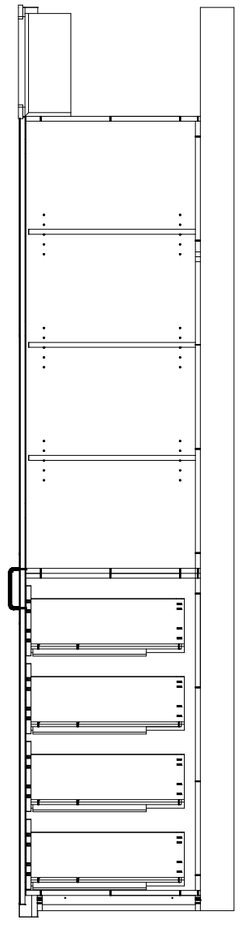

S2/2 Section - Bed 2 Robe
Scale: 1:20

Approved CN Drawings Supersede All Other Drawings and Specs

CODE	DESCRIPTION
JO2	18mm Chifley Profile 2Pac Flannel Flower 13/65 Bauwerk Zero Gloss
HO2	Handle - Beslag Thread - Toniton Greige
HR1	Hanging Rail - White Oval
LED2	Surface Mounted LED and Profile by Others

Name: Grace Lewin

Address:
235 Esplanade East
Port Melbourne

Sheet # 7 of 13

Date: 26/10/26

Drawn By: AF

JOB STANDARD MATERIALS

UNLESS STATED OTHERWISE
INTERNAL CARCASSES TO BE:
* 16mm White - 1mm
ALL ADJ SHELF HOLES 5X 5MM HOLES 32MM SPACINGS
ALL DRAWERS TO BE *Blum Legrabox Drawer
ALL HINGES TO BE 110* BLUM SOFTCLOSE

CN FITOUTS PTY LTD
CUSTOM MADE JOINERY

P 03 9761 6994
E info@cnfitouts.com.au
www.cnfitouts.com.au

6 Stephenson rd.
Bayswater North 3153

Bed 3 Robe 3D

J1122 - 235 Esplanade



Approved CN Drawings Supersede All Other Drawings and Specs

CODE	DESCRIPTION
JO2	18mm Chifley Profile 2Pac Flannel Flower 13/65 Bauwerk Zero Gloss
HO2	Handle - Beslag Thread - Toniton Greige
HR1	Hanging Rail - White Oval
LED2	Surface Mounted LED and Profile by Others

Name: Grace Lewin

Address:
235 Esplanade East
Port Melbourne

Sheet # 8 of 13

Date: 26/10/26

Drawn By: AF

JOB STANDARD MATERIALS

UNLESS STATED OTHERWISE
INTERNAL CARCASSES TO BE:
* 16mm White - 1mm
ALL ADJ SHELF HOLES 5X 5MM HOLES 32MM SPACINGS
ALL DRAWERS TO BE *Blum Legrabox Drawer
ALL HINGES TO BE 110* BLUM SOFTCLOSE


CN FITOUTS PTY LTD
CUSTOM MADE JOINERY


P 03 9761 6994
E info@cnfitouts.com.au
www.cnfitouts.com.au


6 Stephenson rd.
Bayswater North 3153

Bed 3 Robe Plans and Elevations

J1122 - 235 Esplanade

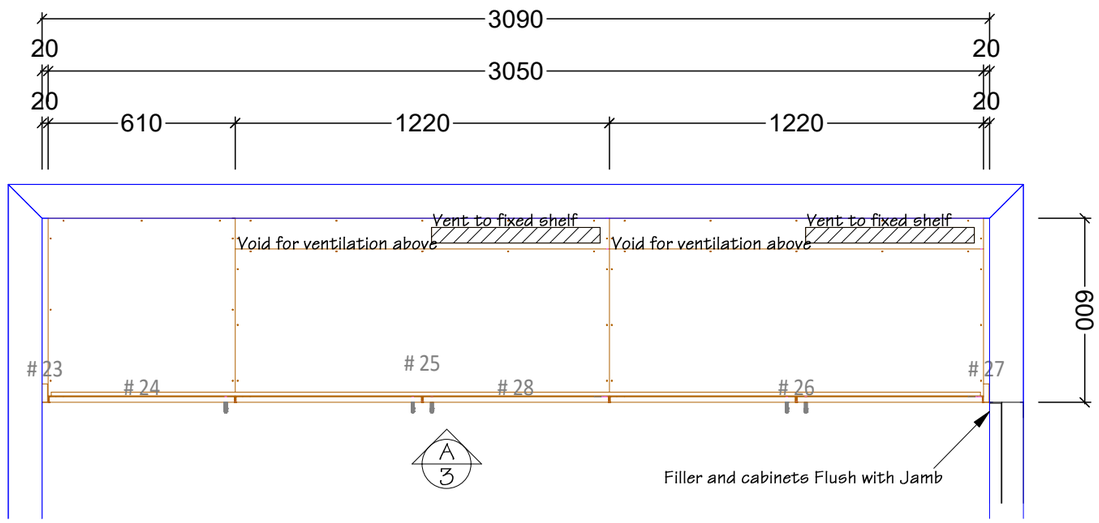

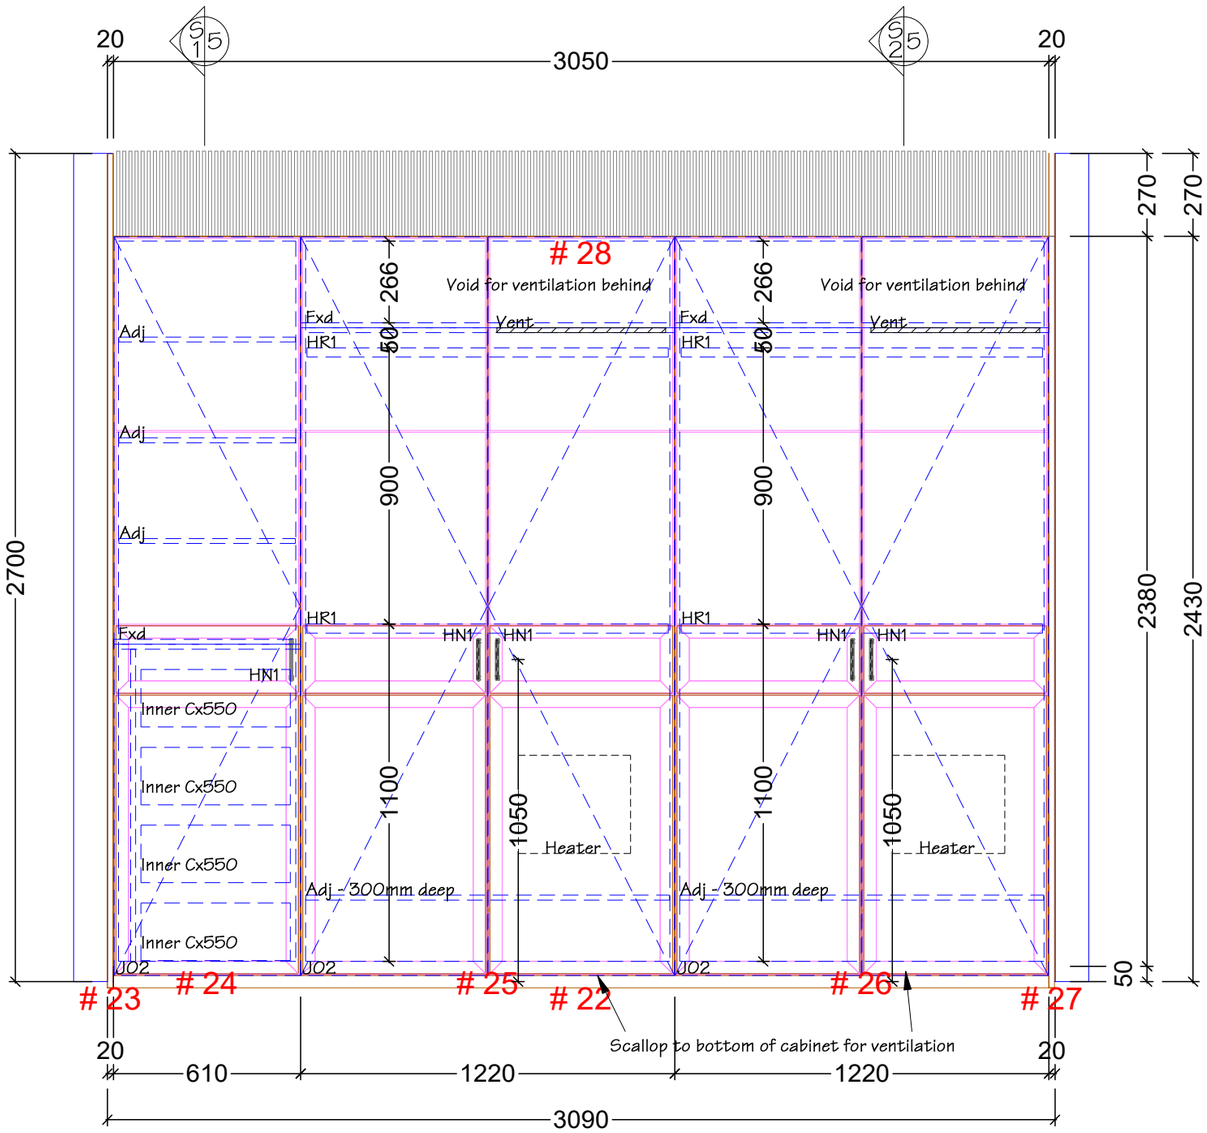

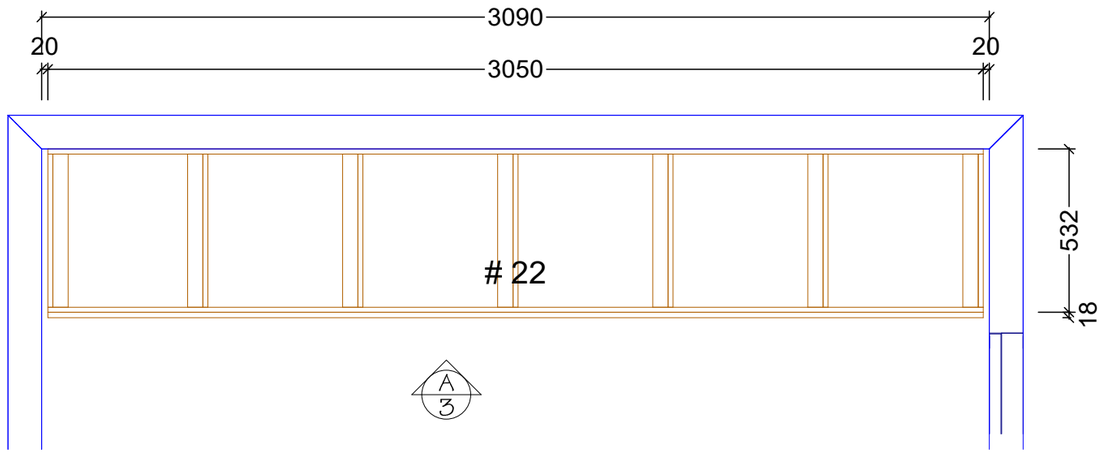

A/3 Elevation - Bed 3 Robe
Scale: 1:20

Approved CN Drawings Supersede All Other Drawings and Specs

CODE	DESCRIPTION
JO2	18mm Chifley Profile 2Pac Flannel Flower 13/65 Bauwerk Zero Gloss
HO2	Handle - Beslag Thread - Toniton Greige
HR1	Hanging Rail - White Oval
LED2	Surface Mounted LED and Profile by Others

Name: Grace Lewin

Address:
235 Esplanade East
Port Melbourne

Sheet # 9 of 13

Date: 26/10/26

Drawn By: AF

JOB STANDARD MATERIALS

UNLESS STATED OTHERWISE
INTERNAL CARCASSES TO BE:
* 16mm White - 1mm
ALL ADJ SHELF HOLES 5X 5MM HOLES 32MM SPACINGS
ALL DRAWERS TO BE *Blum Legrabox Drawer
ALL HINGES TO BE 110* BLUM SOFTCLOSE


CN FITOUTS PTY LTD
CUSTOM MADE JOINERY

P 03 9761 6994
E info@cnfitouts.com.au
www.cnfitouts.com.au


6 Stephenson rd.
Bayswater North 3153

Bed 3 Robe Sections


J1122 - 235 Esplanade

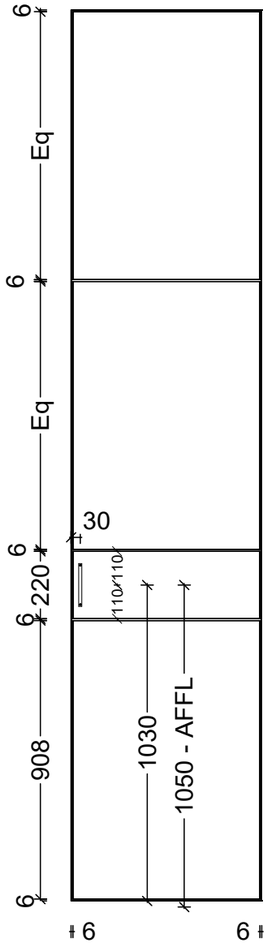

Door Typical Layout
Scale: 1:20

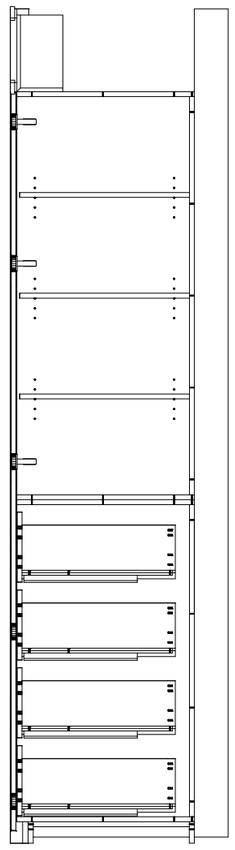

S1 / 3 Section - Bed 3 Robe
Scale: 1:20

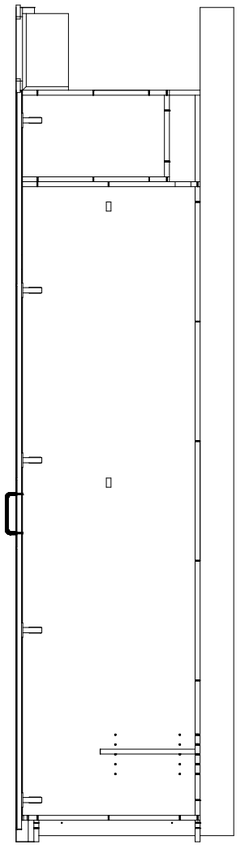

S2 / 3 Section - Bed 3 Robe
Scale: 1:20

Approved CN Drawings Supersede All Other Drawings and Specs

CODE	DESCRIPTION
JO2	18mm Chifley Profile 2Pac Flannel Flower 13/65 Bauwerk Zero Gloss
HO2	Handle - Beslag Thread - Toniton Greige
HR1	Hanging Rail - White Oval
LED2	Surface Mounted LED and Profile by Others

Name: Grace Lewin

Address:
235 Esplanade East
Port Melbourne

Sheet # 10 of 13

Date: 26/10/26

Drawn By: AF

JOB STANDARD MATERIALS

UNLESS STATED OTHERWISE
INTERNAL CARCASSES TO BE:
* 16mm White - 1mm
ALL ADJ SHELF HOLES 5X 5MM HOLES 32MM SPACINGS
ALL DRAWERS TO BE *Blum Legrabox Drawer
ALL HINGES TO BE 110* BLUM SOFTCLOSE

CN FITOUTS PTY LTD
CUSTOM MADE JOINERY

P 03 9761 6994
E info@cnfitouts.com.au
www.cnfitouts.com.au

6 Stephenson rd.
Bayswater North 3153

Bed 4 Robe 3D

J1122 - 235 Esplanade



Approved CN Drawings Supersede All Other Drawings and Specs

CODE	DESCRIPTION
JO2	18mm Chifley Profile 2Pac Flannel Flower 13/65 Bauwerk Zero Gloss
HO2	Handle - Beslag Thread - Toniton Greige
HR1	Hanging Rail - White Oval
LED2	Surface Mounted LED and Profile by Others

Name: Grace Lewin

Address:
235 Esplanade East
Port Melbourne

Sheet # 11 of 13

Date: 26/10/26

Drawn By: AF

JOB STANDARD MATERIALS

UNLESS STATED OTHERWISE
INTERNAL CARCASSES TO BE:
* 16mm White - 1mm
ALL ADJ SHELF HOLES 5X 5MM HOLES 32MM SPACINGS
ALL DRAWERS TO BE *Blum Legrabox Drawer
ALL HINGES TO BE 110* BLUM SOFTCLOSE


CN FITOUTS PTY LTD
CUSTOM MADE JOINERY


P 03 9761 6994
E info@cnfitouts.com.au
www.cnfitouts.com.au


6 Stephenson rd.
Bayswater North 3153

Bed 4 Robe Plan and Elevations

J1122 - 235 Esplanade

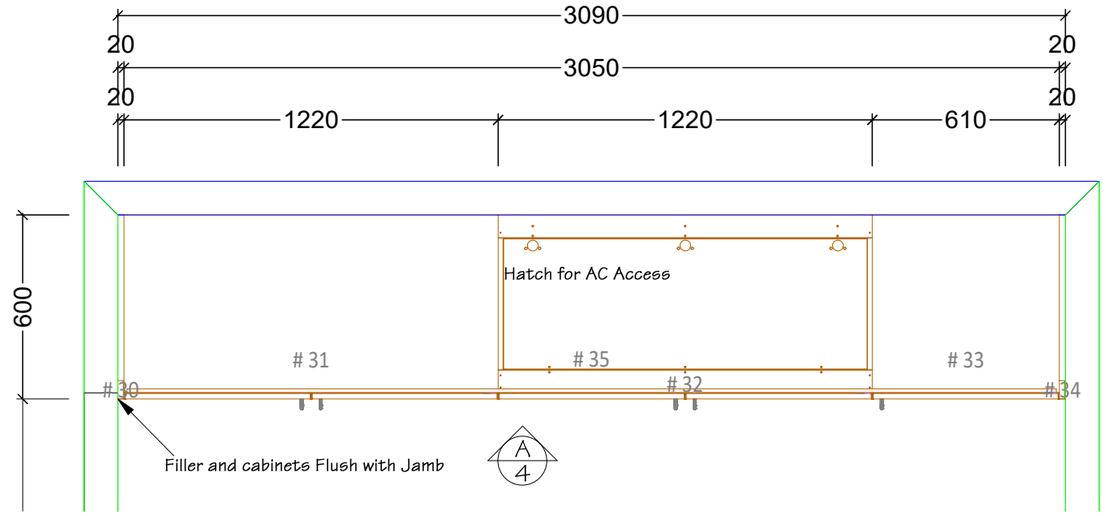

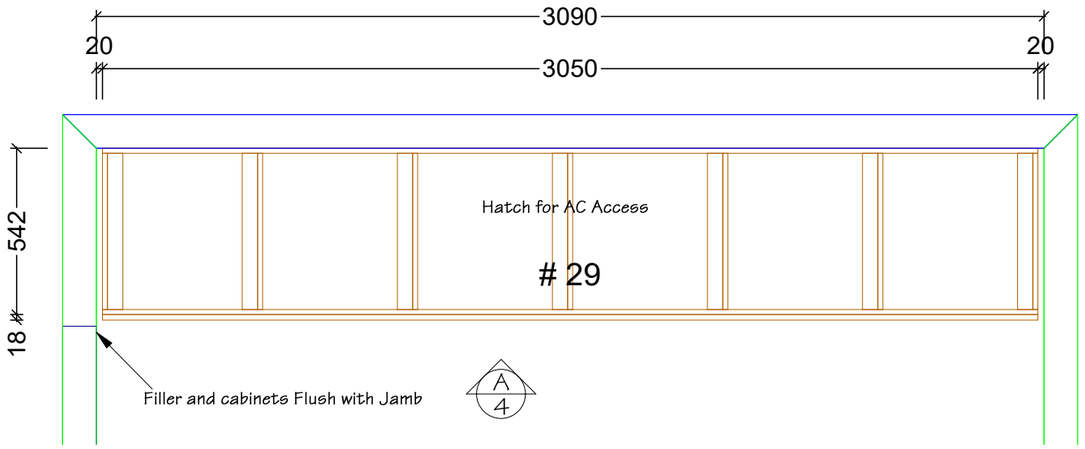

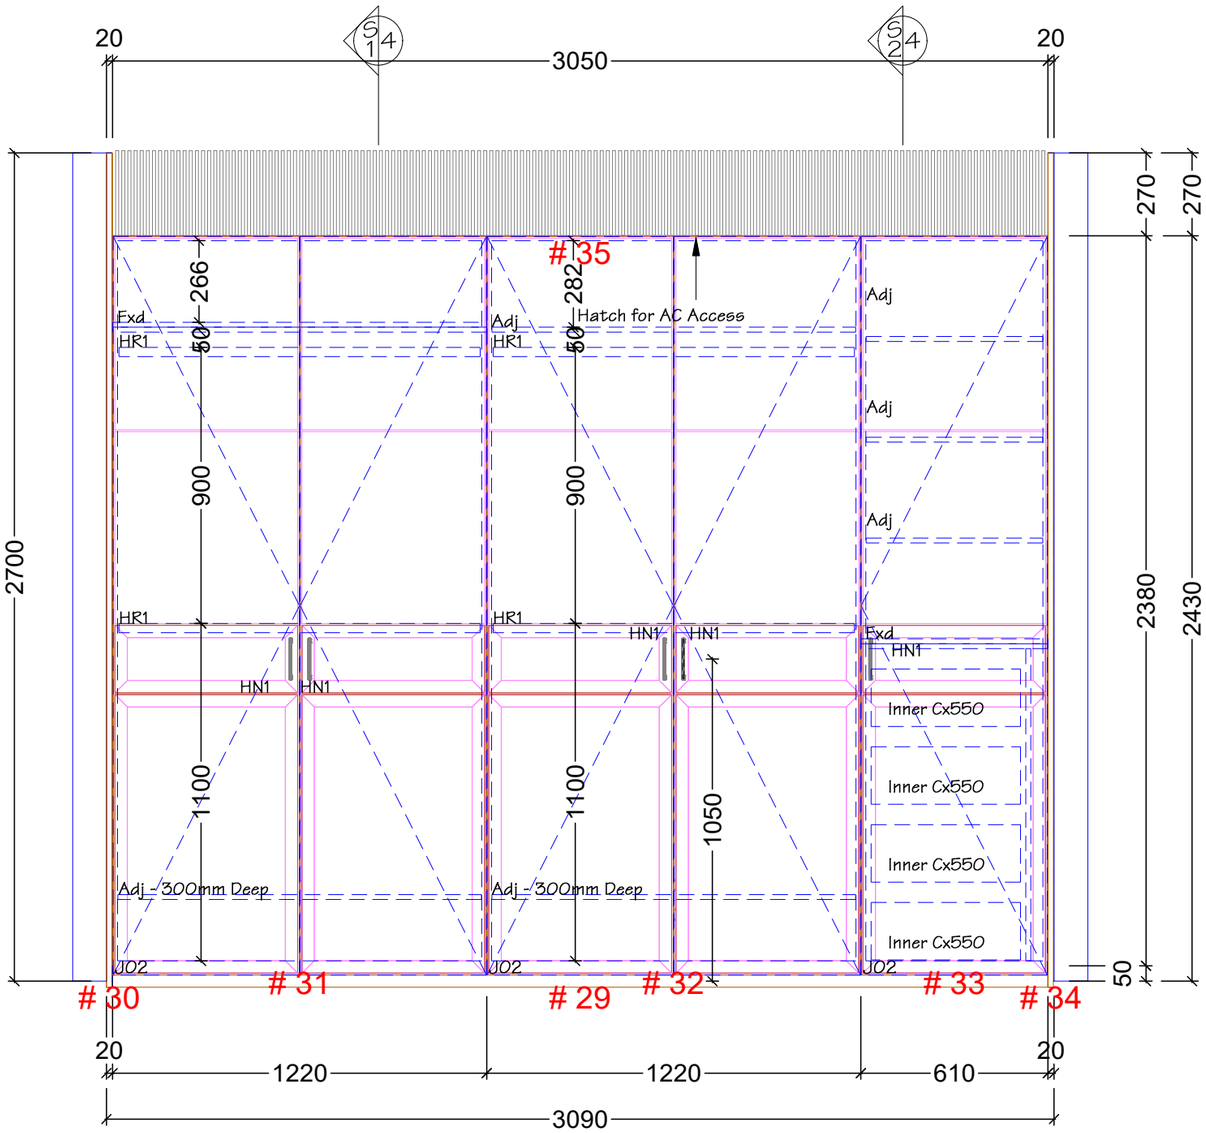

A 4 Elevation - Bed 4 Robe
Scale: 1:20

Approved CN Drawings Supersede All Other Drawings and Specs

CODE	DESCRIPTION
JO2	18mm Chifley Profile 2Pac Flannel Flower 13/65 Bauwerk Zero Gloss
HO2	Handle - Beslag Thread - Toniton Greige
HR1	Hanging Rail - White Oval
LED2	Surface Mounted LED and Profile by Others

Name: Grace Lewin

Address:
235 Esplanade East
Port Melbourne

Sheet # 12 of 13

Date: 26/10/26

Drawn By: AF

JOB STANDARD MATERIALS

UNLESS STATED OTHERWISE
INTERNAL CARCASSES TO BE:
* 16mm White - 1mm
ALL ADJ SHELF HOLES 5X 5MM HOLES 32MM SPACINGS
ALL DRAWERS TO BE *Blum Legrabox Drawer
ALL HINGES TO BE 110* BLUM SOFTCLOSE


CN FITOUTS PTY LTD
CUSTOM MADE JOINERY

P 03 9761 6994
E info@cnfitouts.com.au
www.cnfitouts.com.au


6 Stephenson rd.
Bayswater North 3153

Bed 4 Robe Sections


J1122 - 235 Esplanade

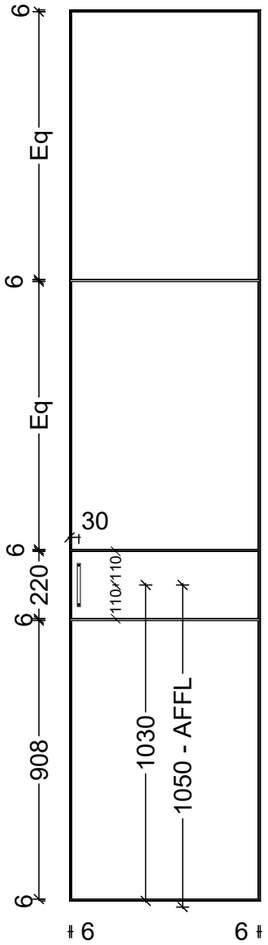

Door Typical Layout
Scale: 1:20

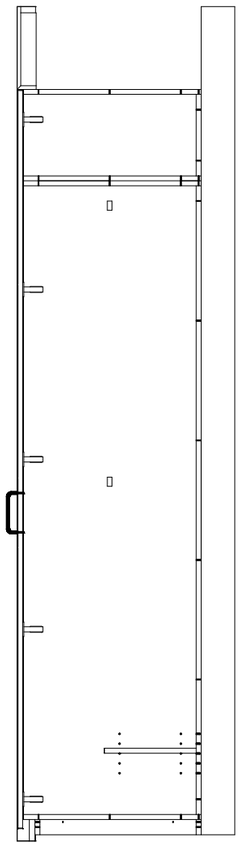

S1 / 4 Section - Bed 4 Robe
Scale: 1:20

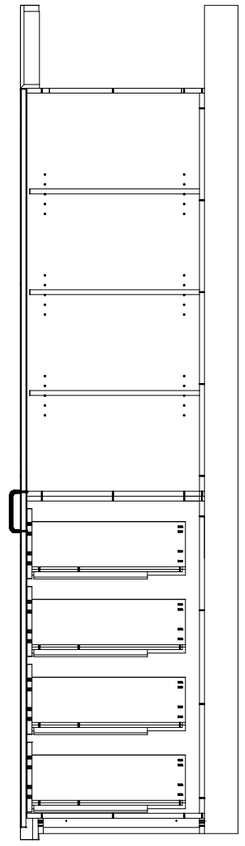

S2 / 4 Section - Bed 4 Robe
Scale: 1:20

Approved CN Drawings Supersede All Other Drawings and Specs

CODE	DESCRIPTION
JO2	18mm Chifley Profile 2Pac Flannel Flower 13/65 Bauwerk Zero Gloss
HO2	Handle - Beslag Thread - Toniton Greige
HR1	Hanging Rail - White Oval
LED2	Surface Mounted LED and Profile by Others

Name: Grace Lewin

Address:
235 Esplanade East
Port Melbourne

Sheet # 13 of 13

Date: 26/10/26

Drawn By: AF

JOB STANDARD MATERIALS

UNLESS STATED OTHERWISE
INTERNAL CARCASSES TO BE:
* 16mm White - 1mm
ALL ADJ SHELF HOLES 5X 5MM HOLES 32MM SPACINGS
ALL DRAWERS TO BE *Blum Legrabox Drawer
ALL HINGES TO BE 110* BLUM SOFTCLOSE

CN FITOUTS PTY LTD
CUSTOM MADE JOINERY

P 03 9761 6994
E info@cnfitouts.com.au
www.cnfitouts.com.au

6 Stephenson rd.
Bayswater North 3153