
Fillers set back 20mm - Shadowline

J936 - Barry St Basement

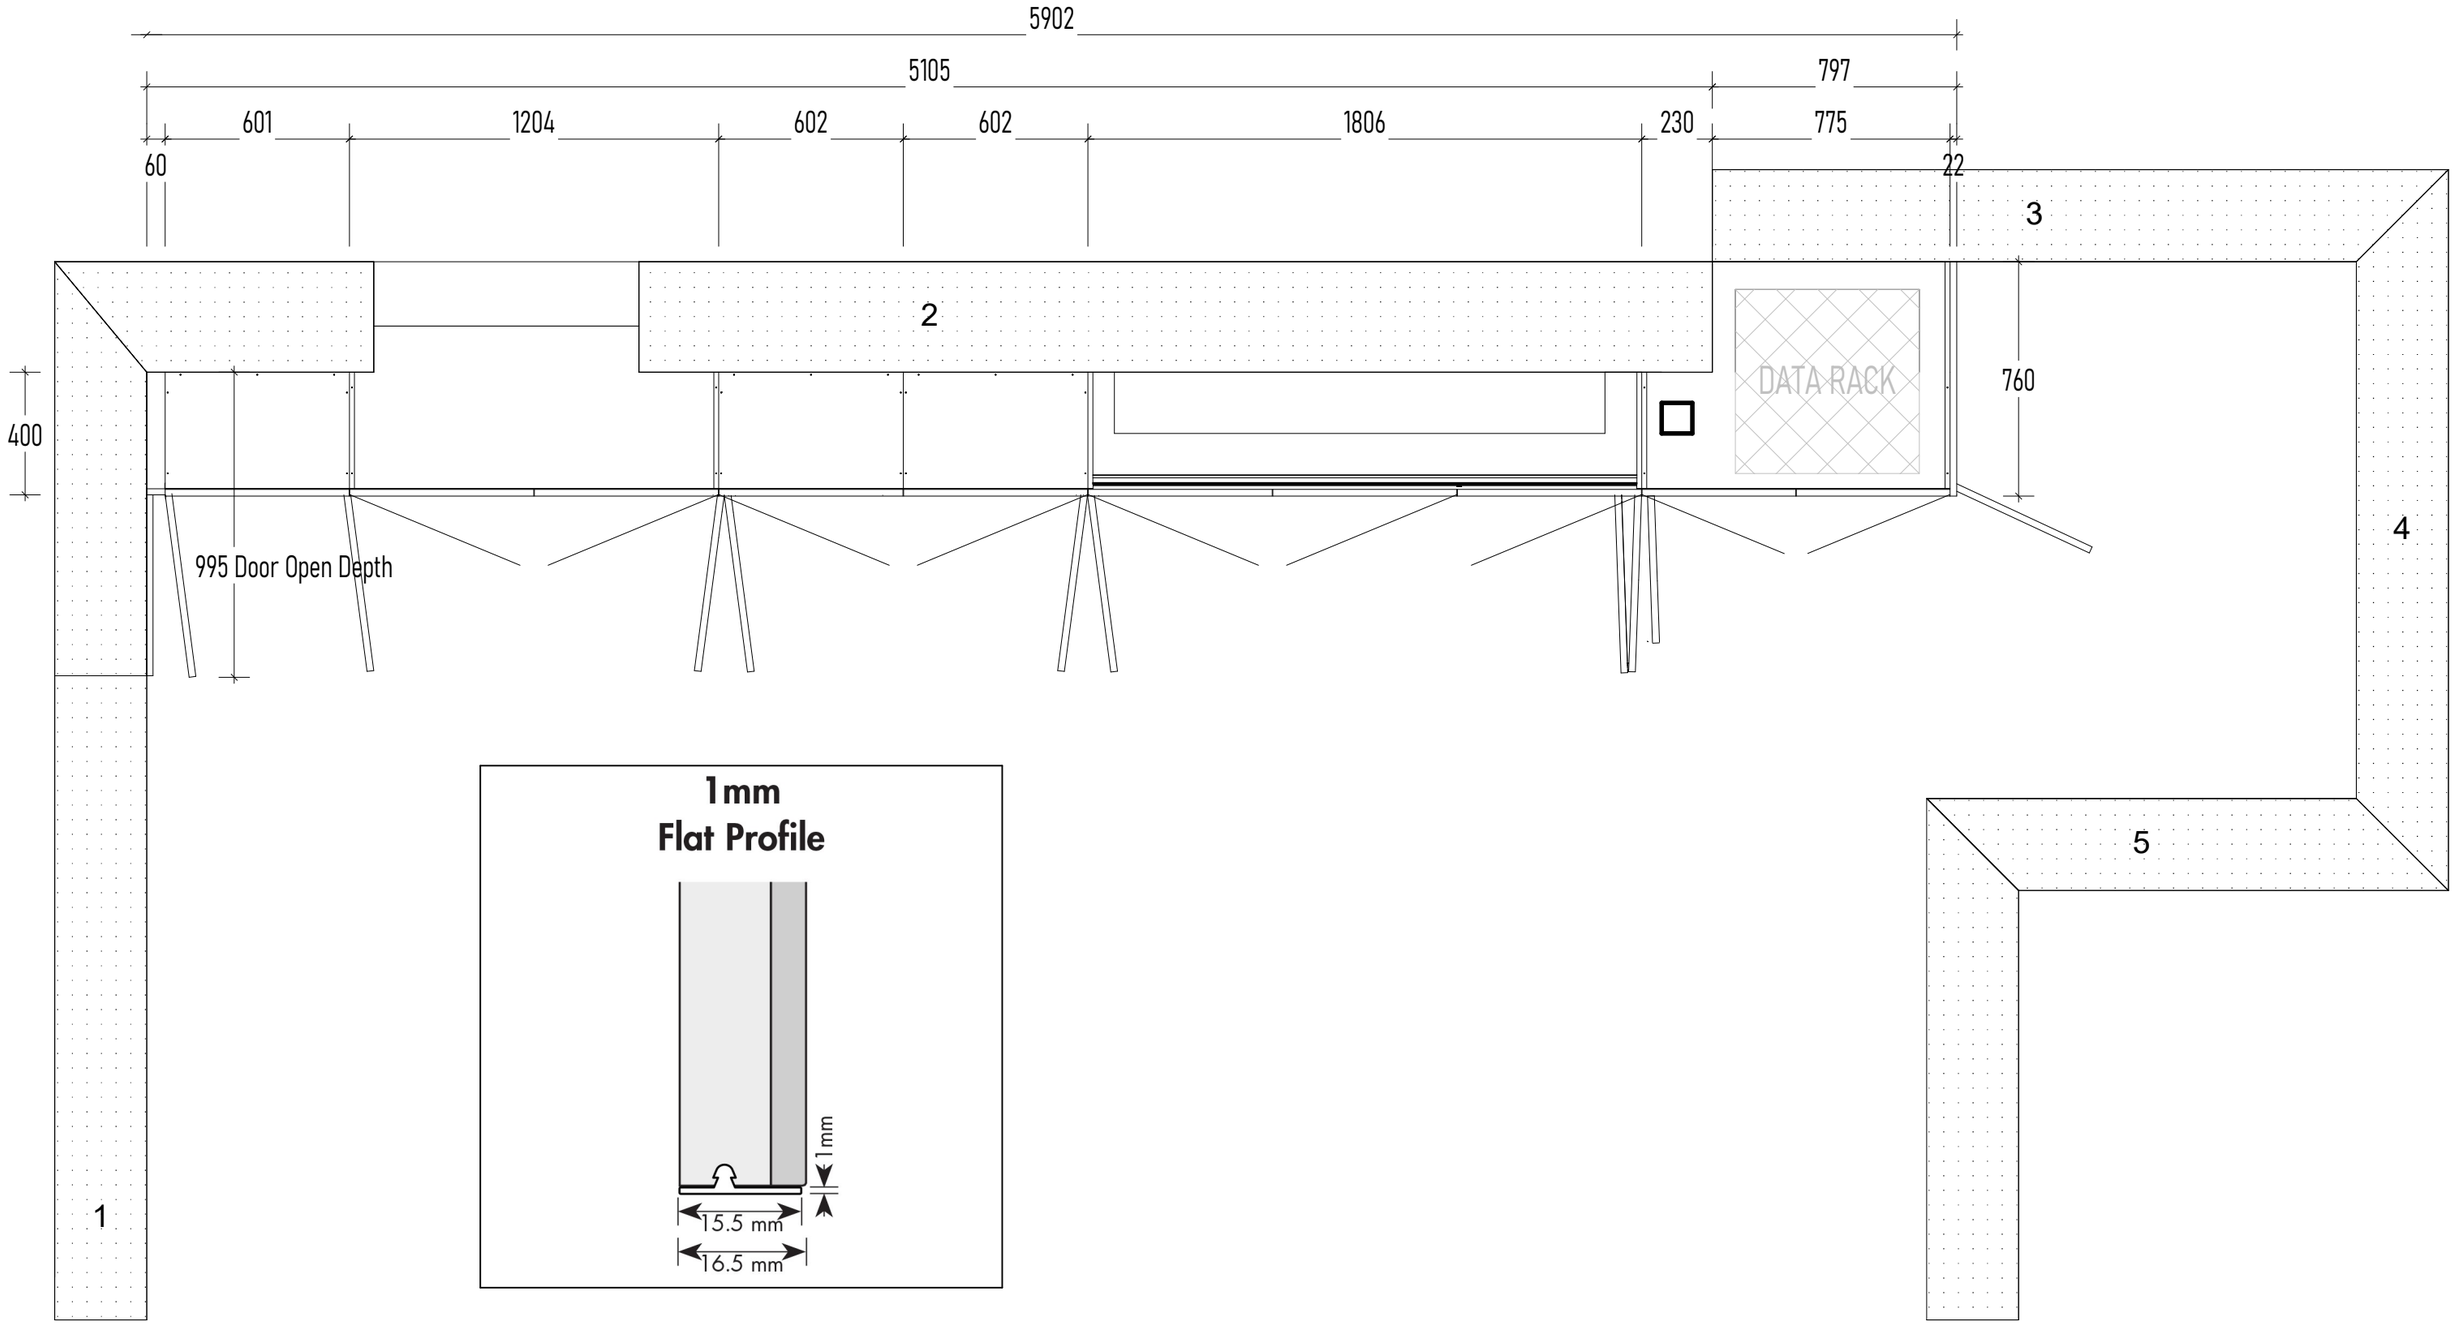

Garage Cabinets Plan

Scale: 1 : 20

CN FITOUTS PTY LTD
CUSTOM MADE JOINERY

P 03 9761 6994
E info@cnfitouts.com.au
www.cnfitouts.com.au

6 Stephenson rd.
Bayswater North 3153

CODE	DESCRIPTION
PF-1	18MM 2PAC Painted 'Colour match to Resene Taupe Grey 1/2 strength 30% Satin'
PF-3	18mm 2PAC Painted 'Dulux Haast 1/2 Strength 30% Satin'
PF-5	18mm 2PAC Painted 'Matt Black 30% Satin'
MR-1	16MM POLYTEC 1mm BLACK ANNODISED PROFILE W SMOKEY GREY MIRROR DOOR - BLACK BACKING
ST-2	20MM STONE - ESMERELDA HONED (BLOCK 402 - BATCH F4650)
ST-4	20mm Black Zimbabwe rough cut finish granite
HD1	20mm New York Marble - Backlit LED
DRW	200mm SATIN CHROME LIP PULL
ADJ	BLUM LEGRABOX
FXD	ADJUSTABLE SHELF
	FIXED SHELF

ALL JOINERY

ALL CARCASSES TO BE MADE FROM 16mm HMR White - 1mm Edge

ALL ADJ SHELF HOLES 5X 5MM HOLES 32MM SPACINGS

ALL DRAWERS TO BE Blum Legrabox Drawer


ALL HINGES TO BE 110° BLUM SOFTCLOSE

ALL HANDLES No Pulls/Knobs

Name: Manchen Projects	Phone:
Address: 21 Barry St	Sheet #16 of 29
City: Kew	Date: 16/10/26
J936 - Barry St Basement	DRAWN MH

Fillers set back 20mm - Shadowline

J936 - Barry St Basement

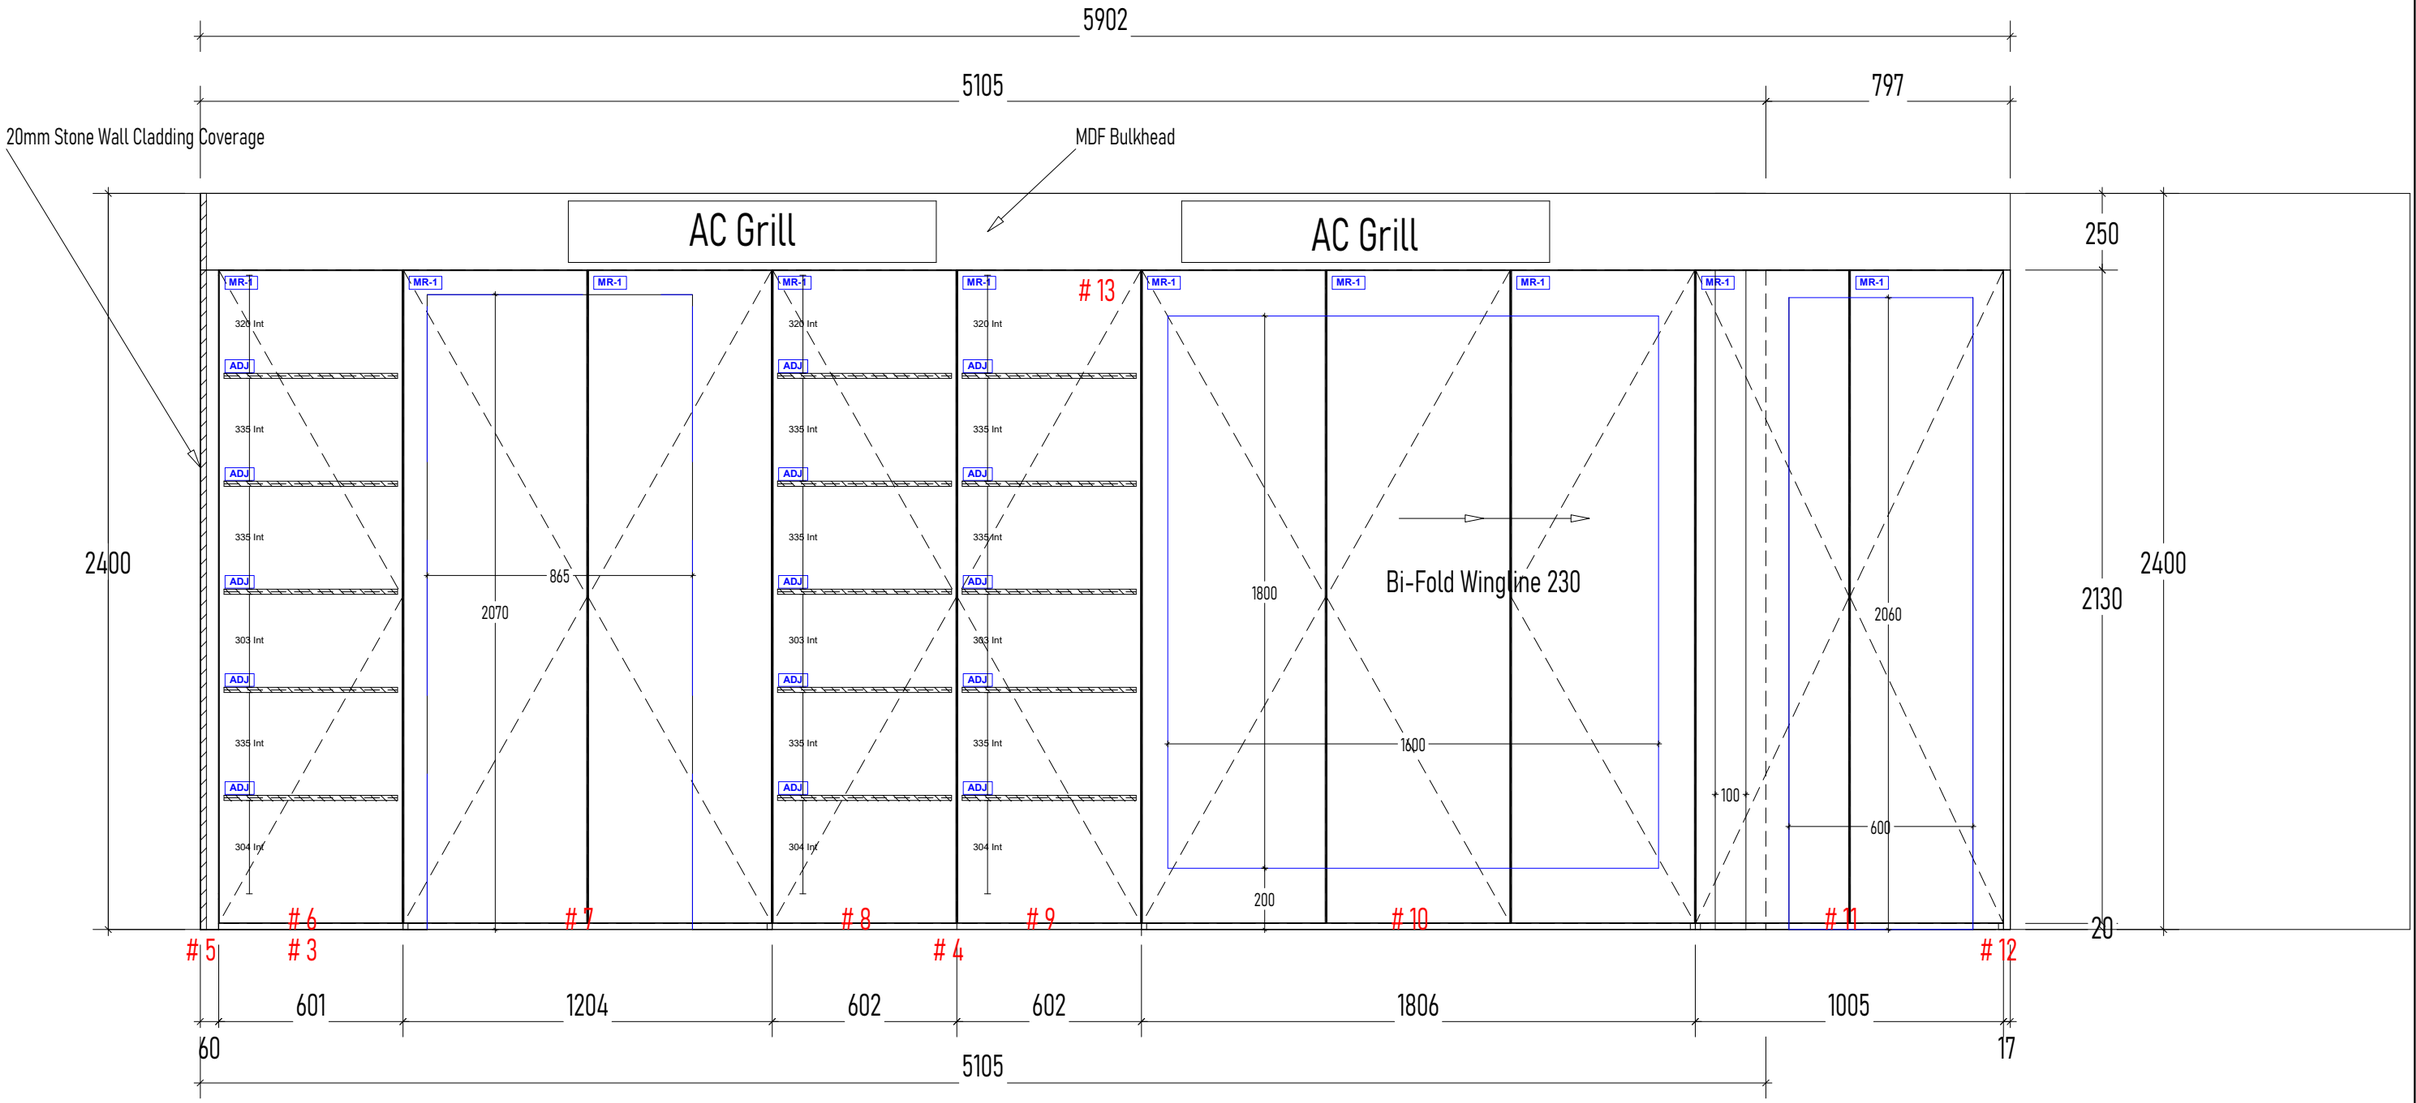

16mm Black Texture Internals

CN FITOUTS PTY LTD
CUSTOM MADE JOINERY

P 03 9761 6994
E info@cnfitouts.com.au
www.cnfitouts.com.au

6 Stephenson rd.
Bayswater North 3153

CODE	DESCRIPTION
PF-1	18MM 2PAC Painted 'Colour match to Resene Taupe Grey 1/2 strength 30% Satin'
PF-3	18mm 2PAC Painted 'Dulux Haast 1/2 Strength 30% Satin'
PF-5	18mm 2PAC Painted 'Matt Black 30% Satin'
MR-1	16MM POLYTEC 1mm BLACK ANNODISED PROFILE W SMOKEY GREY MIRROR DOOR - BLACK BACKING
ST-2	20MM STONE - ESMERELDA HONED (BLOCK 402 - BATCH F4650)
ST-4	20mm Black Zimbabwe rough cut finish granite
HD1	20mm New York Marble - Backlit LED
DRW	200mm SATIN CHROME LIP PULL
ADJ	BLUM LEGRABOX
FXD	ADJUSTABLE SHELF
	FIXED SHELF

ALL JOINERY

ALL CARCASSES TO BE MADE FROM 16mm HMR White - 1mm Edge

ALL ADJ SHELF HOLES 5X 5MM HOLES 32MM SPACINGS

ALL DRAWERS TO BE Blum Legrabox Drawer


ALL HINGES TO BE 110° BLUM SOFTCLOSE

ALL HANDLES No Pulls/Knobs


Name: Manchen Projects	Phone:
Address: 21 Barry St	Sheet #17 of 29
City: Kew	Date: 16/10/26
J936 - Barry St Basement	DRAWN MH

Fillers set back 20mm - Shadowline


J936 - Barry St Basement

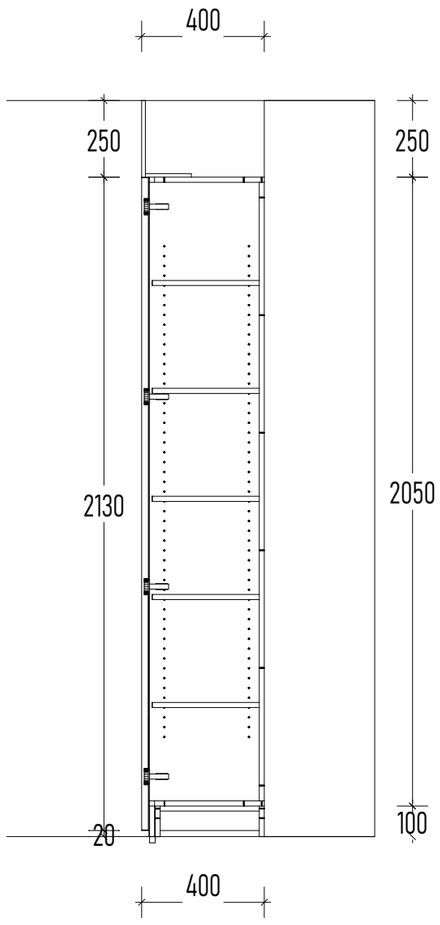


Adj Shelf Cabinet X-Sec
Scale: 1 : 20

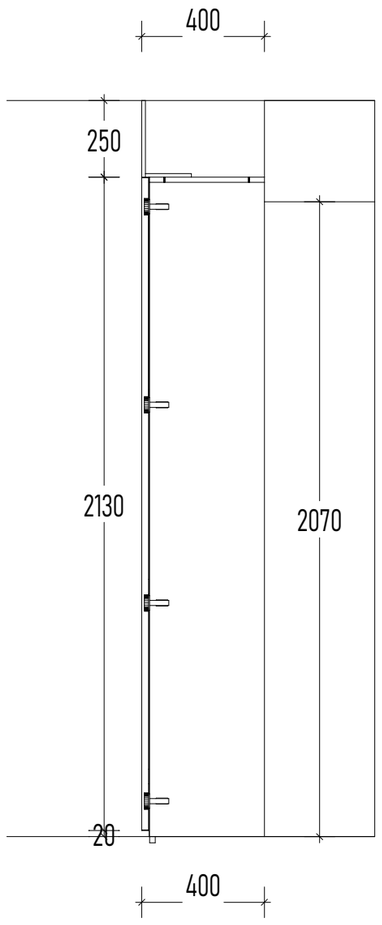


Storage Walk Thru Cabinet X-Sec
Scale: 1 : 20

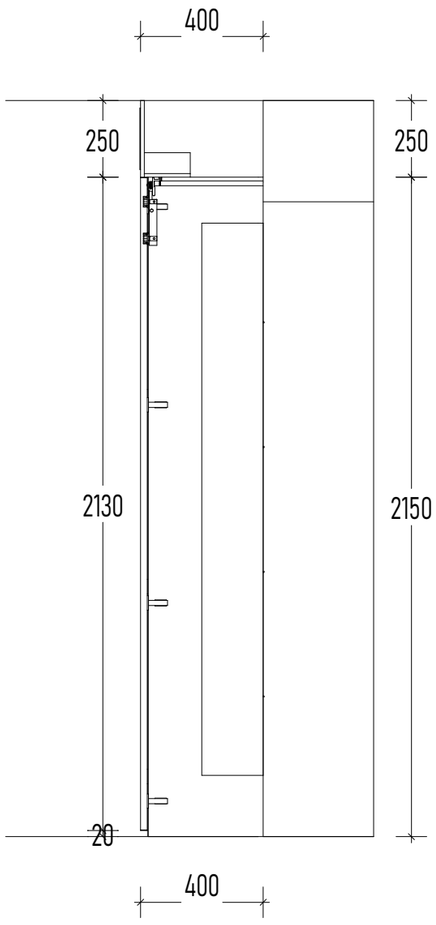

Switchboard Cabinet X-Sec
Scale: 1 : 20

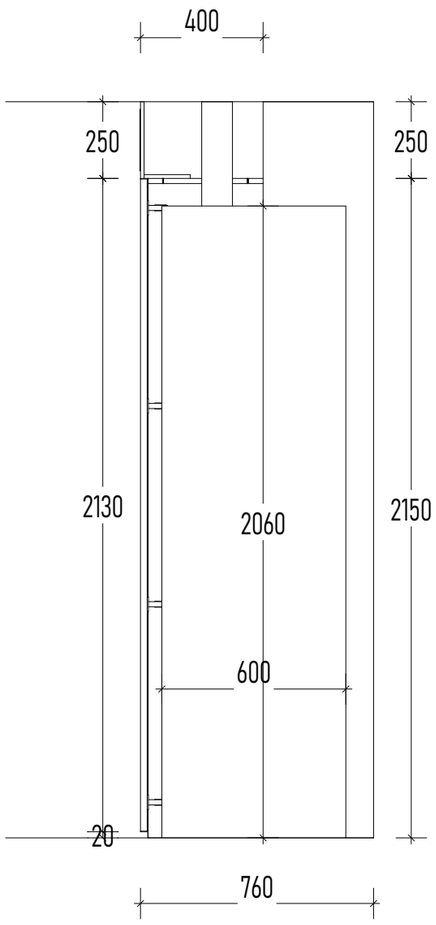

Data Rack Cabinet X-Sec
Scale: 1 : 20

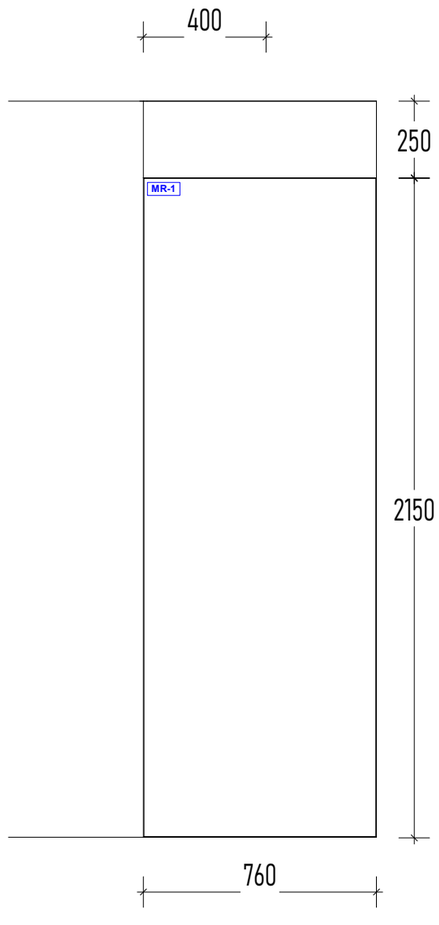

End Panel/View fron Lift X-Sec
Scale: 1 : 20

CN FITOUTS PTY LTD
CUSTOM MADE JOINERY

P 03 9761 6994
E info@cnfitouts.com.au
www.cnfitouts.com.au

6 Stephenson rd.
Bayswater North 3153

CODE	DESCRIPTION
PF-1	18MM 2PAC Painted 'Colour match to Resene Taupe Grey 1/2 strength 30% Satin'
PF-3	18mm 2PAC Painted 'Dulux Haast 1/2 Strength 30% Satin'
PF-5	18mm 2PAC Painted 'Matt Black 30% Satin'
MR-1	16MM POLYTEC 1mm BLACK ANNODISED PROFILE W SMOKEY GREY MIRROR DOOR - BLACK BACKING
ST-2	20MM STONE - ESMERELDA HONED (BLOCK 402 - BATCH F4650)
ST-4	20mm Black Zimbabwe rough cut finish granite
HD1	20mm New York Marble - Backlit LED
DRW	200mm SATIN CHROME LIP PULL
ADJ	BLUM LEGRABOX
FXD	ADJUSTABLE SHELF
	FIXED SHELF

ALL JOINERY

ALL CARCASSES TO BE MADE FROM 16mm HMR White - 1mm Edge

ALL ADJ SHELF HOLES 5X 5MM HOLES 32MM SPACINGS

ALL DRAWERS TO BE Blum Legrabox Drawer

ALL HINGES TO BE 110° BLUM SOFTCLOSE

ALL HANDLES No Pulls/Knobs

Name: Manchen Projects | Phone:

Address: 21 Barry St | Sheet #18 of 29

City: Kew | Date: 16/10/26

J936 - Barry St Basement | DRAWN MH

Fillers set back 20mm - Shadowline



CN FITOUTS PTY LTD
CUSTOM MADE JOINERY

P 03 9761 6994
E info@cnfitouts.com.au
www.cnfitouts.com.au

6 Stephenson rd.
Bayswater North 3153

CODE	DESCRIPTION
PF-1	18MM 2PAC Painted 'Colour match to Resene Taupe Grey 1/2 strength 30% Satin'
PF-3	18mm 2PAC Painted 'Dulux Haast 1/2 Strength 30% Satin'
PF-5	18mm 2PAC Painted 'Matt Black 30% Satin'
MR-1	16MM POLYTEC 1mm BLACK ANNODISED PROFILE W SMOKEY GREY MIRROR DOOR - BLACK BACKING
ST-2	20MM STONE - ESMERELDA HONED (BLOCK 402 - BATCH F4650)
ST-4	20mm Black Zimbabwe rough cut finish granite
HD1	20mm New York Marble - Backlit LED
DRW	200mm SATIN CHROME LIP PULL
ADJ	BLUM LEGRABOX
FXD	ADJUSTABLE SHELF
	FIXED SHELF

ALL JOINERY

ALL CARCASSES TO BE MADE FROM 16mm HMR White - 1mm Edge

ALL ADJ SHELF HOLES 5X 5MM HOLES 32MM SPACINGS

ALL DRAWERS TO BE Blum Legrabox Drawer

ALL HINGES TO BE 110° BLUM SOFTCLOSE

ALL HANDLES No Pulls/Knobs

Name: Manchen Projects | Phone:

Address: 21 Barry St | Sheet #19 of 29

City: Kew | Date: 16/10/26

J936 - Barry St Basement | DRAWN MH

Fillers set back 20mm - Shadowline



16mm Black Texture Internals

CN FITOUTS PTY LTD
CUSTOM MADE JOINERY

P 03 9761 6994
E info@cnfitouts.com.au
www.cnfitouts.com.au

6 Stephenson rd.
Bayswater North 3153

CODE	DESCRIPTION
PF-1	18MM 2PAC Painted 'Colour match to Resene Taupe Grey 1/2 strength 30% Satin'
PF-3	18mm 2PAC Painted 'Dulux Haast 1/2 Strength 30% Satin'
PF-5	18mm 2PAC Painted 'Matt Black 30% Satin'
MR-1	16MM POLYTEC 1mm BLACK ANNODISED PROFILE W SMOKEY GREY MIRROR DOOR - BLACK BACKING
ST-2	20MM STONE - ESMERELDA HONED (BLOCK 402 - BATCH F4650)
ST-4	20mm Black Zimbabwe rough cut finish granite
HD1	20mm New York Marble - Backlit LED
DRW	200mm SATIN CHROME LIP PULL
ADJ	BLUM LEGRABOX
FXD	ADJUSTABLE SHELF
	FIXED `SHELF

ALL JOINERY

ALL CARCASSES TO BE MADE FROM 16mm HMR White - 1mm Edge

ALL ADJ SHELF HOLES 5X 5MM HOLES 32MM SPACINGS

ALL DRAWERS TO BE Blum Legrabox Drawer

ALL HINGES TO BE 110* BLUM SOFTCLOSE

ALL HANDLES No Pulls/Knobs

Name: Manchen Projects | Phone:

Address: 21 Barry St | Sheet #20 of 29

City: Kew | Date: 16/10/26

J936 - Barry St Basement | DRAWN MH