
Fillers set back 20mm - Shadowline

J936 - Barry St Basement

A - L

A - R

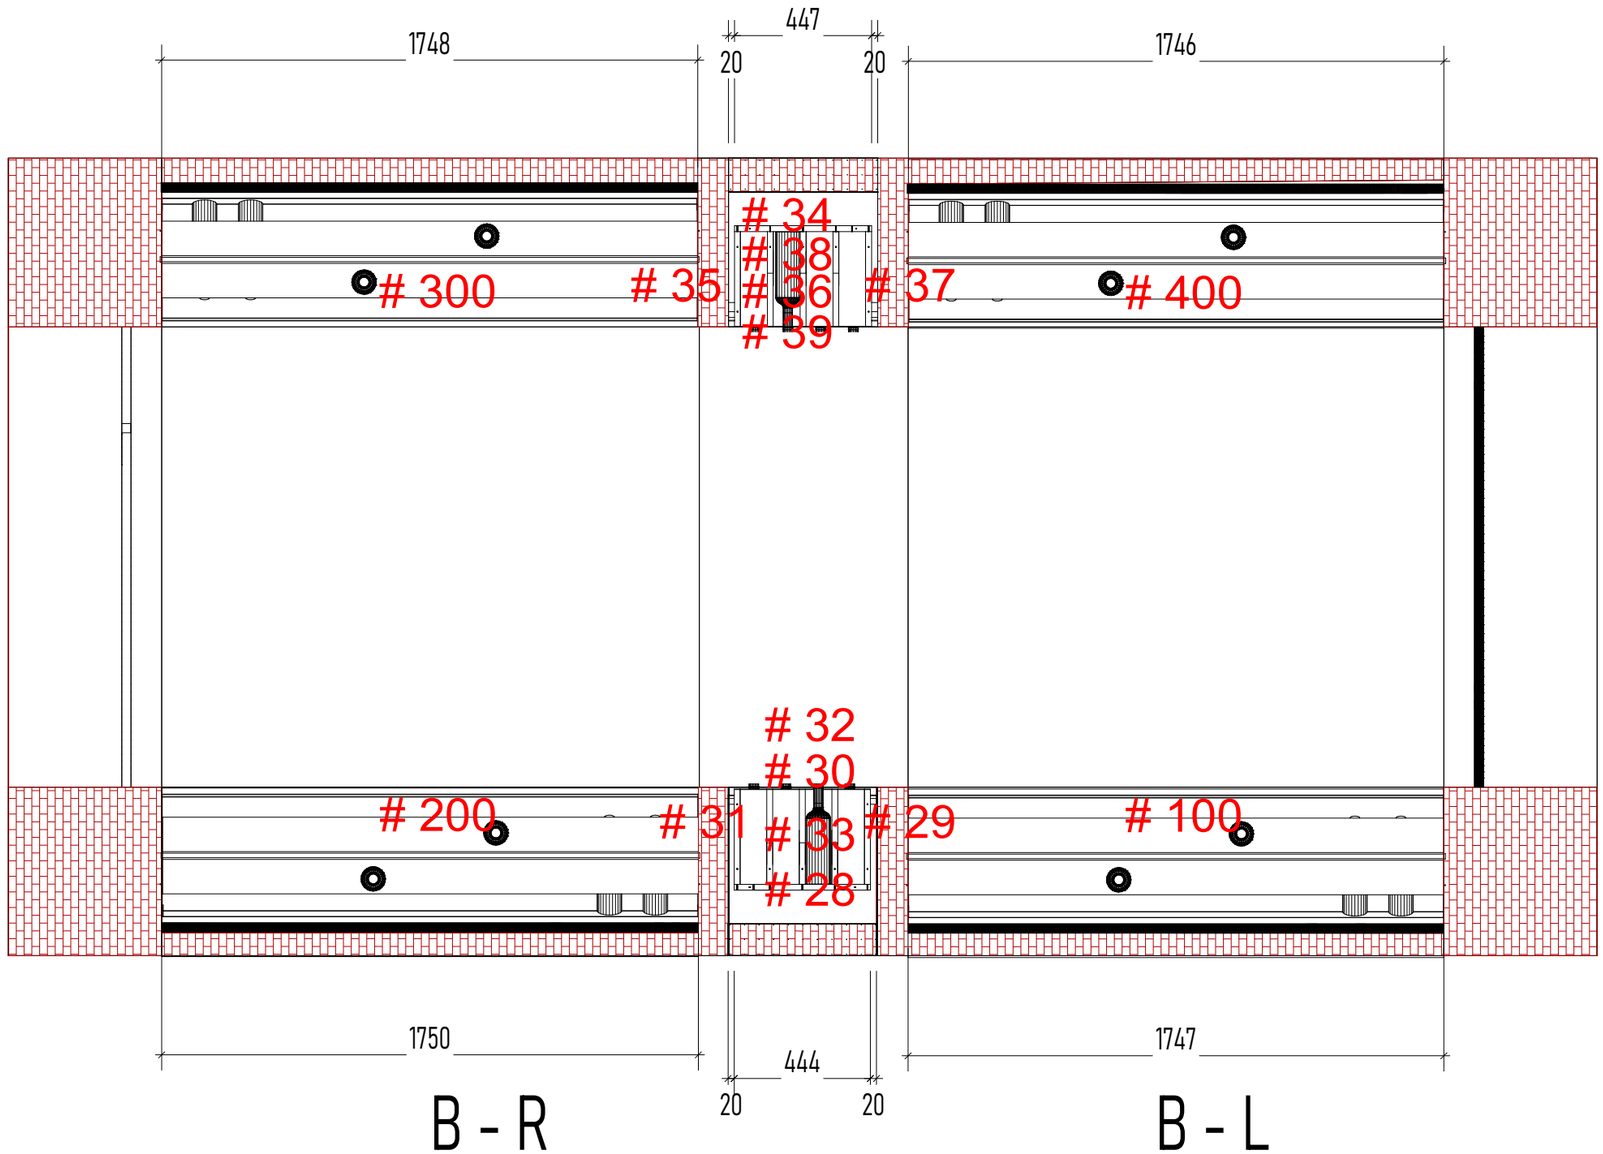

ENTRY DOOR

DRIVEWAY

B - R

B - L

Wine Cellar Plan

Scale: 1 : 20

CN FITOUTS PTY LTD
CUSTOM MADE JOINERY

P 03 9761 6994
E info@cnfitouts.com.au
www.cnfitouts.com.au

6 Stephenson rd.
Bayswater North 3153

CODE	DESCRIPTION
PF-1	18MM 2PAC Painted 'Colour match to Resene Taupe Grey 1/2 strength 30% Satin'
PF-3	18mm 2PAC Painted 'Dulux Haast 1/2 Strength 30% Satin'
PF-5	18mm 2PAC Painted 'Matt Black 30% Satin'
MR-1	16MM POLYTEC 1mm BLACK ANNODISED PROFILE W SMOKEY GREY MIRROR DOOR - BLACK BACKING
ST-2	20MM STONE - ESMERELDA HONED (BLOCK 402 - BATCH F4650)
ST-4	20mm Black Zimbabwe rough cut finish granite
HD1	20mm New York Marble - Backlit LED
DRW	200mm SATIN CHROME LIP PULL
ADJ	BLUM LEGRABOX
FXD	ADJUSTABLE SHELF
	FIXED SHELF

ALL JOINERY

ALL CARCASSES TO BE MADE FROM 16mm HMR White - 1mm Edge

ALL ADJ SHELF HOLES 5X 5MM HOLES 32MM SPACINGS

ALL DRAWERS TO BE Blum Legrabox Drawer


ALL HINGES TO BE 110° BLUM SOFTCLOSE


ALL HANDLES No Pulls/Knobs

Name: Manchen Projects	Phone:
Address: 21 Barry St	Sheet # 4 of 29
City: Kew	Date: 16/10/26
J936 - Barry St Basement	DRAWN MH


Fillers set back 20mm - Shadowline

J936 - Barry St Basement

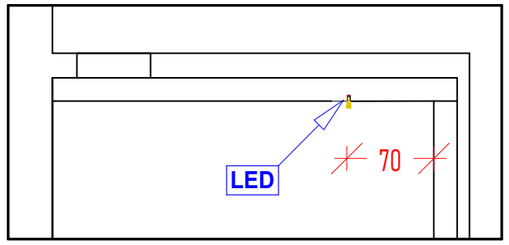


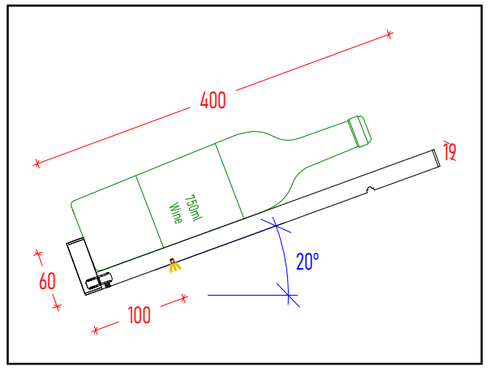


LED Detail
Scale: 1 : 5

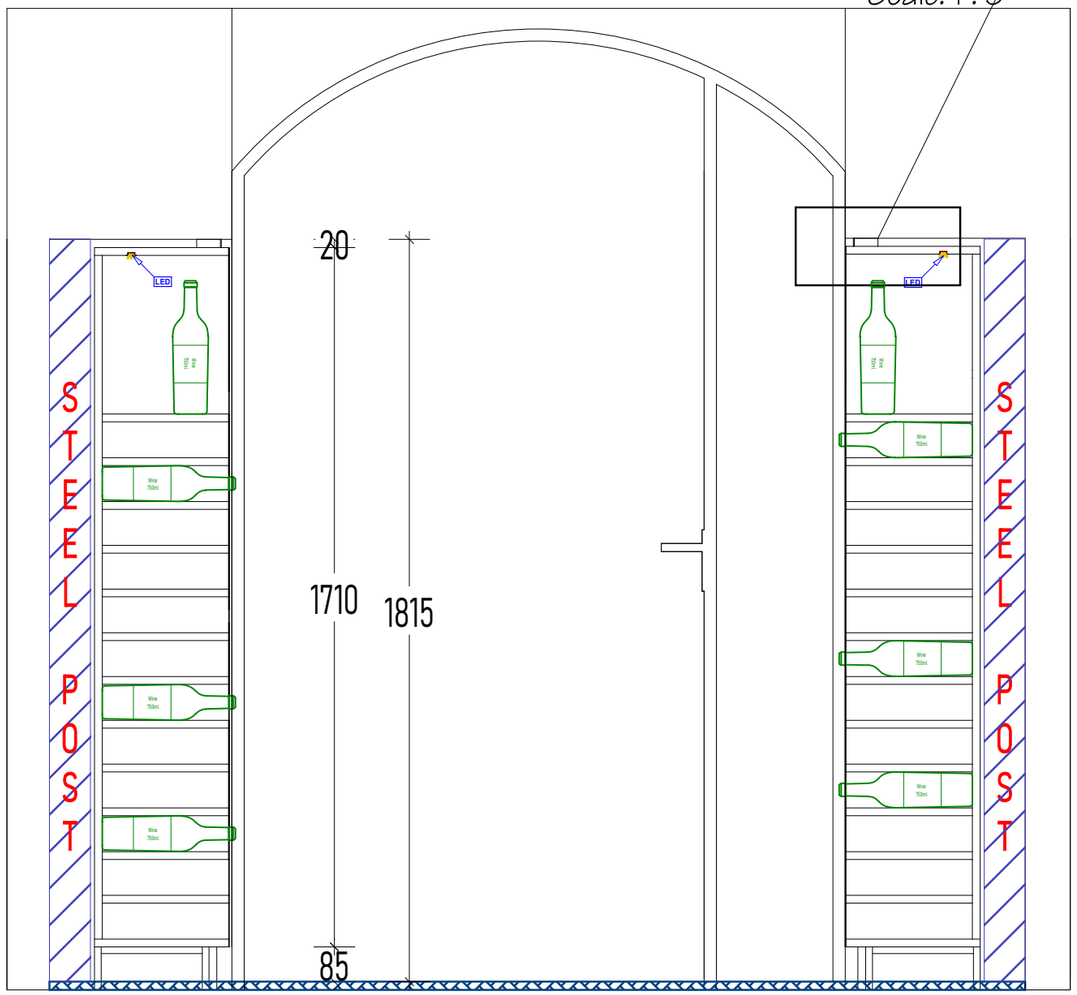

Wine Cellar XSec
Scale: 1 : 15

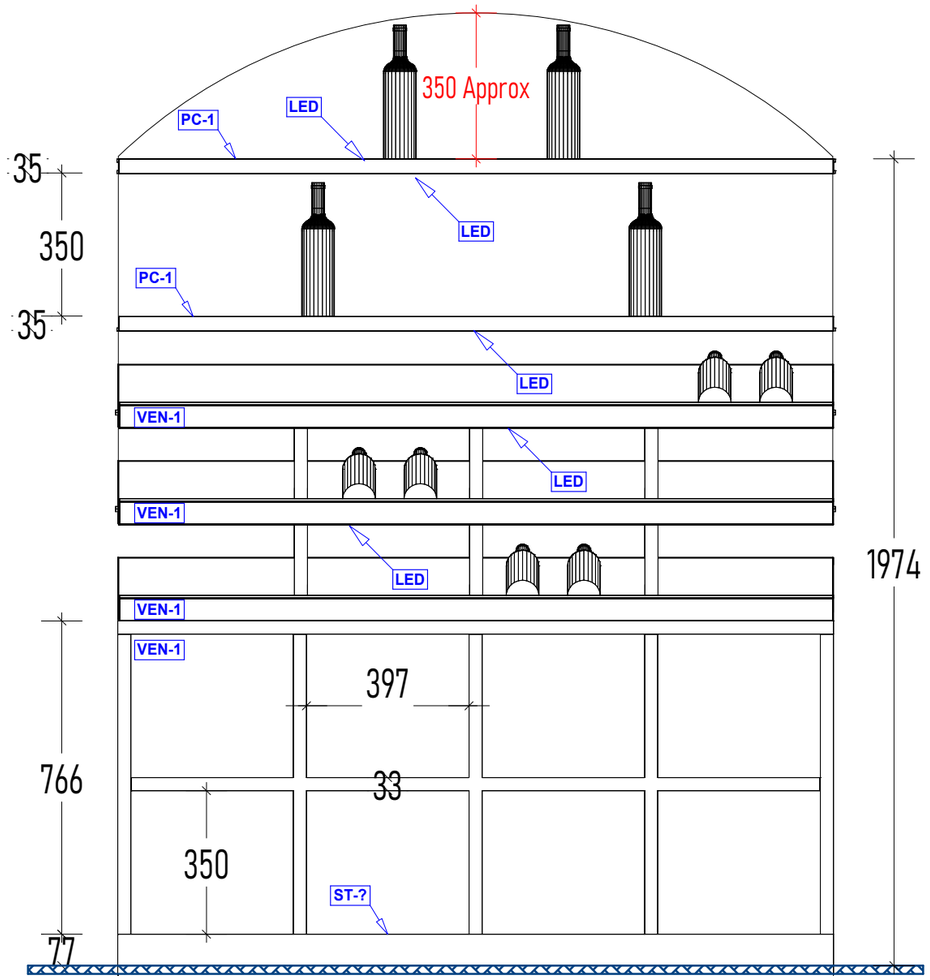

Wine Cellar Typical Elevation A
Scale: 1 : 15

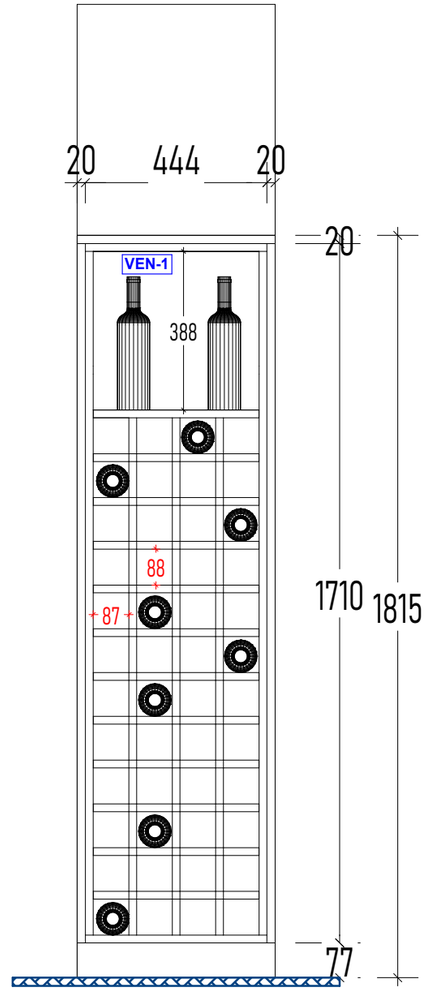


Wine Cellar Typical Elevation B
Scale: 1 : 15

CN FITOUTS PTY LTD
CUSTOM MADE JOINERY

P 03 9761 6994
E info@cnfitouts.com.au
www.cnfitouts.com.au

6 Stephenson rd.
Bayswater North 3153

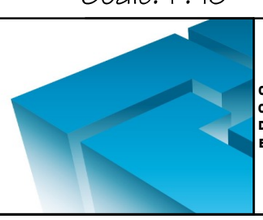

CODE	DESCRIPTION
PF-1	18MM 2PAC Painted 'Colour match to Resene Taupe Grey 1/2 strength 30% Satin'
PF-3	18mm 2PAC Painted 'Dulux Haast 1/2 Strength 30% Satin'
PF-5	18mm 2PAC Painted 'Matt Black 30% Satin'
MR-1	16MM POLYTEC 1mm BLACK ANNODISED PROFILE W SMOKEY GREY MIRROR DOOR - BLACK BACKING
ST-2	20MM STONE - ESMERELDA HONED (BLOCK 402 - BATCH F4650)
ST-4	20mm Black Zimbabwe rough cut finish granite
HD1	20mm New York Marble - Backlit LED
DRW	200mm SATIN CHROME LIP PULL
ADJ	BLUM LEGRABOX
FXD	ADJUSTABLE SHELF
	FIXED SHELF

ALL JOINERY

ALL CARCASSES TO BE MADE FROM 16mm HMR White - 1mm Edge

ALL ADJ SHELF HOLES 5X 5MM HOLES 32MM SPACINGS

ALL DRAWERS TO BE Blum Legrabox Drawer

ALL HINGES TO BE 110° BLUM SOFTCLOSE

ALL HANDLES No Pulls/Knobs

Name: Manchen Projects | Phone:


Address: 21 Barry St | Sheet # 5 of 29


City: Kew | Date: 16/10/26

J936 - Barry St Basement | DRAWN MH

Fillers set back 20mm - Shadowline

J936 - Barry St Basement

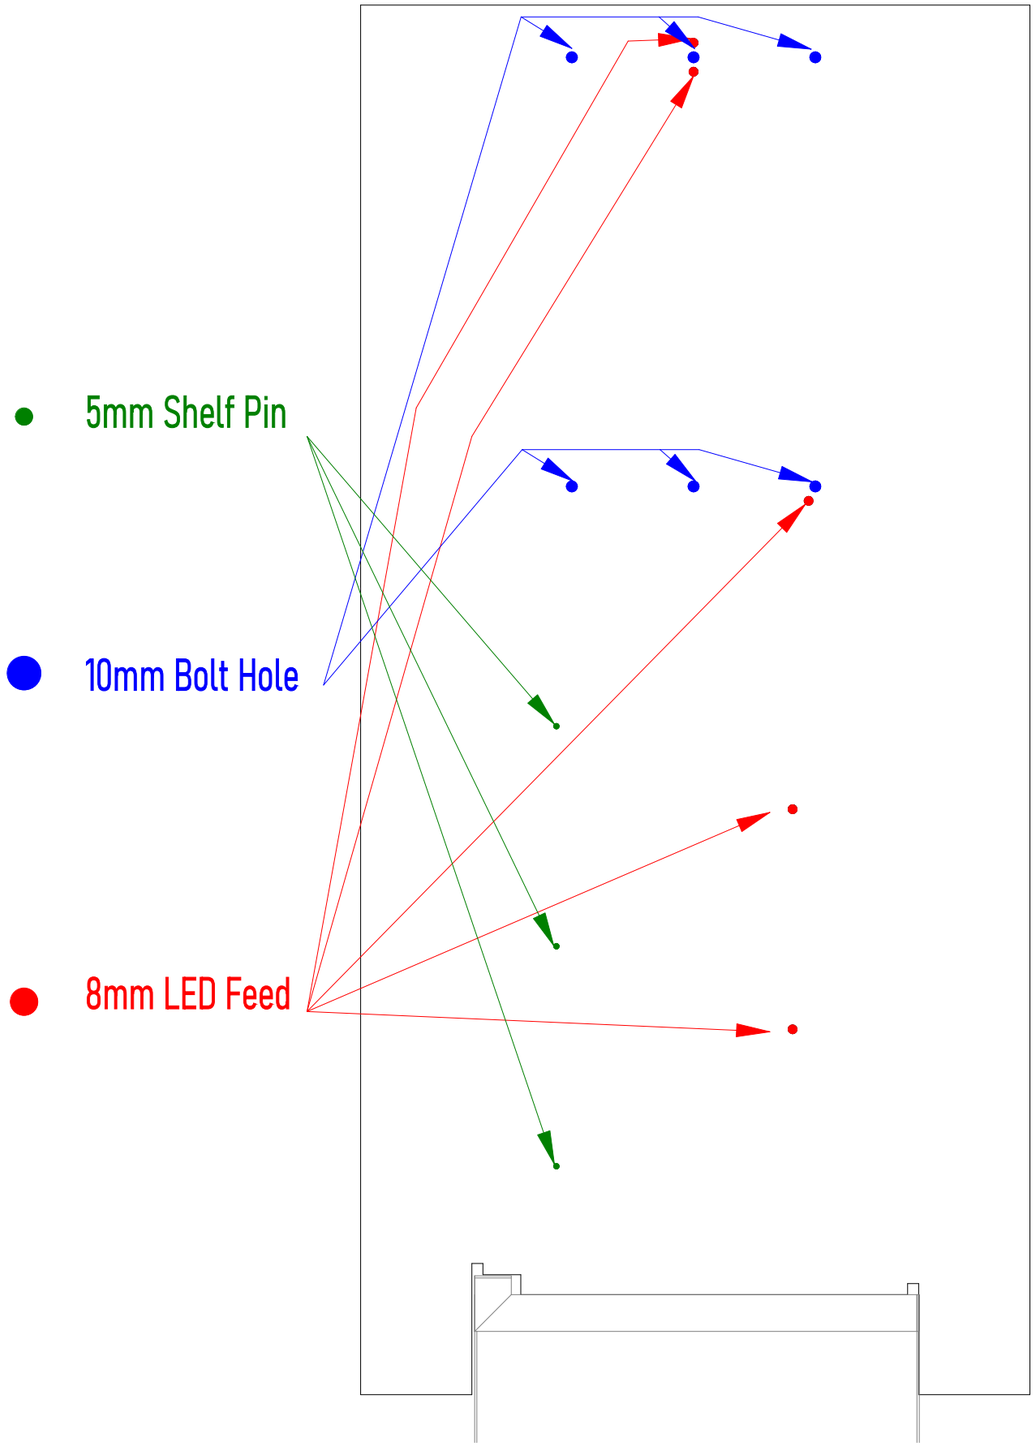

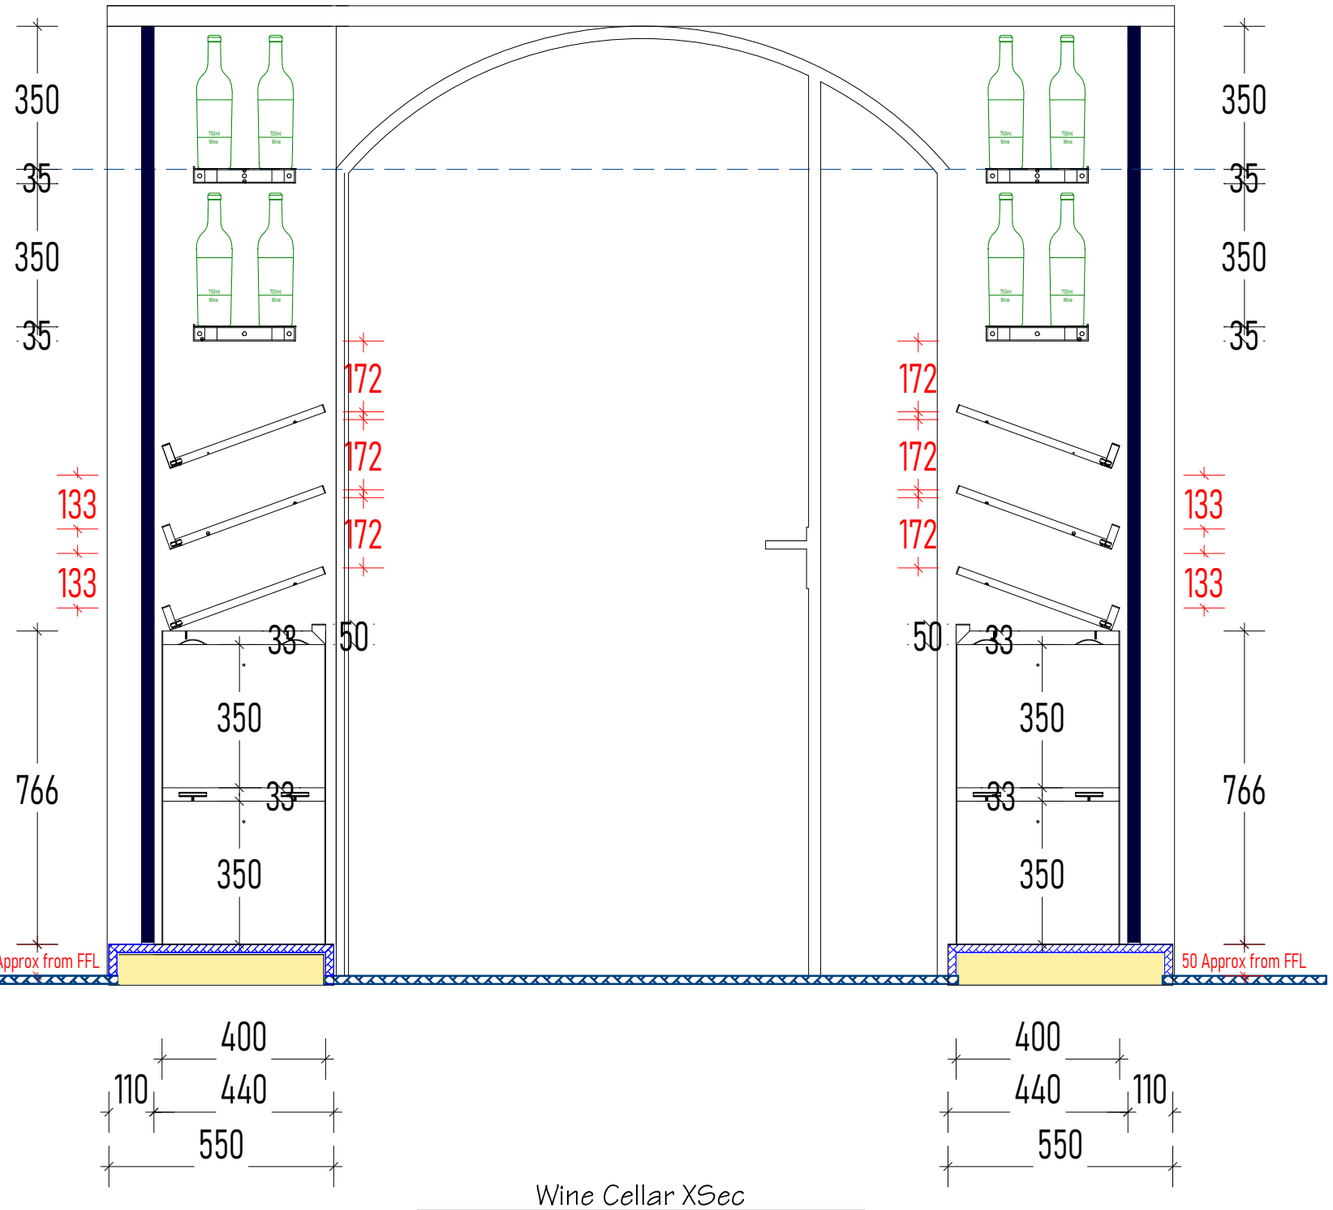

Wine Cellar XSec

Scale: 1 : 15

CN FITOUTS PTY LTD
CUSTOM MADE JOINERY

P 03 9761 6994
E info@cnfitouts.com.au
www.cnfitouts.com.au

6 Stephenson rd.
Bayswater North 3153

CODE	DESCRIPTION
PF-1	18MM 2PAC Painted 'Colour match to Resene Taupe Grey 1/2 strength 30% Satin'
PF-3	18mm 2PAC Painted 'Dulux Haast 1/2 Strength 30% Satin'
PF-5	18mm 2PAC Painted 'Matt Black 30% Satin'
MR-1	16MM POLYTEC 1mm BLACK ANNODISED PROFILE W SMOKEY GREY MIRROR DOOR - BLACK BACKING
ST-2	20MM STONE - ESMERELDA HONED (BLOCK 402 - BATCH F4650)
ST-4	20mm Black Zimbabwe rough cut finish granite
HD1	20mm New York Marble - Backlit LED
DRW	200mm SATIN CHROME LIP PULL
ADJ	BLUM LEGRABOX
FXD	ADJUSTABLE SHELF
	FIXED SHELF

ALL JOINERY

ALL CARCASSES TO BE MADE FROM 16mm HMR White - 1mm Edge

ALL ADJ SHELF HOLES 5X 5MM HOLES 32MM SPACINGS

ALL DRAWERS TO BE Blum Legrabox Drawer

ALL HINGES TO BE 110° BLUM SOFTCLOSE

ALL HANDLES No Pulls/Knobs

Name: Manchen Projects	Phone:
Address: 21 Barry St	Sheet # 6 of 29
City: Kew	Date: 16/10/26
J936 - Barry St Basement	DRAWN MH

Fillers set back 20mm - Shadowline

J936 - Barry St Basement



CN FITOUTS PTY LTD
CUSTOM MADE JOINERY

P 03 9761 6994
E info@cnfitouts.com.au
www.cnfitouts.com.au

6 Stephenson rd.
Bayswater North 3153

CODE	DESCRIPTION
PF-1	18MM 2PAC Painted 'Colour match to Resene Taupe Grey 1/2 strength 30% Satin'
PF-3	18mm 2PAC Painted 'Dulux Haast 1/2 Strength 30% Satin'
PF-5	18mm 2PAC Painted 'Matt Black 30% Satin'
MR-1	16MM POLYTEC 1mm BLACK ANNODISED PROFILE W SMOKEY GREY MIRROR DOOR - BLACK BACKING
ST-2	20MM STONE - ESMERELDA HONED (BLOCK 402 - BATCH F4650)
ST-4	20mm Black Zimbabwe rough cut finish granite
HD1	20mm New York Marble - Backlit LED
DRW	200mm SATIN CHROME LIP PULL
ADJ	BLUM LEGRABOX
FXD	ADJUSTABLE SHELF
	FIXED SHELF

ALL JOINERY

ALL CARCASSES TO BE MADE FROM 16mm HMR White - 1mm Edge

ALL ADJ SHELF HOLES 5X 5MM HOLES 32MM SPACINGS

ALL DRAWERS TO BE Blum Legrabox Drawer

ALL HINGES TO BE 110° BLUM SOFTCLOSE

ALL HANDLES No Pulls/Knobs

Name: Manchen Projects | Phone:

Address: 21 Barry St | Sheet # 7 of 29

City: Kew | Date: 16/10/26

J936 - Barry St Basement | DRAWN MH

Fillers set back 20mm - Shadowline

J936 - Barry St Basement





CN FITOUTS PTY LTD
CUSTOM MADE JOINERY

P 03 9761 6994
E info@cnfitouts.com.au
www.cnfitouts.com.au

6 Stephenson rd.
Bayswater North 3153

CODE	DESCRIPTION
PF-1	18MM 2PAC Painted 'Colour match to Resene Taupe Grey 1/2 strength 30% Satin'
PF-3	18mm 2PAC Painted 'Dulux Haast 1/2 Strength 30% Satin'
PF-5	18mm 2PAC Painted 'Matt Black 30% Satin'
MR-1	16MM POLYTEC 1mm BLACK ANNODISED PROFILE W SMOKEY GREY MIRROR DOOR - BLACK BACKING
ST-2	20MM STONE - ESMERELDA HONED (BLOCK 402 - BATCH F4650)
ST-4	20mm Black Zimbabwe rough cut finish granite
HD1	20mm New York Marble - Backlit LED
DRW	200mm SATIN CHROME LIP PULL
ADJ	BLUM LEGRABOX
FXD	ADJUSTABLE SHELF
	FIXED SHELF

ALL JOINERY

ALL CARCASSES TO BE MADE FROM 16mm HMR White - 1mm Edge

ALL ADJ SHELF HOLES 5X 5MM HOLES 32MM SPACINGS

ALL DRAWERS TO BE Blum Legrabox Drawer

ALL HINGES TO BE 110° BLUM SOFTCLOSE

ALL HANDLES No Pulls/Knobs

Name: Manchen Projects | Phone:


Address: 21 Barry St | Sheet # 8 of 29

City: Kew | Date: 16/10/26

J936 - Barry St Basement | DRAWN MH

Fillers set back 20mm - Shadowline

J936 - Barry St Basement

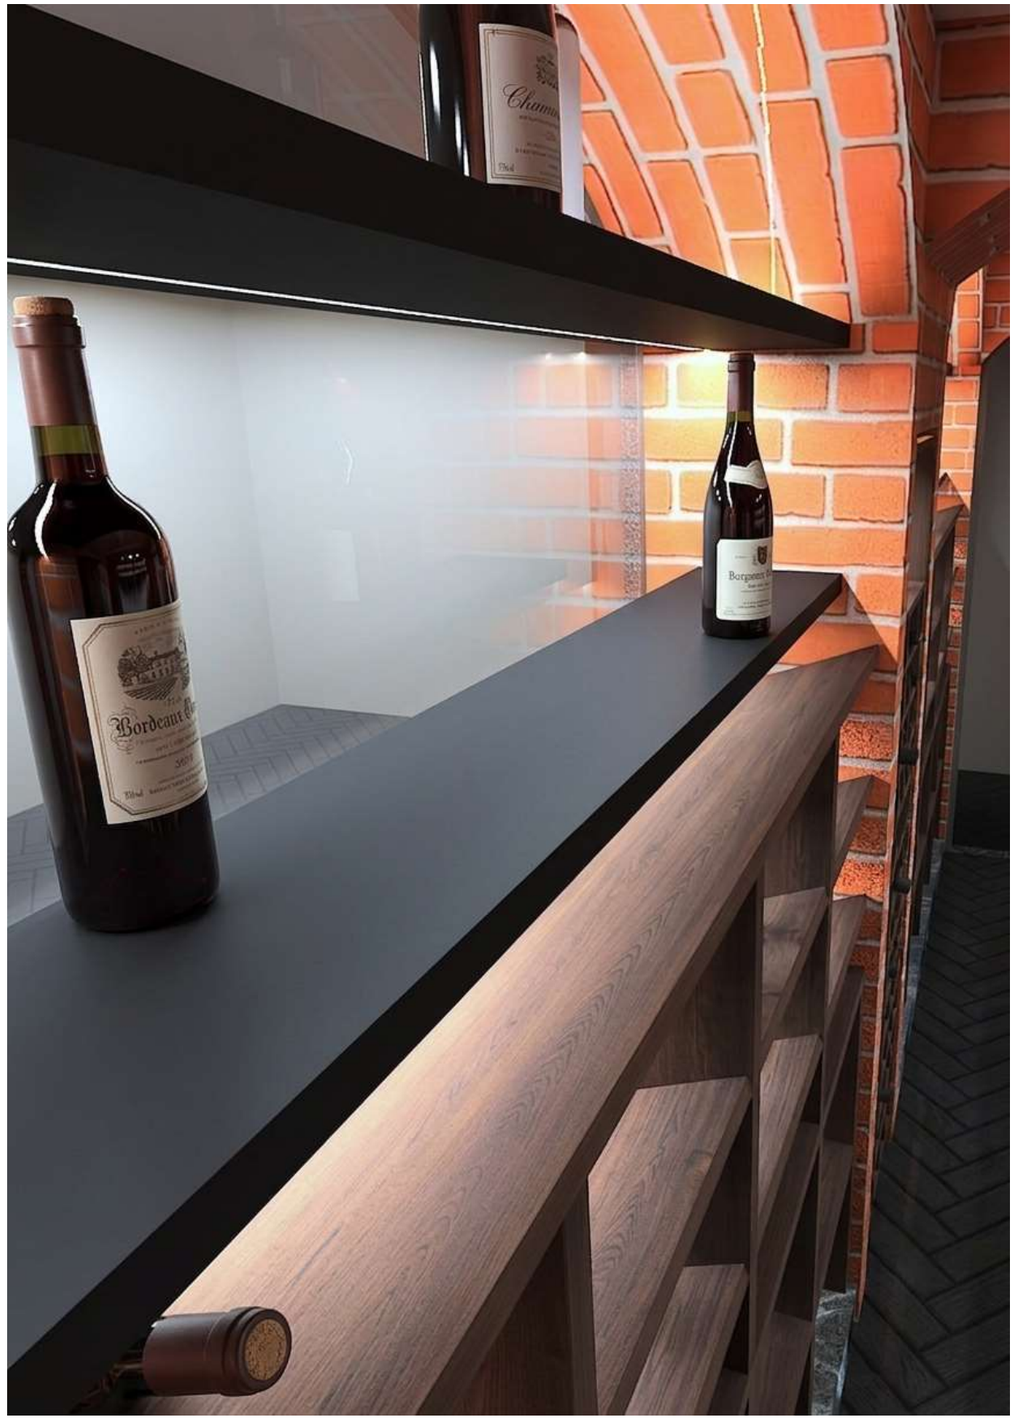



CN FITOUTS PTY LTD
CUSTOM MADE JOINERY

P 03 9761 6994
E info@cnfitouts.com.au
www.cnfitouts.com.au

6 Stephenson rd.
Bayswater North 3153

CODE	DESCRIPTION
PF-1	18MM 2PAC Painted 'Colour match to Resene Taupe Grey 1/2 strength 30% Satin'
PF-3	18mm 2PAC Painted 'Dulux Haast 1/2 Strength 30% Satin'
PF-5	18mm 2PAC Painted 'Matt Black 30% Satin'
MR-1	16MM POLYTEC 1mm BLACK ANNODISED PROFILE W SMOKEY GREY MIRROR DOOR - BLACK BACKING
ST-2	20MM STONE - ESMERELDA HONED (BLOCK 402 - BATCH F4650)
ST-4	20mm Black Zimbabwe rough cut finish granite
HD1	20mm New York Marble - Backlit LED
DRW	200mm SATIN CHROME LIP PULL
ADJ	BLUM LEGRABOX
FXD	ADJUSTABLE SHELF
	FIXED SHELF

ALL JOINERY

ALL CARCASSES TO BE MADE FROM 16mm HMR White - 1mm Edge

ALL ADJ SHELF HOLES 5X 5MM HOLES 32MM SPACINGS

ALL DRAWERS TO BE Blum Legrabox Drawer

ALL HINGES TO BE 110° BLUM SOFTCLOSE


ALL HANDLES No Pulls/Knobs

Name: Manchen Projects | Phone:

Address: 21 Barry St | Sheet # 9 of 29


City: Kew | Date: 16/10/26

J936 - Barry St Basement | DRAWN MH

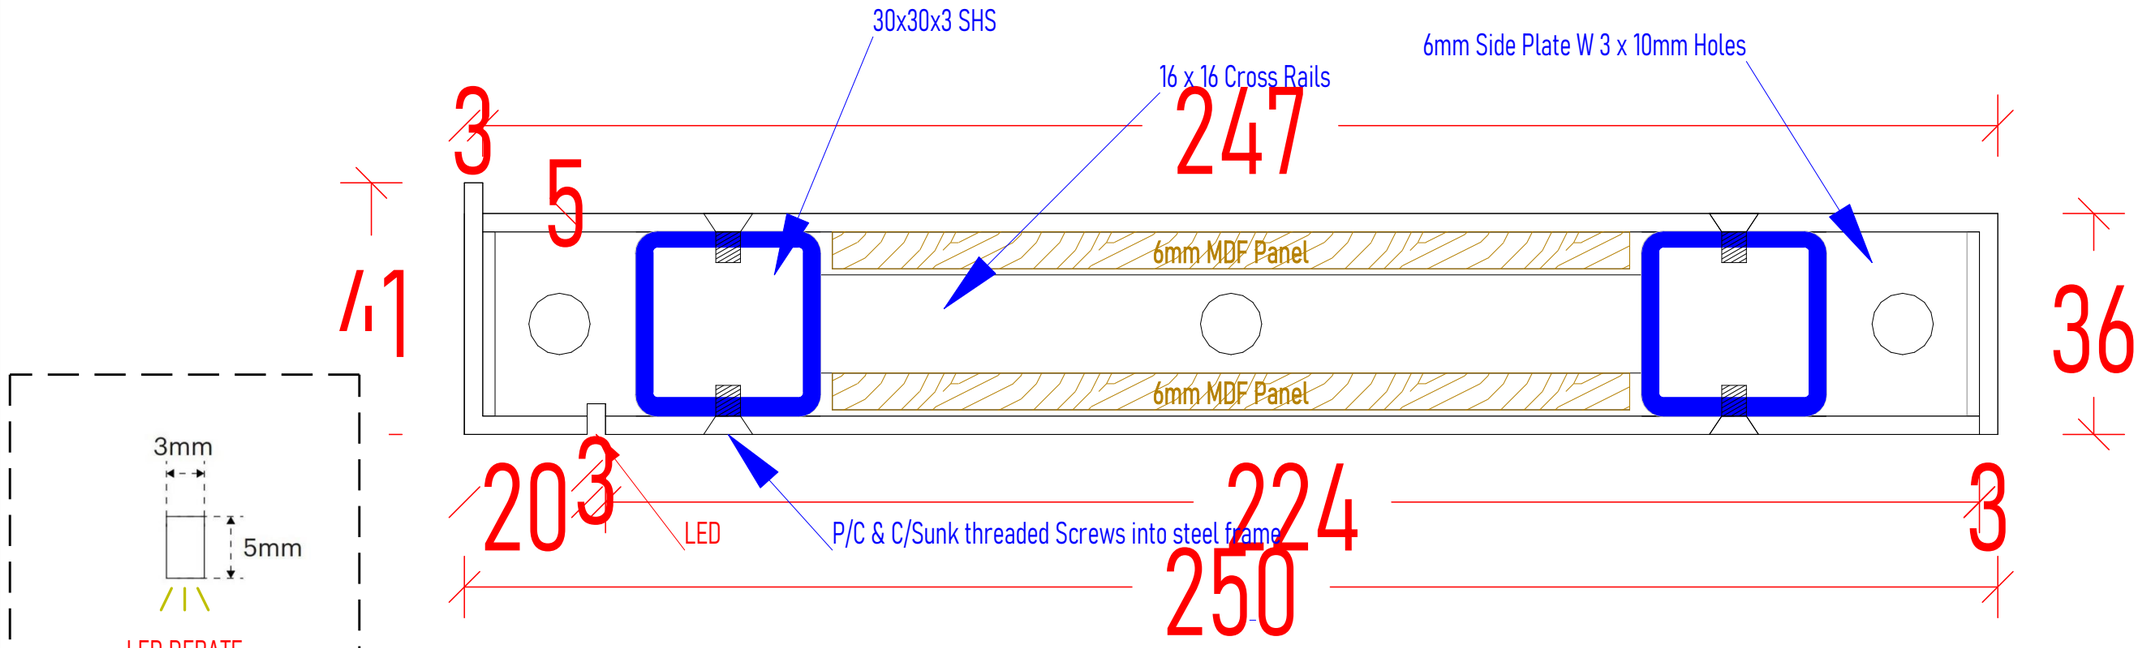

BOTTOM - 36mm Steel Shelf X-Sec

Scale: 1 : 1

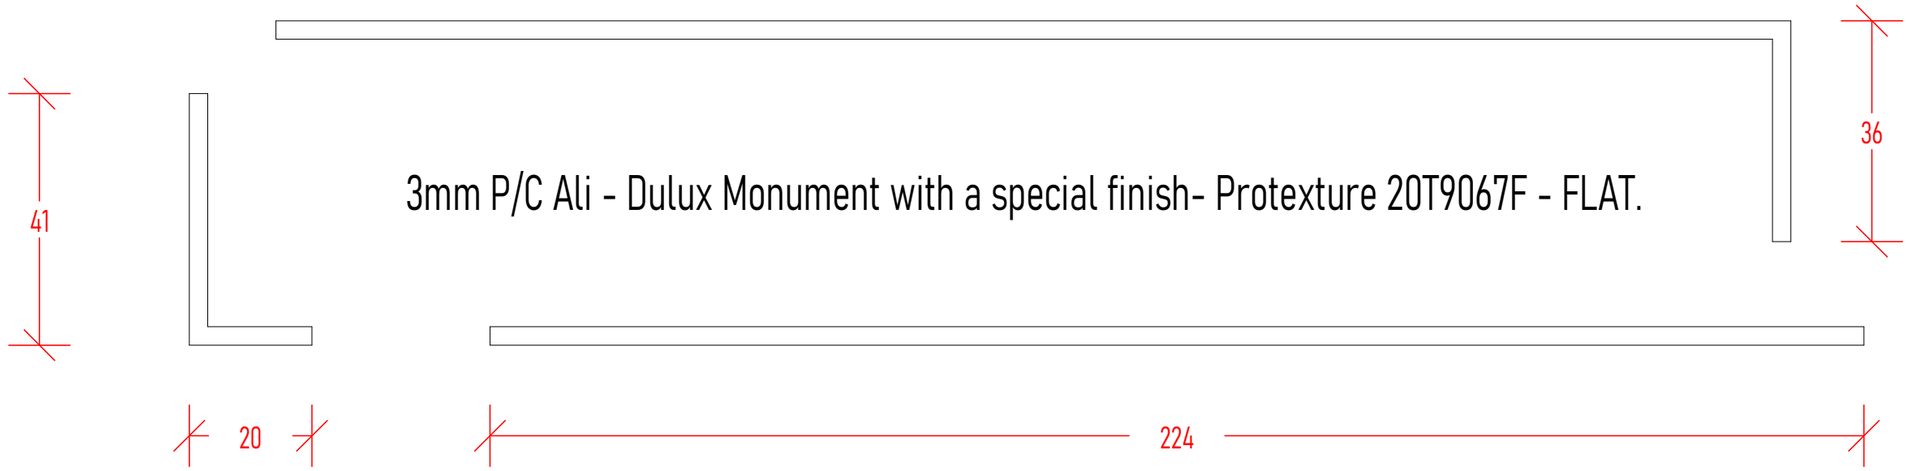

BOTTOM - 36mm Steel Shelf X-Sec

Scale: 1 : 1

CN FITOUTS PTY LTD
CUSTOM MADE JOINERY

P 03 9761 6994
E info@cnfitouts.com.au
www.cnfitouts.com.au

6 Stephenson rd.
Bayswater North 3153

CODE	DESCRIPTION
PF-1	18MM 2PAC Painted 'Colour match to Resene Taupe Grey 1/2 strength 30% Satin'
PF-3	18mm 2PAC Painted 'Dulux Haast 1/2 Strength 30% Satin'
PF-5	18mm 2PAC Painted 'Matt Black 30% Satin'
MR-1	16MM POLYTEC 1mm BLACK ANNODISED PROFILE W SMOKEY GREY MIRROR DOOR - BLACK BACKING
ST-2	20MM STONE - ESMERELDA HONED (BLOCK 402 - BATCH F4650)
ST-4	20mm Black Zimbabwe rough cut finish granite
HD1	20mm New York Marble - Backlit LED
DRW	200mm SATIN CHROME LIP PULL
ADJ	BLUM LEGRABOX
FXD	ADJUSTABLE SHELF
	FIXED SHELF

ALL JOINERY

ALL CARCASSES TO BE MADE FROM 16mm HMR White - 1mm Edge


ALL ADJ SHELF HOLES 5X 5MM HOLES 32MM SPACINGS


ALL DRAWERS TO BE Blum Legrabox Drawer

ALL HINGES TO BE 110° BLUM SOFTCLOSE


ALL HANDLES No Pulls/Knobs

Name: Manchen Projects	Phone:
Address: 21 Barry St	Sheet #12 of 29
City: Kew	Date: 16/10/26
J936 - Barry St Basement	DRAWN MH

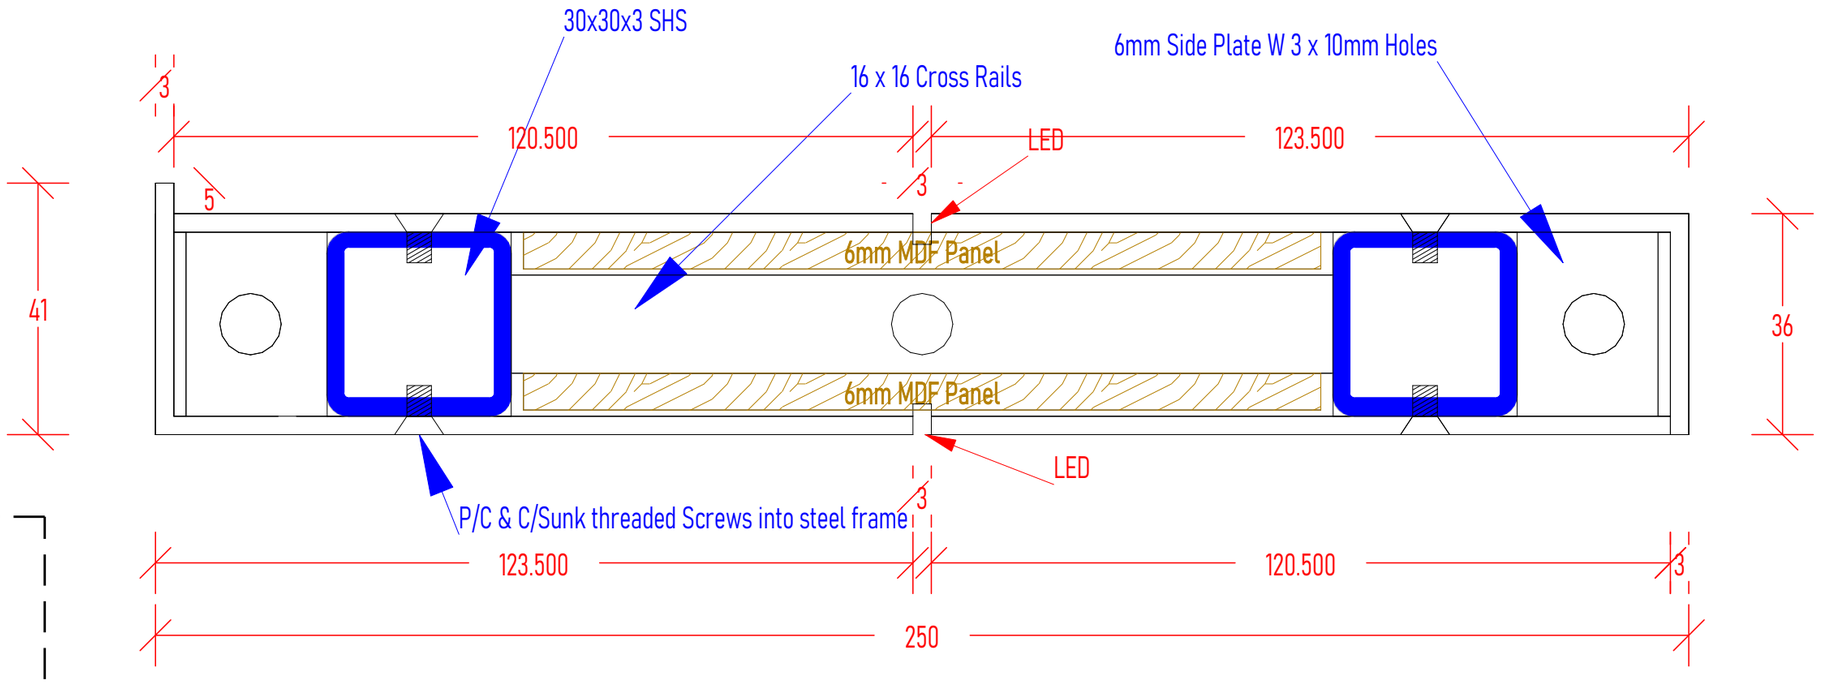

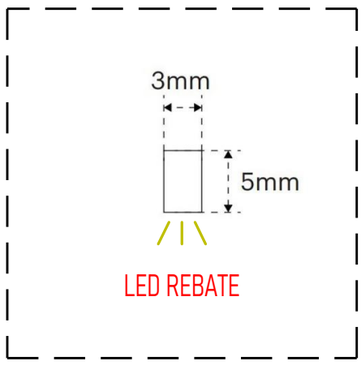

Top - 36mm Steel Shelf X-Sec

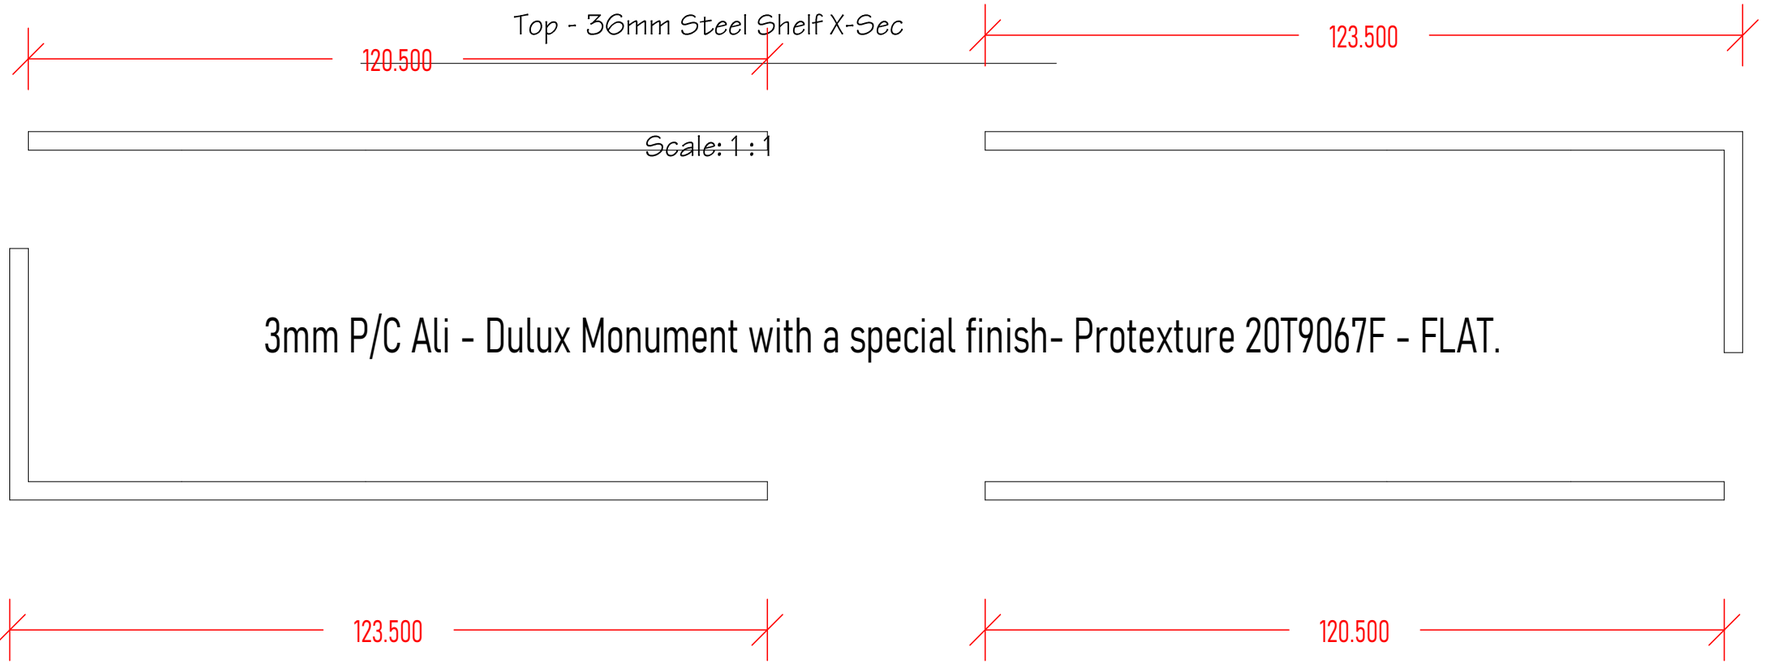

3mm P/C Ali - Dulux Monument with a special finish- Protexture 20T9067F - FLAT.

CN FITOUTS PTY LTD
CUSTOM MADE JOINERY

P 03 9761 6994
E info@cnfitouts.com.au
www.cnfitouts.com.au

6 Stephenson rd.
Bayswater North 3153

CODE	DESCRIPTION
PF-1	18MM 2PAC Painted 'Colour match to Resene Taupe Grey 1/2 strength 30% Satin'
PF-3	18mm 2PAC Painted 'Dulux Haast 1/2 Strength 30% Satin'
PF-5	18mm 2PAC Painted 'Matt Black 30% Satin'
MR-1	16MM POLYTEC 1mm BLACK ANNODISED PROFILE W SMOKEY GREY MIRROR DOOR - BLACK BACKING
ST-2	20MM STONE - ESMERELDA HONED (BLOCK 402 - BATCH F4650)
ST-4	20mm Black Zimbabwe rough cut finish granite
HD1	20mm New York Marble - Backlit LED
DRW	200mm SATIN CHROME LIP PULL
ADJ	BLUM LEGRABOX
FXD	ADJUSTABLE SHELF
	FIXED SHELF

ALL JOINERY

ALL CARCASSES TO BE MADE FROM 16mm HMR White - 1mm Edge


ALL ADJ SHELF HOLES 5X 5MM HOLES 32MM SPACINGS

ALL DRAWERS TO BE Blum Legrabox Drawer

ALL HINGES TO BE 110° BLUM SOFTCLOSE

ALL HANDLES No Pulls/Knobs

Name: Manchen Projects	Phone:
Address: 21 Barry St	Sheet #13 of 29
City: Kew	Date: 16/10/26
J936 - Barry St Basement	DRAWN MH

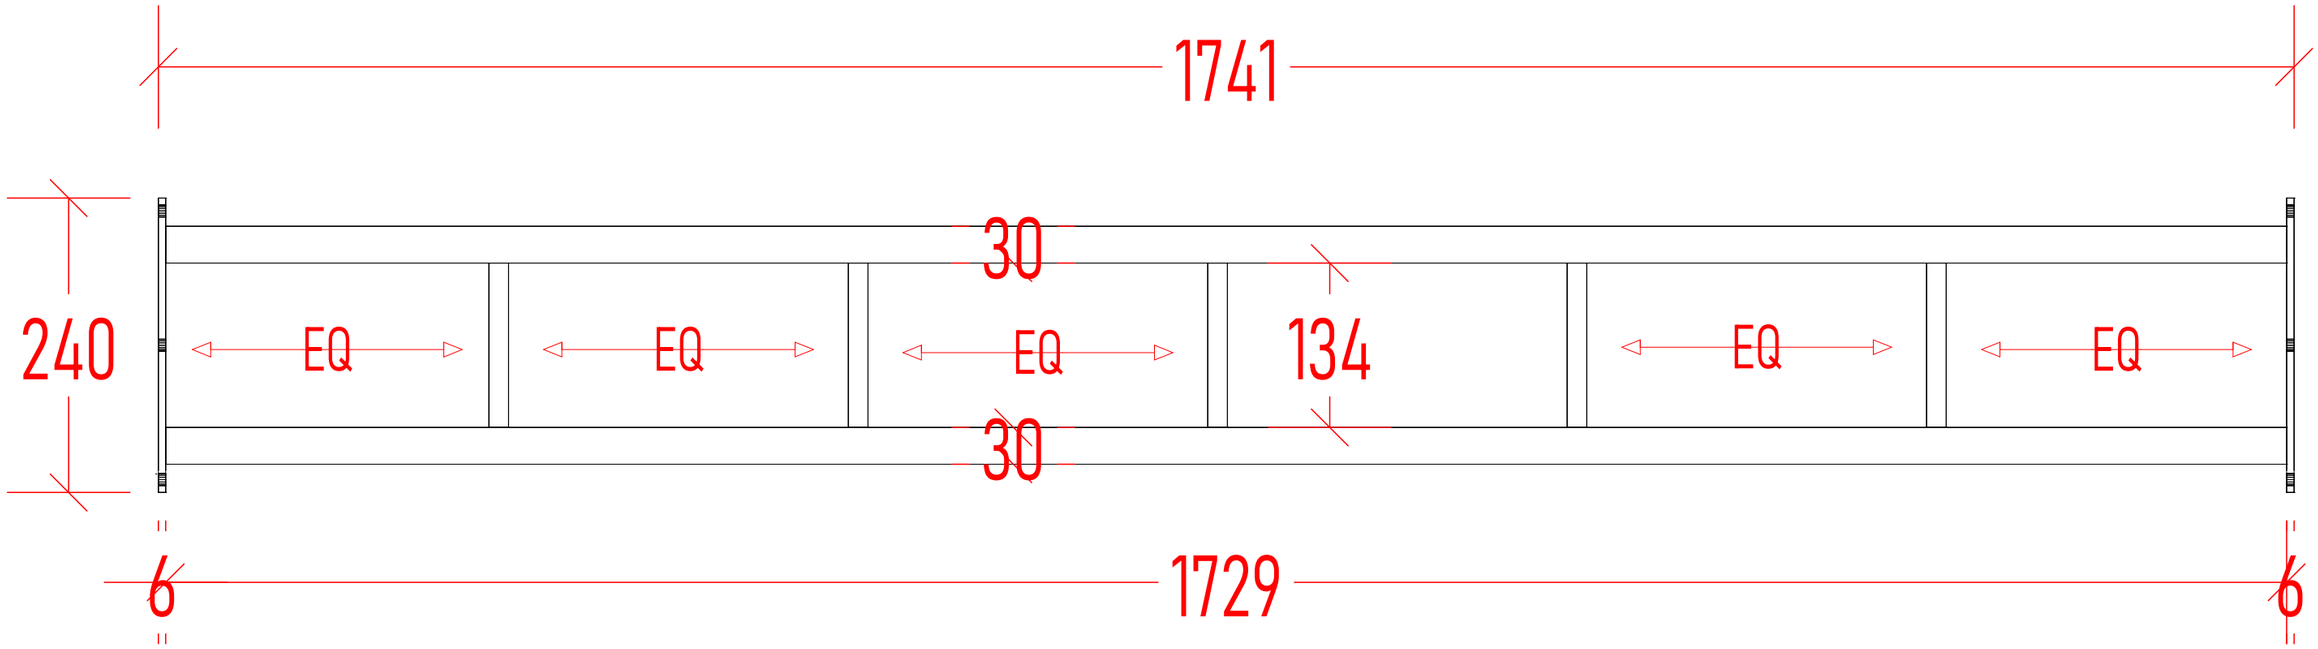



CN FITOUTS PTY LTD
CUSTOM MADE JOINERY

P 03 9761 6994
E info@cnfitouts.com.au
www.cnfitouts.com.au

6 Stephenson rd.
Bayswater North 3153

CODE	DESCRIPTION
PF-1	18MM 2PAC Painted 'Colour match to Resene Taupe Grey 1/2 strength 30% Satin'
PF-3	18mm 2PAC Painted 'Dulux Haast 1/2 Strength 30% Satin'
PF-5	18mm 2PAC Painted 'Matt Black 30% Satin'
MR-1	16MM POLYTEC 1mm BLACK ANNODISED PROFILE W SMOKEY GREY MIRROR DOOR - BLACK BACKING
ST-2	20MM STONE - ESMERELDA HONED (BLOCK 402 - BATCH F4650)
ST-4	20mm Black Zimbabwe rough cut finish granite
HD1	20mm New York Marble - Backlit LED
DRW	200mm SATIN CHROME LIP PULL
ADJ	BLUM LEGRABOX
FXD	ADJUSTABLE SHELF
	FIXED SHELF

ALL JOINERY

ALL CARCASSES TO BE MADE FROM 16mm HMR White - 1mm Edge

ALL ADJ SHELF HOLES 5X 5MM HOLES 32MM SPACINGS

ALL DRAWERS TO BE Blum Legrabox Drawer

ALL HINGES TO BE 110° BLUM SOFTCLOSE

ALL HANDLES No Pulls/Knobs

Name: Manchen Projects | Phone:


Address: 21 Barry St | Sheet #14 of 29


City: Kew | Date: 16/10/26

J936 - Barry St Basement | DRAWN MH

Fillers set back 20mm - Shadowline



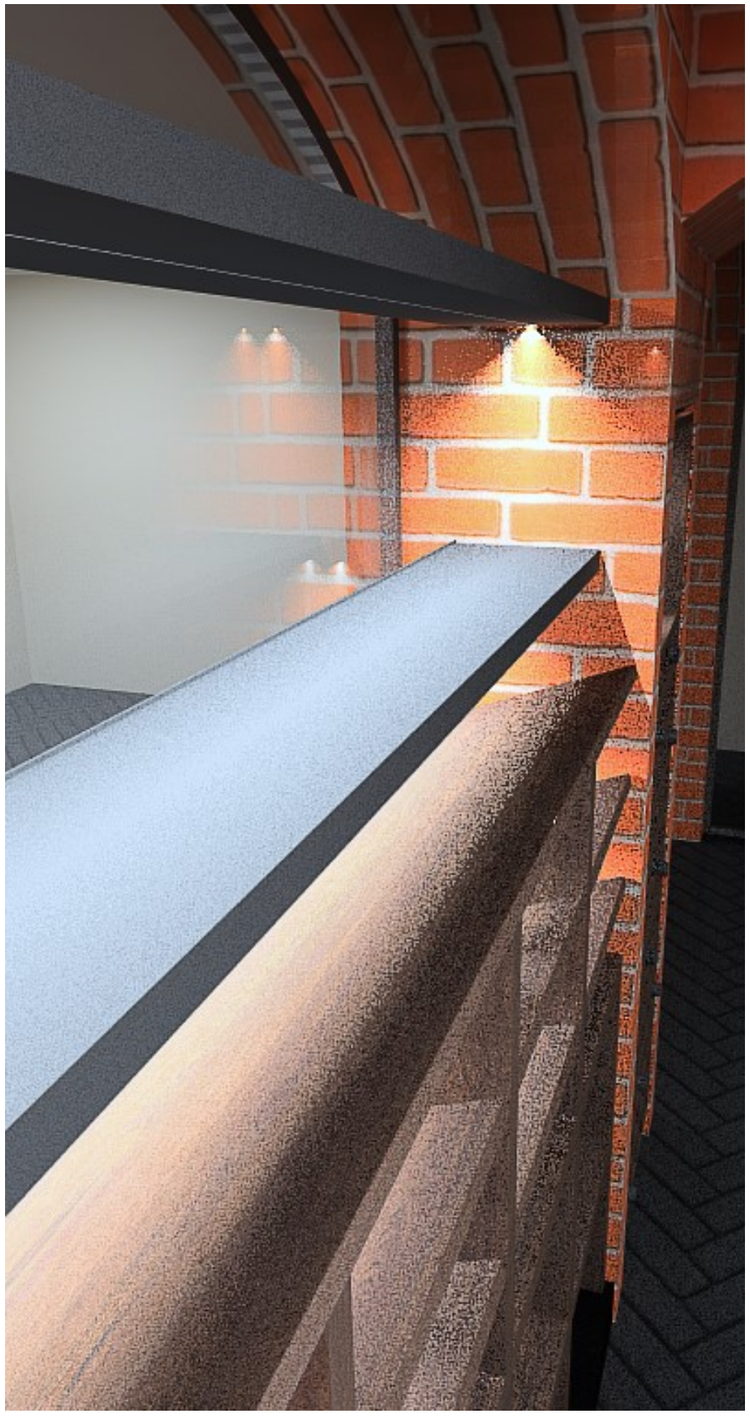

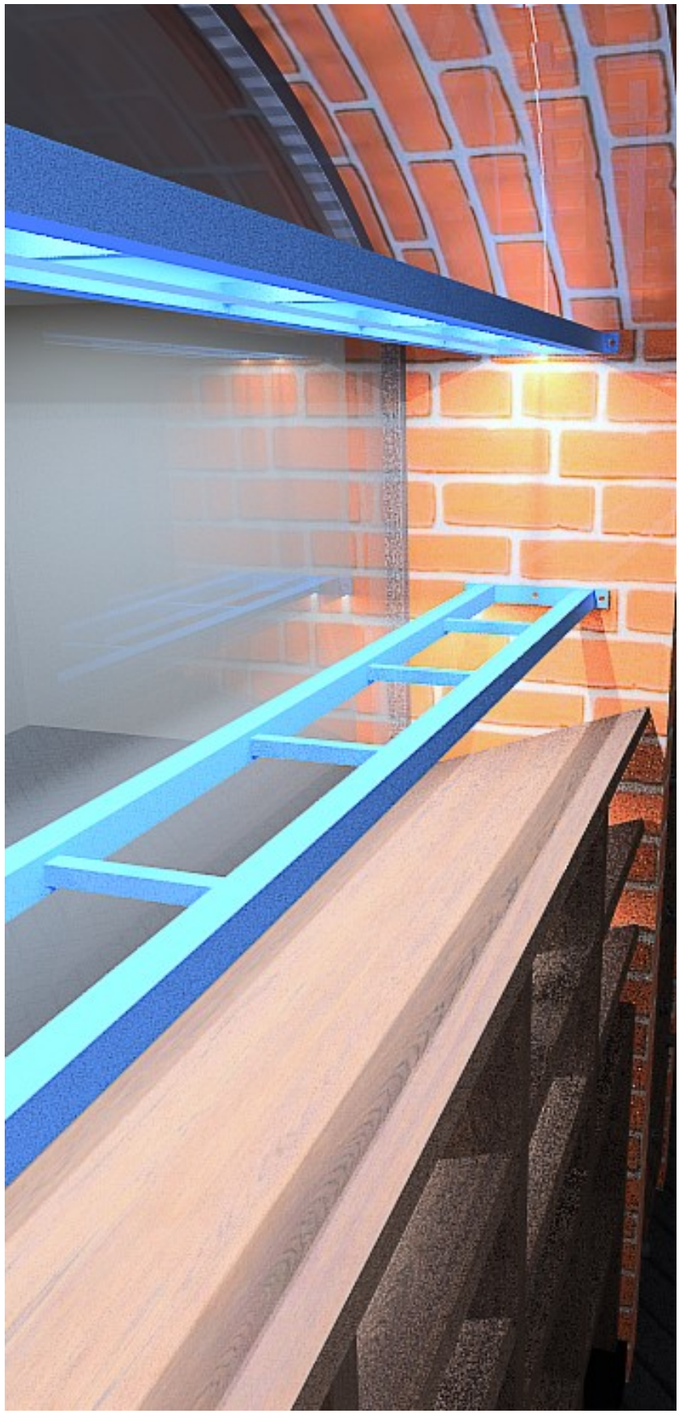

CN FITOUTS PTY LTD
CUSTOM MADE JOINERY

P 03 9761 6994
E info@cnfitouts.com.au
www.cnfitouts.com.au

6 Stephenson rd.
Bayswater North 3153

CODE	DESCRIPTION
PF-1	18MM 2PAC Painted 'Colour match to Resene Taupe Grey 1/2 strength 30% Satin'
PF-3	18mm 2PAC Painted 'Dulux Haast 1/2 Strength 30% Satin'
PF-5	18mm 2PAC Painted 'Matt Black 30% Satin'
MR-1	16MM POLYTEC 1mm BLACK ANNODISED PROFILE W SMOKEY GREY MIRROR DOOR - BLACK BACKING
ST-2	20MM STONE - ESMERELDA HONED (BLOCK 402 - BATCH F4650)
ST-4	20mm Black Zimbabwe rough cut finish granite
HD1	20mm New York Marble - Backlit LED
DRW	200mm SATIN CHROME LIP PULL
ADJ	BLUM LEGRABOX
FXD	ADJUSTABLE SHELF
	FIXED SHELF

ALL JOINERY

ALL CARCASSES TO BE MADE FROM 16mm HMR White - 1mm Edge

ALL ADJ SHELF HOLES 5X 5MM HOLES 32MM SPACINGS

ALL DRAWERS TO BE Blum Legrabox Drawer

ALL HINGES TO BE 110° BLUM SOFTCLOSE

ALL HANDLES No Pulls/Knobs

Name: Manchen Projects | Phone:

Address: 21 Barry St | Sheet #15 of 29

City: Kew | Date: 16/10/26

J936 - Barry St Basement | DRAWN MH