

Fillers set back 50mm to align Kicker Depth

J1121 - 187 Page St - B3+B4 Robes

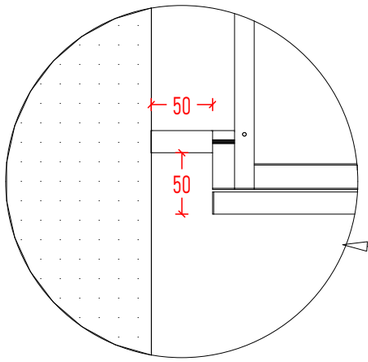


50mm Filler to Wall Detail

Scale: 1 : 5

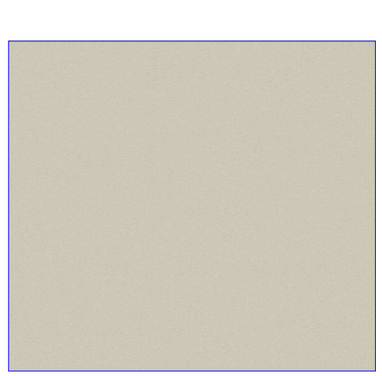

Doors/Panels:
LA2 - 18mm Laminex 'Paper Bark, Absoulute Matte'

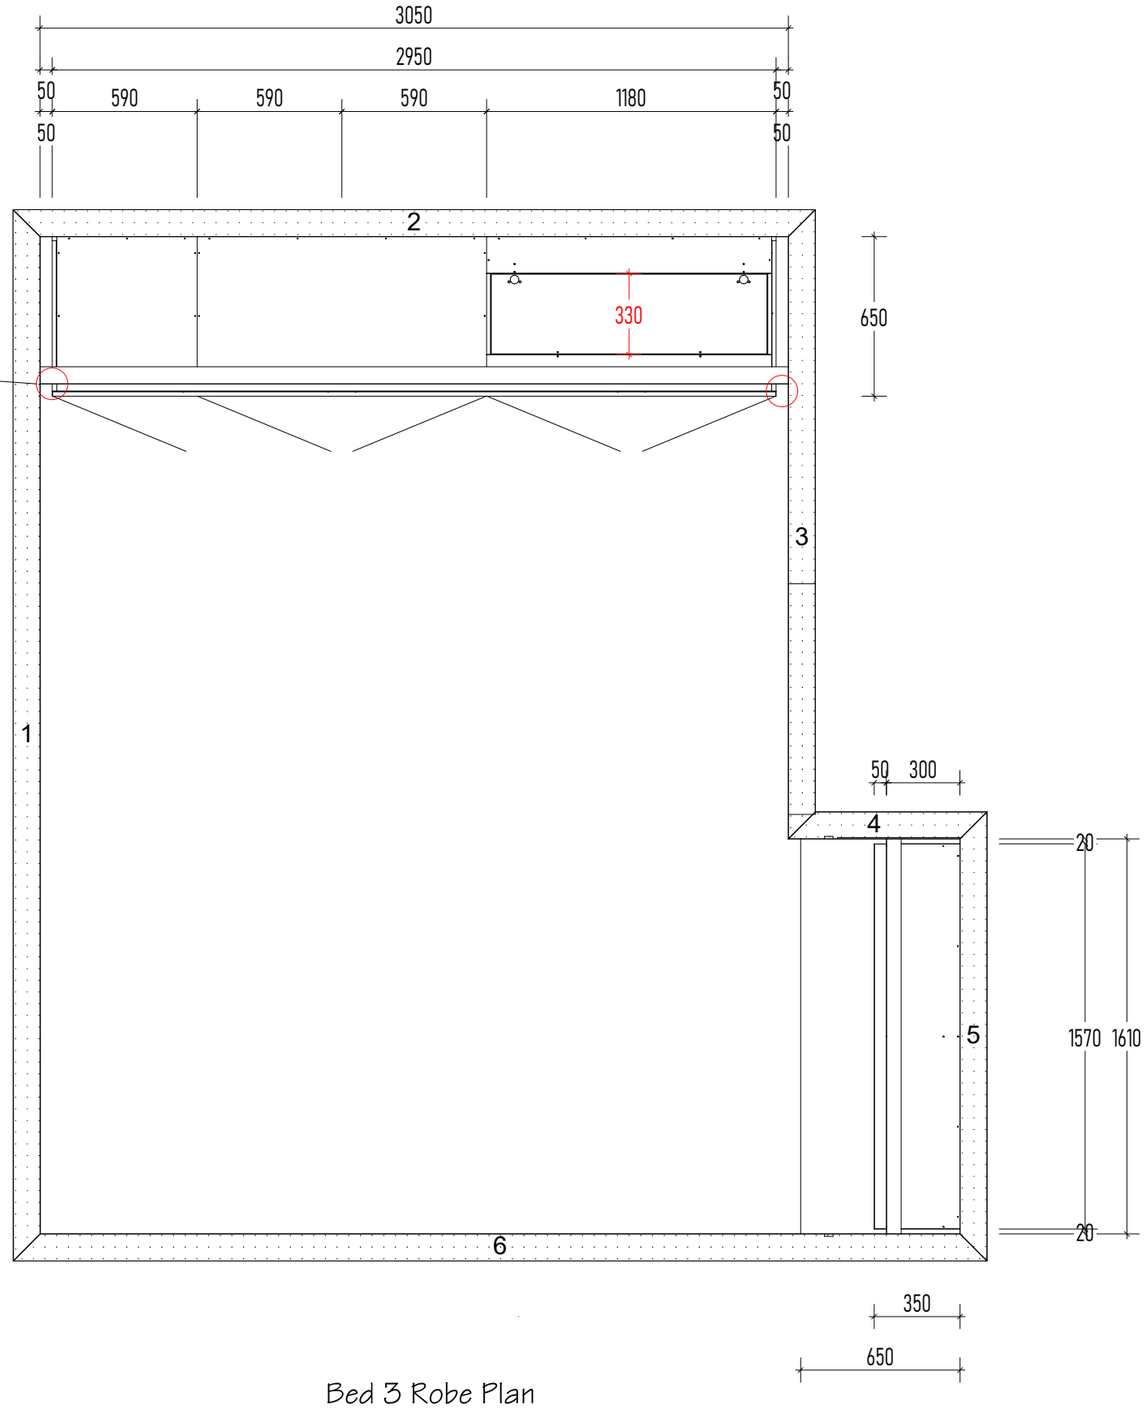

Bed 3 Robe Plan

Scale: 1 : 25

CN FITOUTS PTY LTD
CUSTOM MADE JOINERY

P 03 9761 6994
E info@cnfitouts.com.au
www.cnfitouts.com.au

6 Stephenson rd.
Bayswater North 3153

CODE	DESCRIPTION
LA1/Internals	16mm Polytec Silk Matt
LA2	18mm Laminex Paper Bark Absolute Matt
TV1	19mm Eveneer Prefinished 'Light Oak Wax, Matt'
TV2	19mm Eveneer Prefinished 'Mandel Wax, Matt'
ST1	20mm Sareva 'Natural Stone – Marble, Honed'
ST2	20mm Travertine Litzio " Natural Stone, Filled Honed'
Handle	TBC
GRO-01	

ALL JOINERY

ALL CARCASSES TO BE MADE FROM 16mm Polytec Silk Matt

ALL ADJ SHELF HOLES 5X 5MM HOLES 32MM SPACINGS

ALL DRAWERS TO BE Blum Legrabox Drawer

ALL HINGES TO BE 110° BLUM SOFTCLOSE

ALL HANDLES 224mm C-Pull

Name: Grace Lewin

Phone:

Address: 187 Page St.

City: Middle Park

Sheet # 1 of 8


Date: 05/11/26

J1121 - 187 Page St - B3+B4 Robes

DRAWN MH


Fillers set back 50mm to align Kicker Depth

J1121 - 187 Page St - B3+B4 Robes

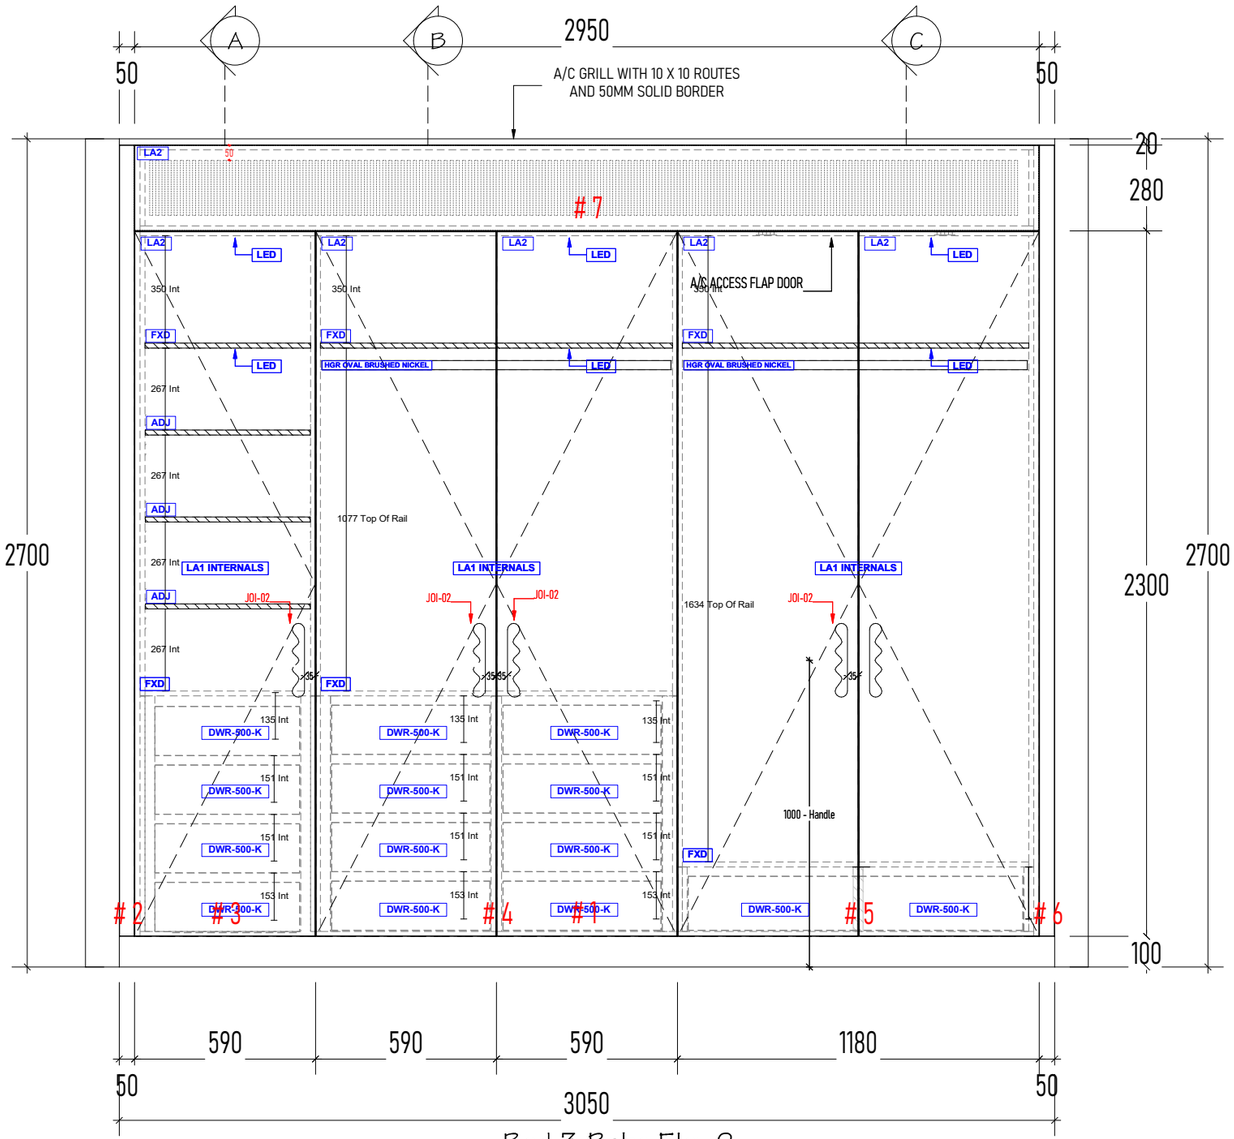


Bed 3 Robe Elev 2

Scale: 1 : 20

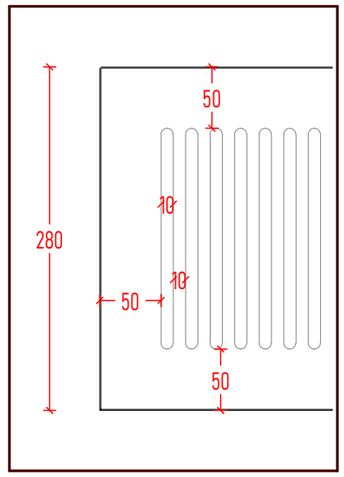

A/C Bulkhead Detail

Scale: 1 : 5

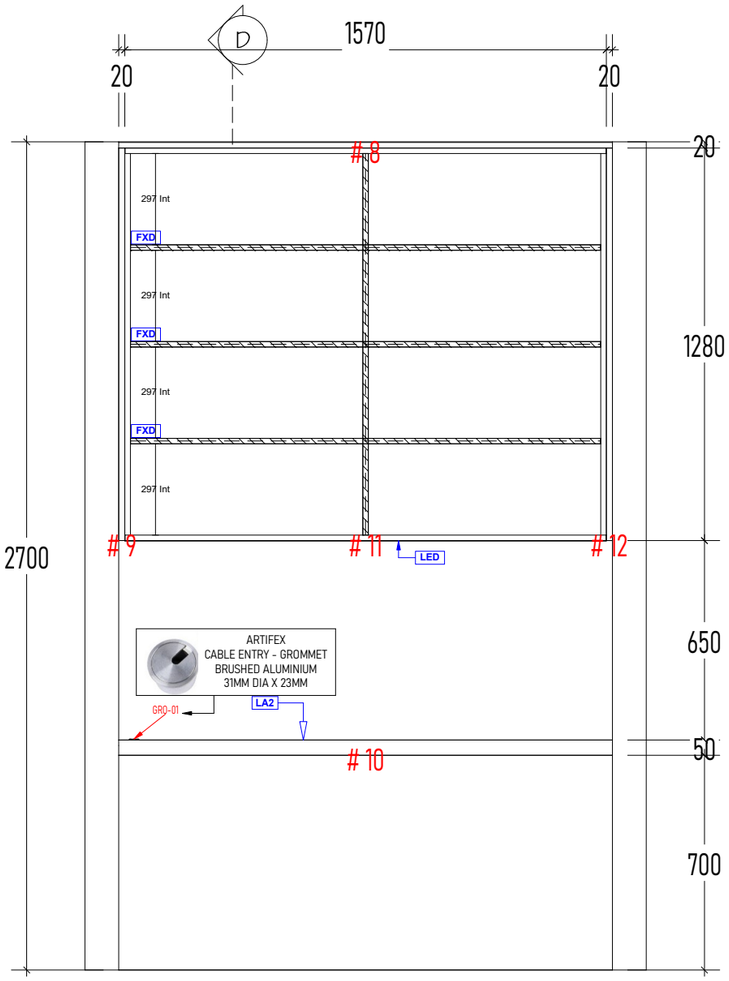

Bed 3 Robe Elev 5

Scale: 1 : 20

CN FITOUTS PTY LTD
CUSTOM MADE JOINERY

P 03 9761 6994
E info@cnfitouts.com.au
www.cnfitouts.com.au

6 Stephenson rd.
Bayswater North 3153

CODE	DESCRIPTION
LA1/Internals	16mm Polytec Silk Matt
LA2	18mm Laminex Paper Bark Absolute Matt
TV1	19mm Eveneer Prefinished 'Light Oak Wax, Matt'
TV2	19mm Eveneer Prefinished 'Mandel Wax, Matt'
ST1	20mm Sareva 'Natural Stone – Marble, Honed'
ST2	20mm Travertine Litzio ' Natural Stone, Filled Honed'
Handle	TBC
GRO-01	

ALL JOINERY

ALL CARCASSES TO BE MADE FROM 16mm Polytec Silk Matt

ALL ADJ SHELF HOLES 5X 5MM HOLES 32MM SPACINGS

ALL DRAWERS TO BE Blum Legrabox Drawer


ALL HINGES TO BE 110° BLUM SOFTCLOSE

ALL HANDLES 224mm C-Pull

Name: Grace Lewin	Phone:
Address: 187 Page St.	Sheet # 2 of 8
City: Middle Park	Date: 05/11/26
J1121 - 187 Page St - B3+B4 Robes	DRAWN MH


Fillers set back 50mm to align Kicker Depth

J1121 - 187 Page St - B3+B4 Robes

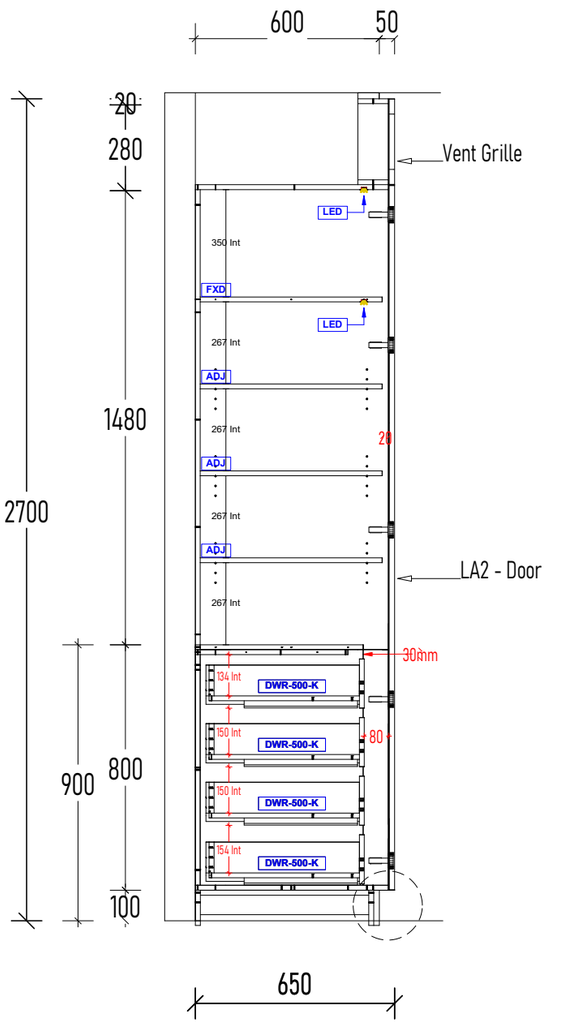


Bed 3 Robe - A X-Sec

Scale: 1 : 20

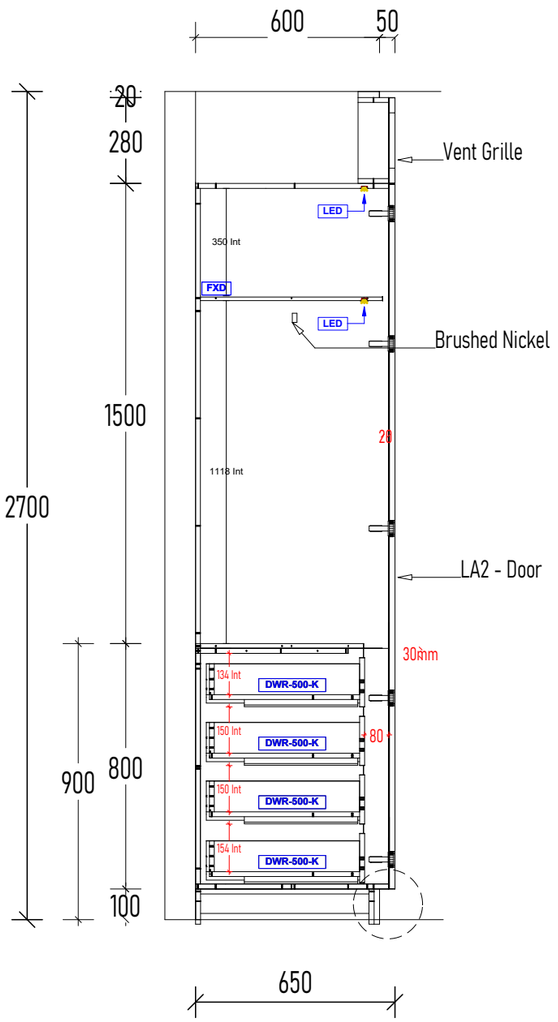


Bed 3 Robe - B X-Sec

Scale: 1 : 20

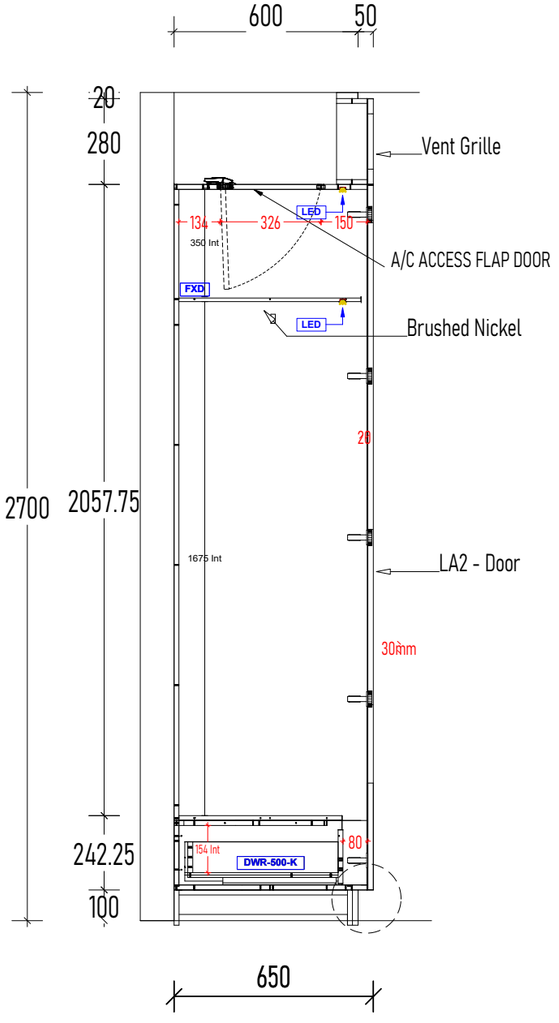


Bed 3 Robe - C X-Sec

Scale: 1 : 20

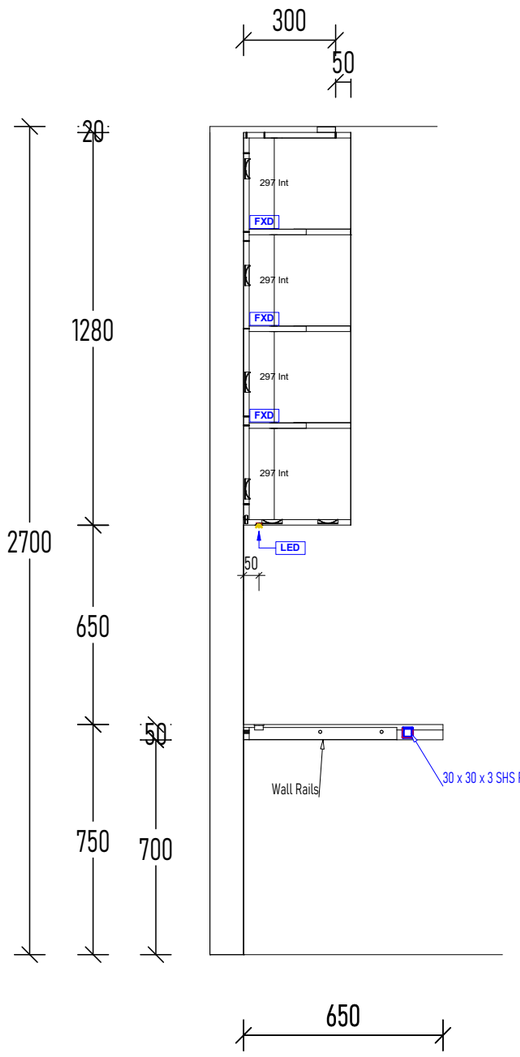

Bed 3 Robe - D X-Sec

Scale: 1 : 20

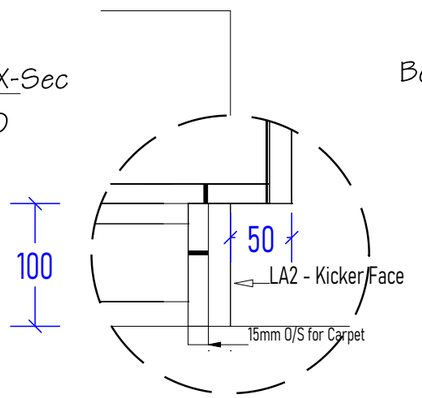

CN FITOUTS PTY LTD
CUSTOM MADE JOINERY

P 03 9761 6994
E info@cnfitouts.com.au
www.cnfitouts.com.au

6 Stephenson rd.
Bayswater North 3153

CODE	DESCRIPTION
LA1/Internals	16mm Polytec Silk Matt
LA2	18mm Laminex Paper Bark Absolute Matt
TV1	19mm Eveneer Prefinished 'Light Oak Wax, Matt'
TV2	19mm Eveneer Prefinished 'Mandel Wax, Matt'
ST1	20mm Sareva 'Natural Stone – Marble, Honed'
ST2	20mm Travertine Litzio ' Natural Stone, Filled Honed'
Handle	TBC
GRO-01	

ALL JOINERY

ALL CARCASSES TO BE MADE FROM 16mm Polytec Silk Matt

ALL ADJ SHELF HOLES 5X 5MM HOLES 32MM SPACINGS

ALL DRAWERS TO BE Blum Legrabox Drawer

ALL HINGES TO BE 110° BLUM SOFTCLOSE

ALL HANDLES 224mm C-Pull

Name: Grace Lewin	Phone:
Address: 187 Page St.	Sheet # 3 of 8
City: Middle Park	Date: 05/11/26
J1121 - 187 Page St - B3+B4 Robes	DRAWN MH

Fillers set back 50mm to align Kicker Depth









CN FITOUTS PTY LTD
CUSTOM MADE JOINERY

P 03 9761 6994
E info@cnfitouts.com.au
www.cnfitouts.com.au

6 Stephenson rd.
Bayswater North 3153

CODE	DESCRIPTION
LA1/Internals	16mm Polytec Silk Matt
LA2	18mm Laminex Paper Bark Absolute Matt
TV1	19mm Eveneer Prefinished 'Light Oak Wax, Matt'
TV2	19mm Eveneer Prefinished 'Mandel Wax, Matt'
ST1	20mm Sareva 'Natural Stone – Marble, Honed'
ST2	20mm Travertine Litzio ' Natural Stone, Filled Honed'
Handle	TBC
GRO-01	

ALL JOINERY

ALL CARCASSES TO BE MADE FROM 16mm Polytec Silk Matt

ALL ADJ SHELF HOLES 5X 5MM HOLES 32MM SPACINGS

ALL DRAWERS TO BE Blum Legrabox Drawer

ALL HINGES TO BE 110° BLUM SOFTCLOSE

ALL HANDLES 224mm C-Pull

Name: Grace Lewin | Phone:

Address: 187 Page St.

City: Middle Park


Sheet # 4 of 8

Date: 05/11/26

J1121 - 187 Page St - B3+B4 Robes | DRAWN MH


Fillers set back 50mm to align Kicker Depth

J1121 - 187 Page St - B3+B4 Robes

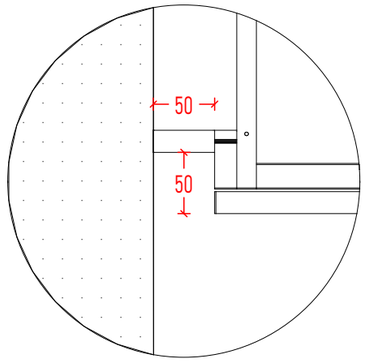


50mm Filler to Wall Detail

Scale: 1 : 5

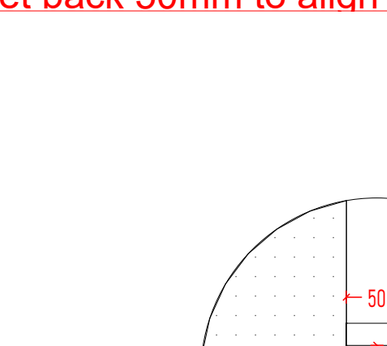

Doors/Panels:
LA2 - 18mm Laminex 'Paper Bark, Absoulute Matte'

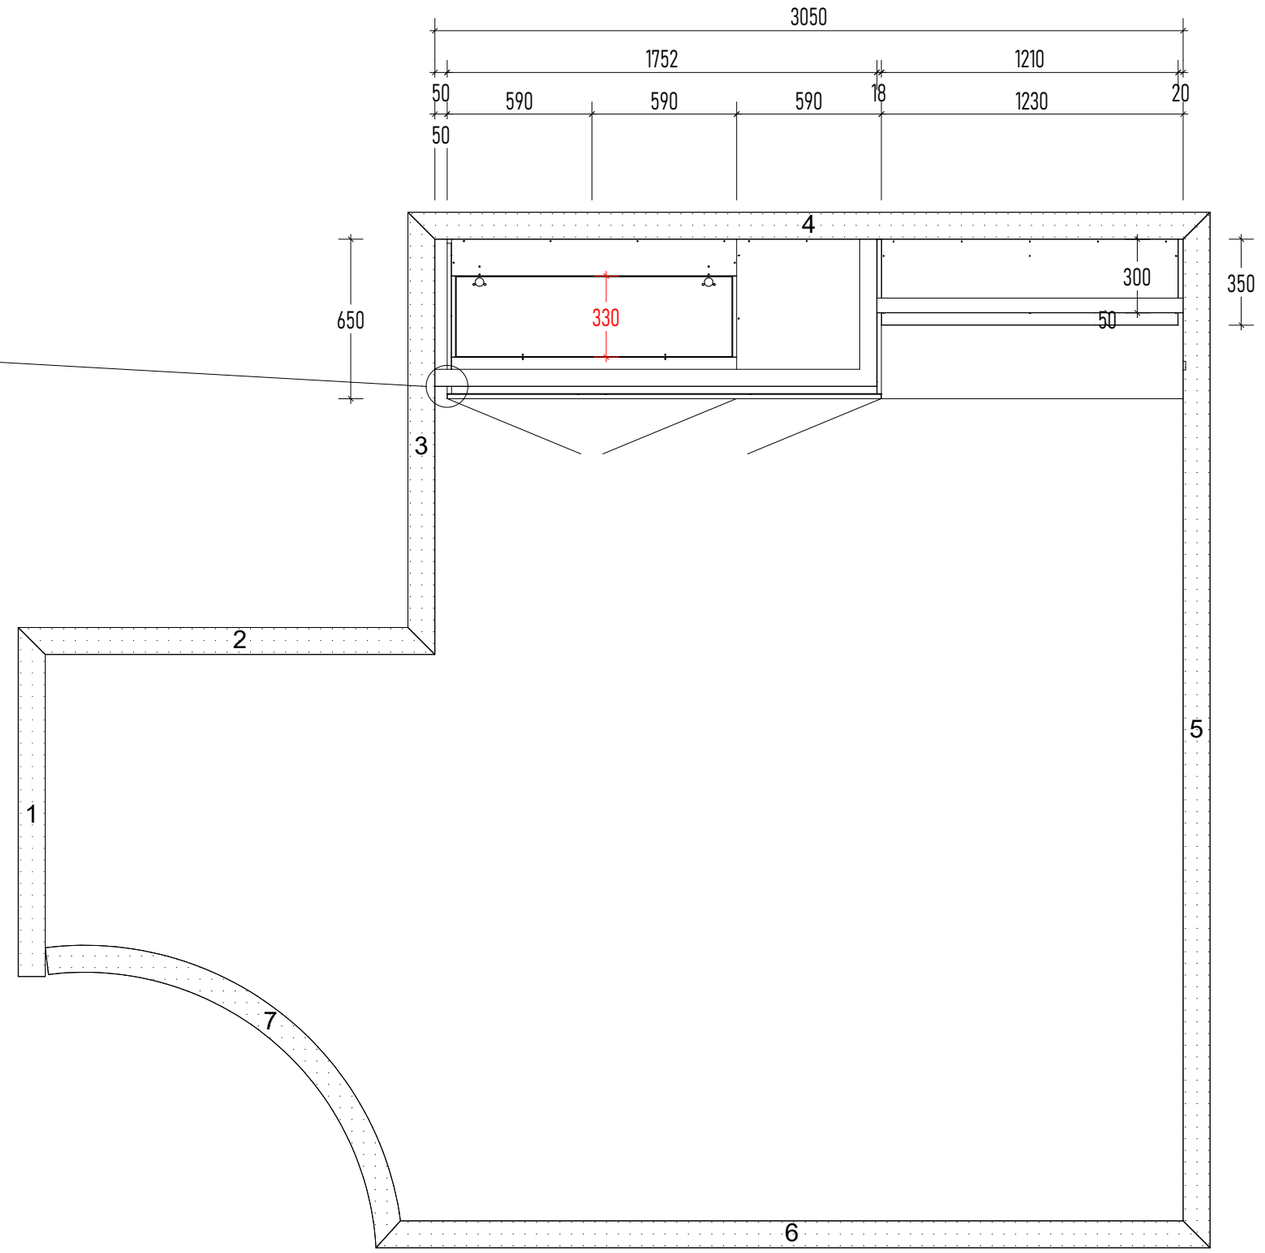

Bed 4 Robe Plan

Scale: 1 : 25

CN FITOUTS PTY LTD
CUSTOM MADE JOINERY

P 03 9761 6994
E info@cnfitouts.com.au
www.cnfitouts.com.au

6 Stephenson rd.
Bayswater North 3153

CODE	DESCRIPTION
LA1/Internals	16mm Polytec Silk Matt
LA2	18mm Laminex Paper Bark Absolute Matt
TV1	19mm Eveneer Prefinished 'Light Oak Wax, Matt'
TV2	19mm Eveneer Prefinished 'Mandel Wax, Matt'
ST1	20mm Sareva 'Natural Stone – Marble, Honed'
ST2	20mm Travertine Litzio ' Natural Stone, Filled Honed'
Handle	TBC
GRO-01	

ALL JOINERY

ALL CARCASSES TO BE MADE FROM 16mm Polytec Silk Matt

ALL ADJ SHELF HOLES 5X 5MM HOLES 32MM SPACINGS

ALL DRAWERS TO BE Blum Legrabox Drawer

ALL HINGES TO BE 110° BLUM SOFTCLOSE

ALL HANDLES 224mm C-Pull

Name: Grace Lewin

Phone:

Address: 187 Page St.

Sheet # 5 of 8

City: Middle Park


Date: 05/11/26

J1121 - 187 Page St - B3+B4 Robes

DRAWN MH


Fillers set back 50mm to align Kicker Depth

J1121 - 187 Page St - B3+B4 Robes

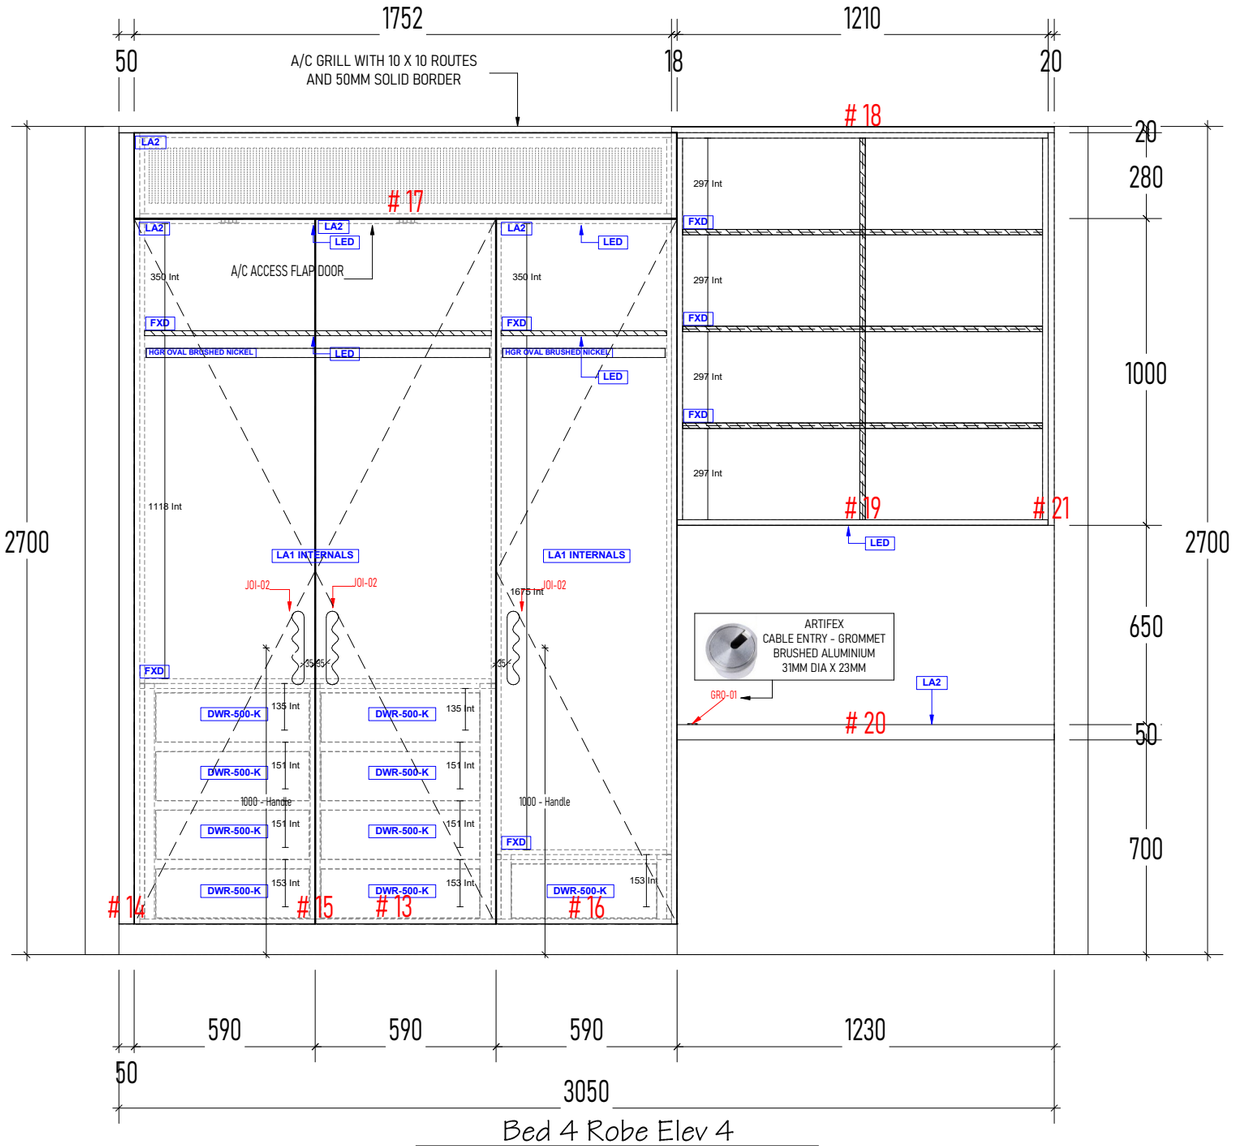

Bed 4 Robe Elev 4

Scale: 1 : 20

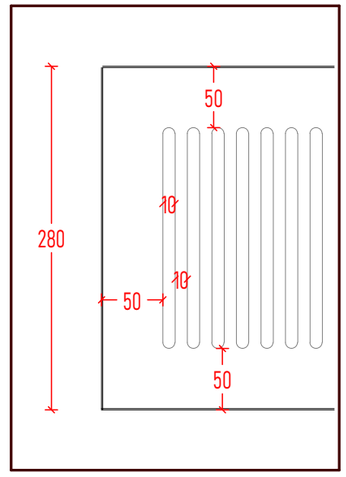

A/C Bulkhead Detail

Scale: 1 : 5

CN FITOUTS PTY LTD
CUSTOM MADE JOINERY

P 03 9761 6994
E info@cnfitouts.com.au
www.cnfitouts.com.au

6 Stephenson rd.
Bayswater North 3153

CODE	DESCRIPTION
LA1/Internals	16mm Polytec Silk Matt
LA2	18mm Laminex Paper Bark Absolute Matt
TV1	19mm Eveneer Prefinished 'Light Oak Wax, Matt'
TV2	19mm Eveneer Prefinished 'Mandel Wax, Matt'
ST1	20mm Sareva 'Natural Stone – Marble, Honed'
ST2	20mm Travertine Litzio ' Natural Stone, Filled Honed'
Handle	TBC
GRO-01	

ALL JOINERY

ALL CARCASSES TO BE MADE FROM 16mm Polytec Silk Matt

ALL ADJ SHELF HOLES 5X 5MM HOLES 32MM SPACINGS

ALL DRAWERS TO BE Blum Legrabox Drawer

ALL HINGES TO BE 110° BLUM SOFTCLOSE

ALL HANDLES 224mm C-Pull

Name: Grace Lewin

Phone:

Address: 187 Page St.

Sheet # 6 of 8


City: Middle Park

Date: 05/11/26

J1121 - 187 Page St - B3+B4 Robes


DRAWN MH


Fillers set back 50mm to align Kicker Depth

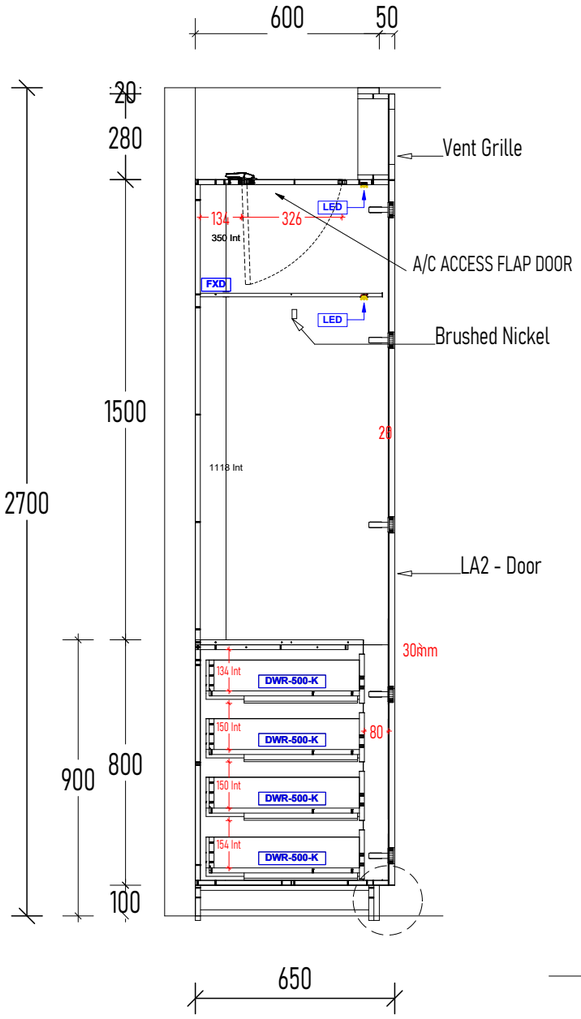

Bed 4 Robe - B X-Sec


Scale: 1 : 20

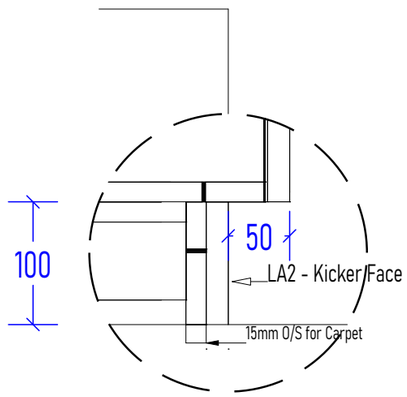

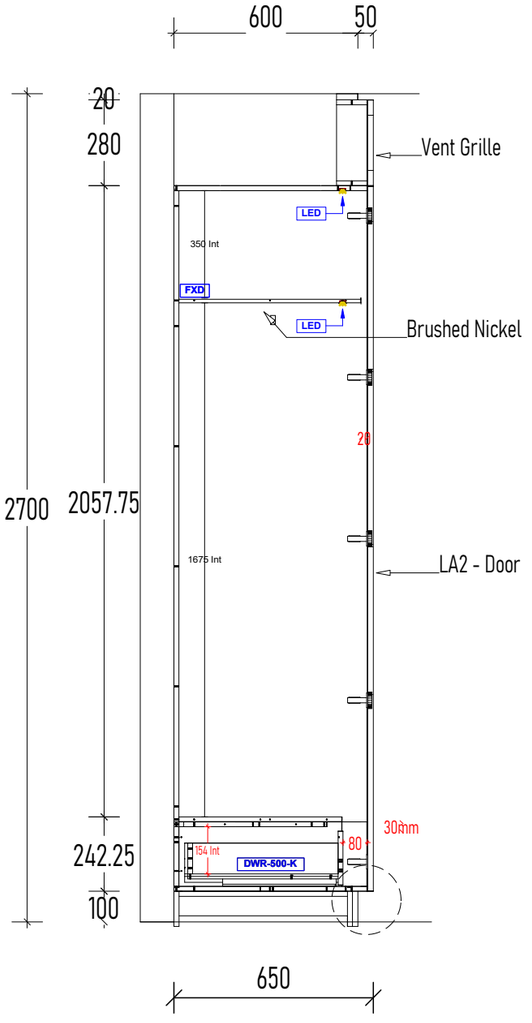

Bed 4 Robe - C X-Sec

Scale: 1 : 20

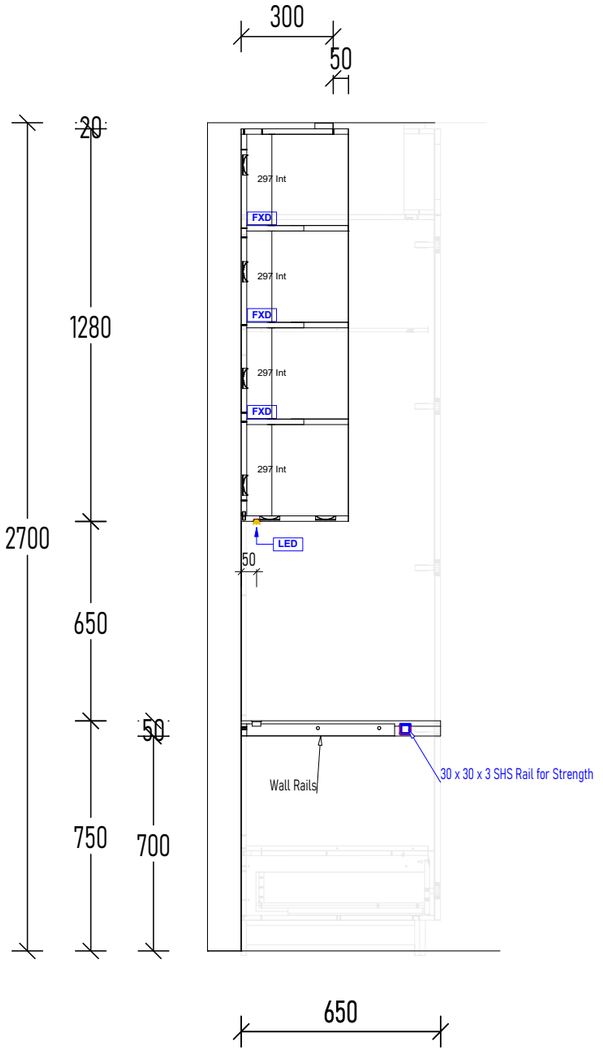

Bed 4 Robe - D X-Sec

Scale: 1 : 20

CN FITOUTS PTY LTD
CUSTOM MADE JOINERY

P 03 9761 6994
E info@cnfitouts.com.au
www.cnfitouts.com.au

6 Stephenson rd.
Bayswater North 3153

CODE	DESCRIPTION
LA1/Internals	16mm Polytec Silk Matt
LA2	18mm Laminex Paper Bark Absolute Matt
TV1	19mm Eveneer Prefinished 'Light Oak Wax, Matt'
TV2	19mm Eveneer Prefinished 'Mandel Wax, Matt'
ST1	20mm Sareva 'Natural Stone – Marble, Honed'
ST2	20mm Travertine Litzio ' Natural Stone, Filled Honed'
Handle	TBC
GRO-01	

ALL JOINERY

ALL CARCASSES TO BE MADE FROM 16mm Polytec Silk Matt

ALL ADJ SHELF HOLES 5X 5MM HOLES 32MM SPACINGS

ALL DRAWERS TO BE Blum Legrabox Drawer

ALL HINGES TO BE 110° BLUM SOFTCLOSE

ALL HANDLES 224mm C-Pull

Name: Grace Lewin	Phone:
Address: 187 Page St.	Sheet # 7 of 8
City: Middle Park	Date: 05/11/26
J1121 - 187 Page St - B3+B4 Robes	DRAWN MH

Fillers set back 50mm to align Kicker Depth

J1121 - 187 Page St - B3+B4 Robes









CN FITOUTS PTY LTD
CUSTOM MADE JOINERY

P 03 9761 6994
E info@cnfitouts.com.au
www.cnfitouts.com.au

6 Stephenson rd.
Bayswater North 3153

CODE	DESCRIPTION
LA1/Internals	16mm Polytec Silk Matt
LA2	18mm Laminex Paper Bark Absolute Matt
TV1	19mm Eveneer Prefinished 'Light Oak Wax, Matt'
TV2	19mm Eveneer Prefinished 'Mandel Wax, Matt'
ST1	20mm Sareva 'Natural' Stone – Marble, Honed'
ST2	20mm Travertine Litzio " Natural Stone, Filled Honed'
Handle	TBC
GRO-01	

ALL JOINERY

ALL CARCASSES TO BE MADE FROM 16mm Polytec Silk Matt

ALL ADJ SHELF HOLES 5X 5MM HOLES 32MM SPACINGS

ALL DRAWERS TO BE Blum Legrabox Drawer

ALL HINGES TO BE 110° BLUM SOFTCLOSE

ALL HANDLES 224mm C-Pull

Name: Grace Lewin

Phone:

Address: 187 Page St.

Sheet # 8 of 8

City: Middle Park

Date: 05/11/26

J1121 - 187 Page St - B3+B4 Robes

DRAWN MH