
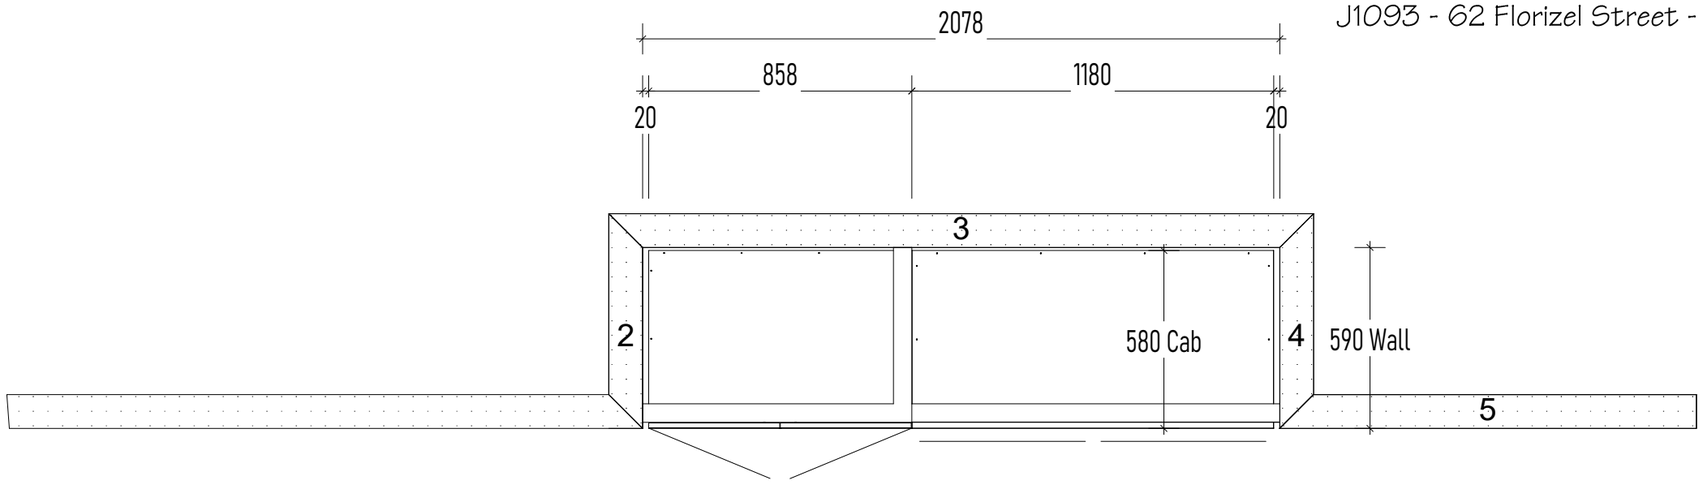


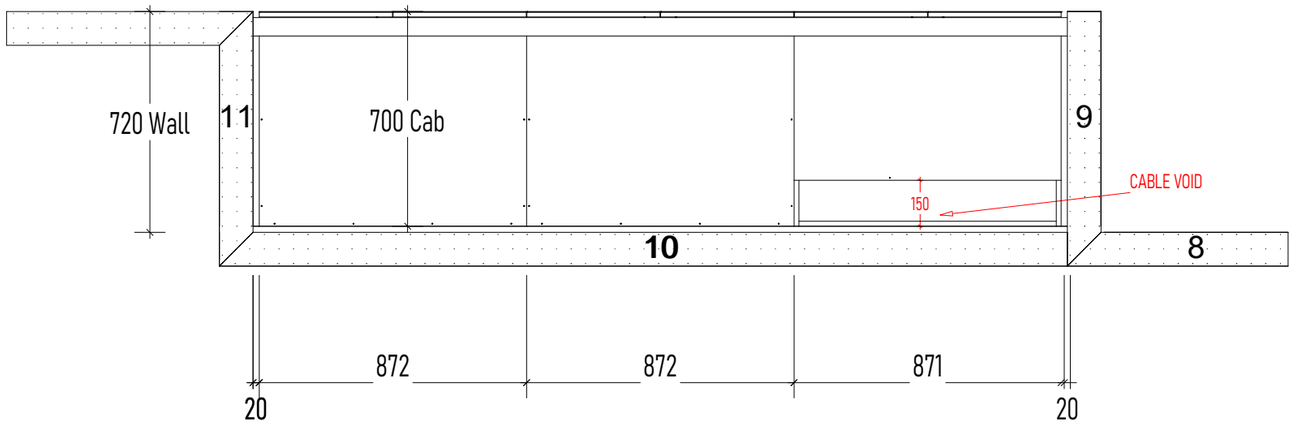

Hallway Laundry & Linen Plan

Scale: 1 : 20

CN FITOUTS PTY LTD
CUSTOM MADE JOINERY

P 03 9761 6994
E info@cnfitouts.com.au
www.cnfitouts.com.au

6 Stephenson rd.
Bayswater North 3153

CODE	DESCRIPTION
PF-1	2PAC PAINTED - SUSSEX ROUTE - COLOUR MATCH TO POLYTEC AMARO - 30% SATIN
PF-2	2PAC PAINTED - SUSSEX ROUTE - DULUX NATURAL WHITE - 30% SATIN
LAM-1	POLYTEC FLORENTINE WALNUT WOODMATT
ST-1	12MM ENVIRO SURFACES - COVE
ST-2	12MM ENVIRO SURFACES - VOLAKAS
DWR	BLUM LEGRABOX SOFTCLOSE DRAWER
ADJ	ADJUSTABLE SHELF
FXD	FIXED SHELF
LED	REBATE AND EXTRUSION ONLY

ALL JOINERY

ALL CARCASSES TO BE MADE FROM 16mm HMR White - 1mm Edge

ALL ADJ SHELF HOLES 5X 5MM HOLES 32MM SPACINGS

ALL DRAWERS TO BE Blum Legrabox Drawer

ALL HINGES TO BE 110° BLUM SOFTCLOSE

ALL HANDLES Linear Standard Brave 1040mm offset in white

Name: Veronica & Param | Phone:


Address: 62 Florizel Street | Sheet # 1 of 9


City: Glen Iris | Date: 28/09/26

J1093 - 62 Florizel Street - Hallway Laundry-Linen | DRAWN MH

Fillers set Set back 20mm - Shadowline

J1093 - 62 Florizel Street - Hallway Laundry-Linen

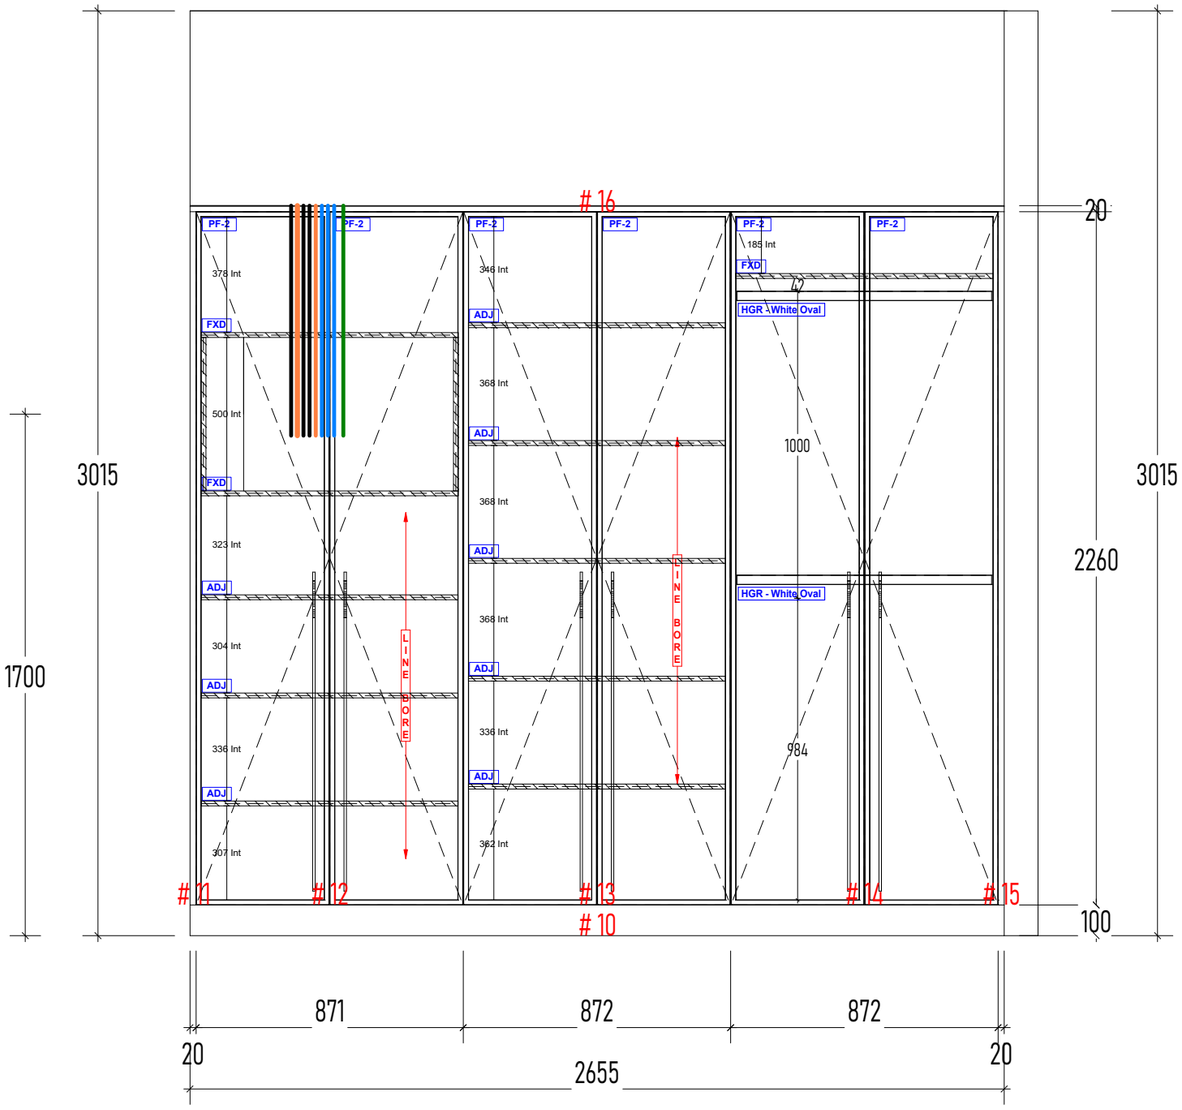

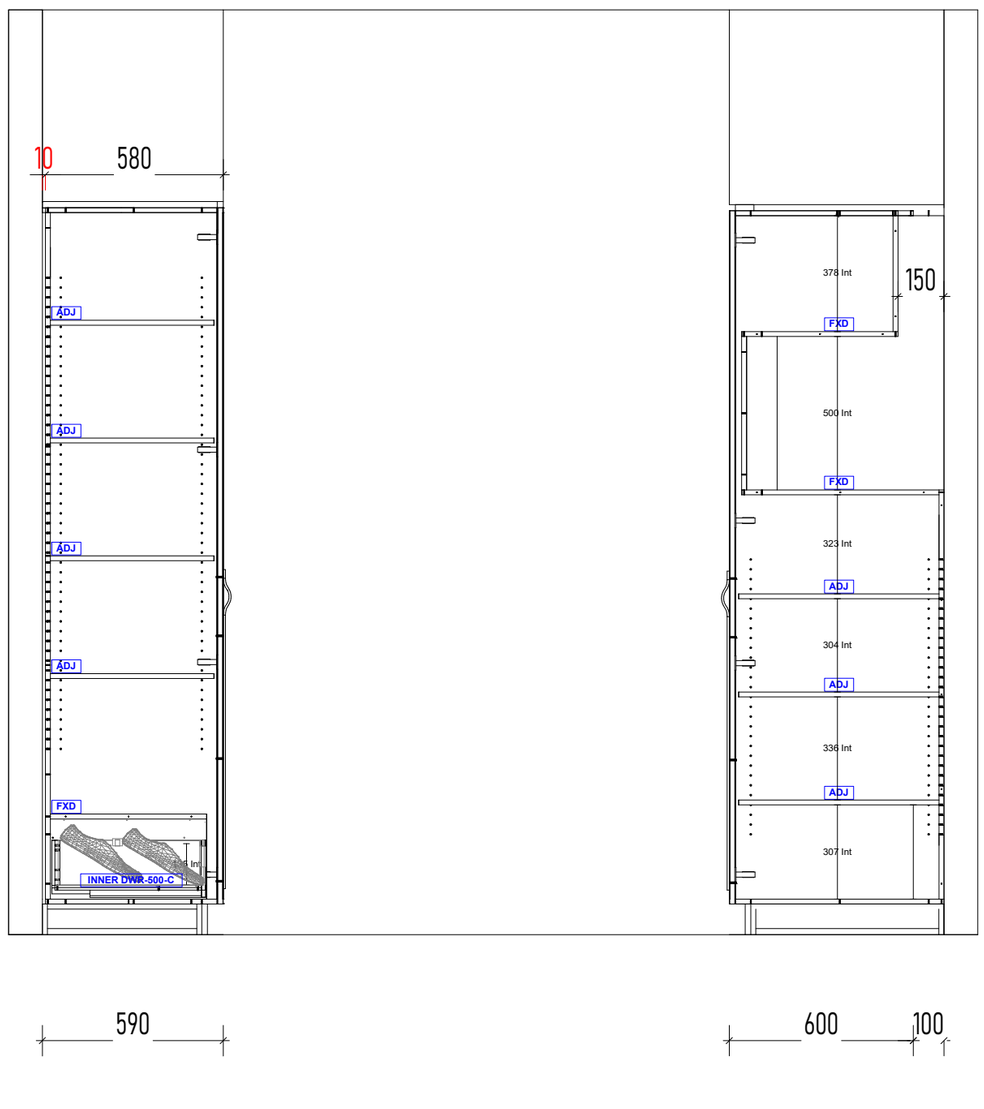

Hallway Laundry & Linen XSec

Scale: 1 : 20

CN FITOUTS PTY LTD
CUSTOM MADE JOINERY

P 03 9761 6994
E info@cnfitouts.com.au
www.cnfitouts.com.au

6 Stephenson rd.
Bayswater North 3153

CODE	DESCRIPTION
PF-1	2PAC PAINTED - SUSSEX ROUTE - COLOUR MATCH TO POLYTEC AMARO - 30% SATIN
PF-2	2PAC PAINTED - SUSSEX ROUTE - DULUX NATURAL WHITE - 30% SATIN
LAM-1	POLYTEC FLORENTINE WALNUT WOODMATT
ST-1	12MM ENVIRO SURFACES - COVE
ST-2	12MM ENVIRO SURFACES - VOLAKAS
DWR	BLUM LEGRABOX SOFTCLOSE DRAWER
ADJ	ADJUSTABLE SHELF
FXD	FIXED SHELF
LED	REBATE AND EXTRUSION ONLY

ALL JOINERY

ALL CARCASSES TO BE MADE FROM 16mm HMR White - 1mm Edge

ALL ADJ SHELF HOLES 5X 5MM HOLES 32MM SPACINGS

ALL DRAWERS TO BE Blum Legrabox Drawer

ALL HINGES TO BE 110° BLUM SOFTCLOSE

ALL HANDLES Linear Standard Brave 1040mm offset in white

Name: Veronica & Param

Phone:

Address: 62 Florizel Street

City: Glen Iris

Sheet # 2 of 9


Date: 28/09/26

J1093 - 62 Florizel Street - Hallway Laundry-Linen

DRAWN MH


Fillers set Set back 20mm - Shadowline

J1093 - 62 Florizel Street - Hallway Laundry-Linen

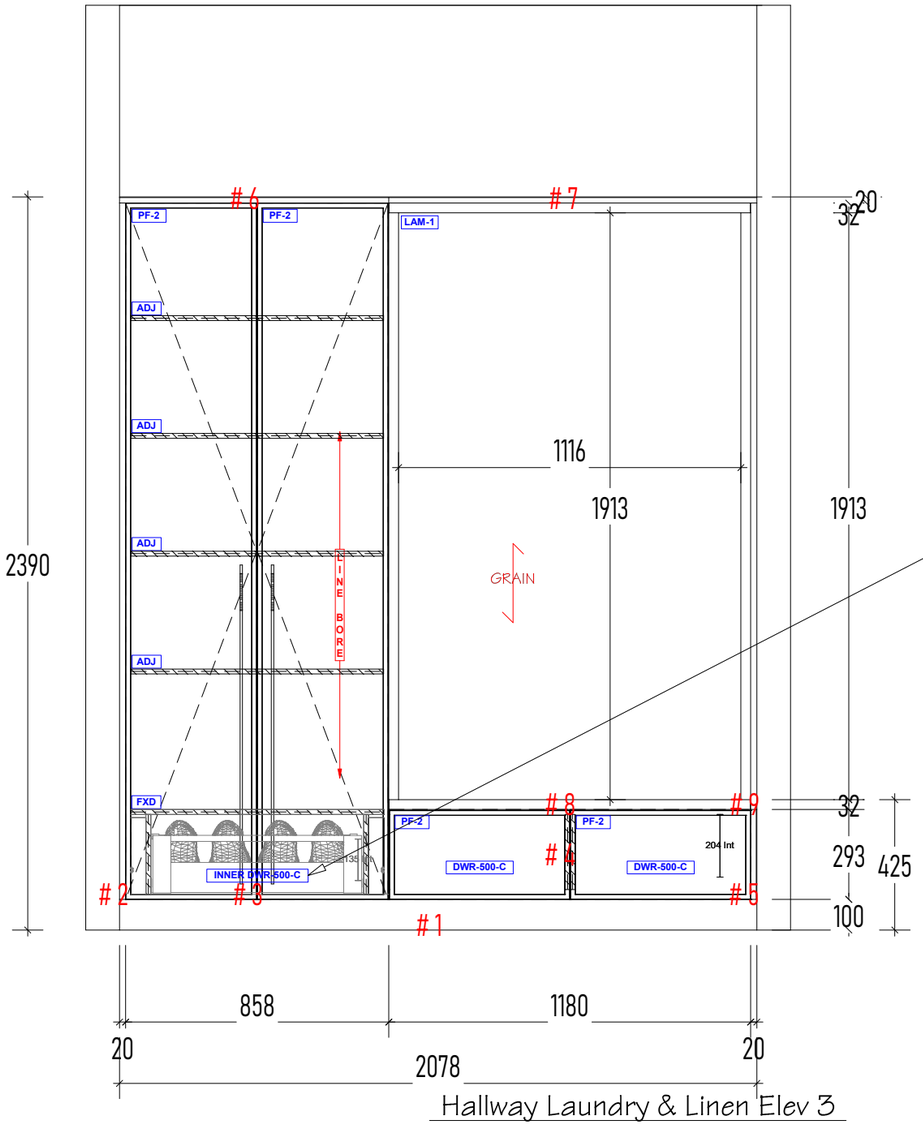


Hallway Laundry & Linen Elev 3

Scale: 1 : 20

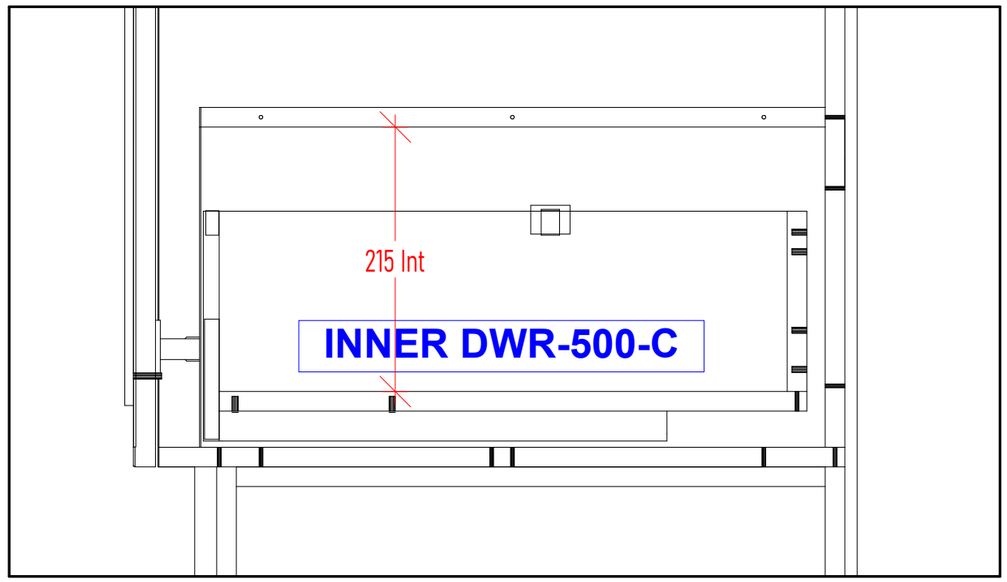


Shoe Drawer

Scale: 1 : 5

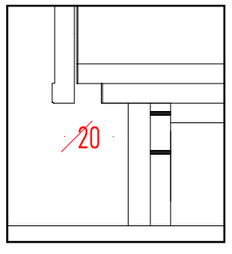

Drawer Fingerpull Detail

Scale: 1 : 5

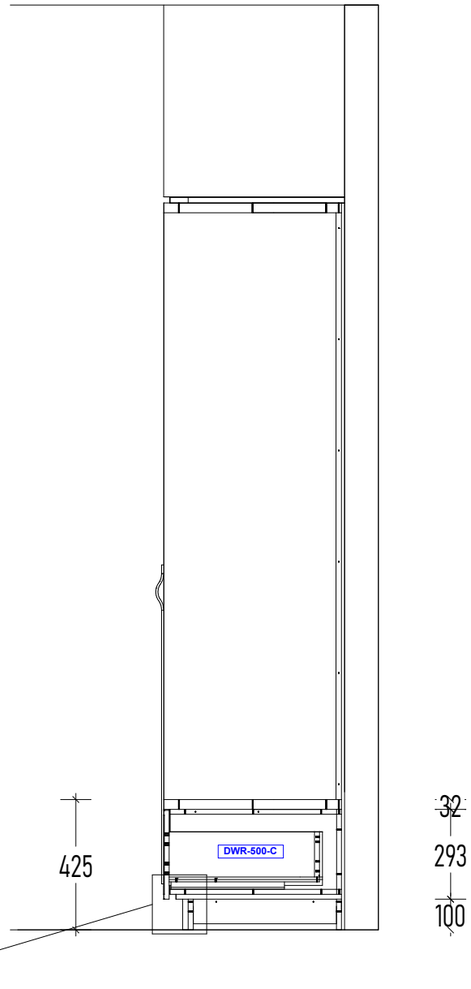

Hallway Laundry & Linen W3XSec

Scale: 1 : 20

CN FITOUTS PTY LTD
CUSTOM MADE JOINERY

P 03 9761 6994
E info@cnfitouts.com.au
www.cnfitouts.com.au

6 Stephenson rd.
Bayswater North 3153

CODE	DESCRIPTION
PF-1	2PAC PAINTED - SUSSEX ROUTE - COLOUR MATCH TO POLYTEC AMARO - 30% SATIN
PF-2	2PAC PAINTED - SUSSEX ROUTE - DULUX NATURAL WHITE - 30% SATIN
LAM-1	POLYTEC FLORENTINE WALNUT WOODMATT
ST-1	12MM ENVIRO SURFACES - COVE
ST-2	12MM ENVIRO SURFACES - VOLAKAS
DWR	BLUM LEGRABOX SOFTCLOSE DRAWER
ADJ	ADJUSTABLE SHELF
FXD	FIXED SHELF
LED	REBATE AND EXTRUSION ONLY

ALL JOINERY

ALL CARCASSES TO BE MADE FROM 16mm HMR White - 1mm Edge

ALL ADJ SHELF HOLES 5X 5MM HOLES 32MM SPACINGS

ALL DRAWERS TO BE Blum Legrabox Drawer

ALL HINGES TO BE 110° BLUM SOFTCLOSE

ALL HANDLES Linear Standard Brave 1040mm offset in white

Name: Veronica & Param

Phone:

Address: 62 Florizel Street

City: Glen Iris

Sheet # 3 of 9

Date: 28/09/26

J1093 - 62 Florizel Street - Hallway Laundry-Linen

DRAWN MH

Fillers set Set back 20mm - Shadowline





CN FITOUTS PTY LTD
CUSTOM MADE JOINERY

P 03 9761 6994
E info@cnfitouts.com.au
www.cnfitouts.com.au

6 Stephenson rd.
Bayswater North 3153

CODE	DESCRIPTION
PF-1	2PAC PAINTED - SUSSEX ROUTE - COLOUR MATCH TO POLYTEC AMARO - 30% SATIN
PF-2	2PAC PAINTED - SUSSEX ROUTE - DULUX NATURAL WHITE - 30% SATIN
LAM-1	POLYTEC FLORENTINE WALNUT WOODMATT
ST-1	12MM ENVIRO SURFACES - COVE
ST-2	12MM ENVIRO SURFACES - VOLAKAS
DWR	BLUM LEGRABOX SOFTCLOSE DRAWER
ADJ	ADJUSTABLE SHELF
FXD	FIXED SHELF
LED	REBATE AND EXTRUSION ONLY

ALL JOINERY

ALL CARCASSES TO BE MADE FROM 16mm HMR White - 1mm Edge

ALL ADJ SHELF HOLES 5X 5MM HOLES 32MM SPACINGS

ALL DRAWERS TO BE Blum Legrabox Drawer

ALL HINGES TO BE 110° BLUM SOFTCLOSE

ALL HANDLES Linear Standard Brave 1040mm offset in white

Name: Veronica & Param | Phone:

Address: 62 Florizel Street | Sheet # 4 of 9

City: Glen Iris | Date: 28/09/26

J1093 - 62 Florizel Street - Hallway Laundry-Linen | DRAWN MH

Fillers set Set back 20mm - Shadowline

J1093 - 62 Florizel Street - Hallway Laundry-Linen







CN FITOUTS PTY LTD
CUSTOM MADE JOINERY

P 03 9761 6994
E info@cnfitouts.com.au
www.cnfitouts.com.au

6 Stephenson rd.
Bayswater North 3153

CODE	DESCRIPTION
PF-1	2PAC PAINTED - SUSSEX ROUTE - COLOUR MATCH TO POLYTEC AMARO - 30% SATIN
PF-2	2PAC PAINTED - SUSSEX ROUTE - DULUX NATURAL WHITE - 30% SATIN
LAM-1	POLYTEC FLORENTINE WALNUT WOODMATT
ST-1	12MM ENVIRO SURFACES - COVE
ST-2	12MM ENVIRO SURFACES - VOLAKAS
DWR	BLUM LEGRABOX SOFTCLOSE DRAWER
ADJ	ADJUSTABLE SHELF
FXD	FIXED SHELF
LED	REBATE AND EXTRUSION ONLY

ALL JOINERY

ALL CARCASSES TO BE MADE FROM 16mm HMR White - 1mm Edge

ALL ADJ SHELF HOLES 5X 5MM HOLES 32MM SPACINGS

ALL DRAWERS TO BE Blum Legrabox Drawer

ALL HINGES TO BE 110° BLUM SOFTCLOSE

ALL HANDLES 160mm Kethy - B682 - Titanium

Name: Veronica & Param | Phone:

Address: 62 Florizel Street | Sheet # 5 of 9

City: Glen Iris | Date: 28/09/26

J1093 - 62 Florizel Street - Hallway Laundry-Linen | DRAWN MH