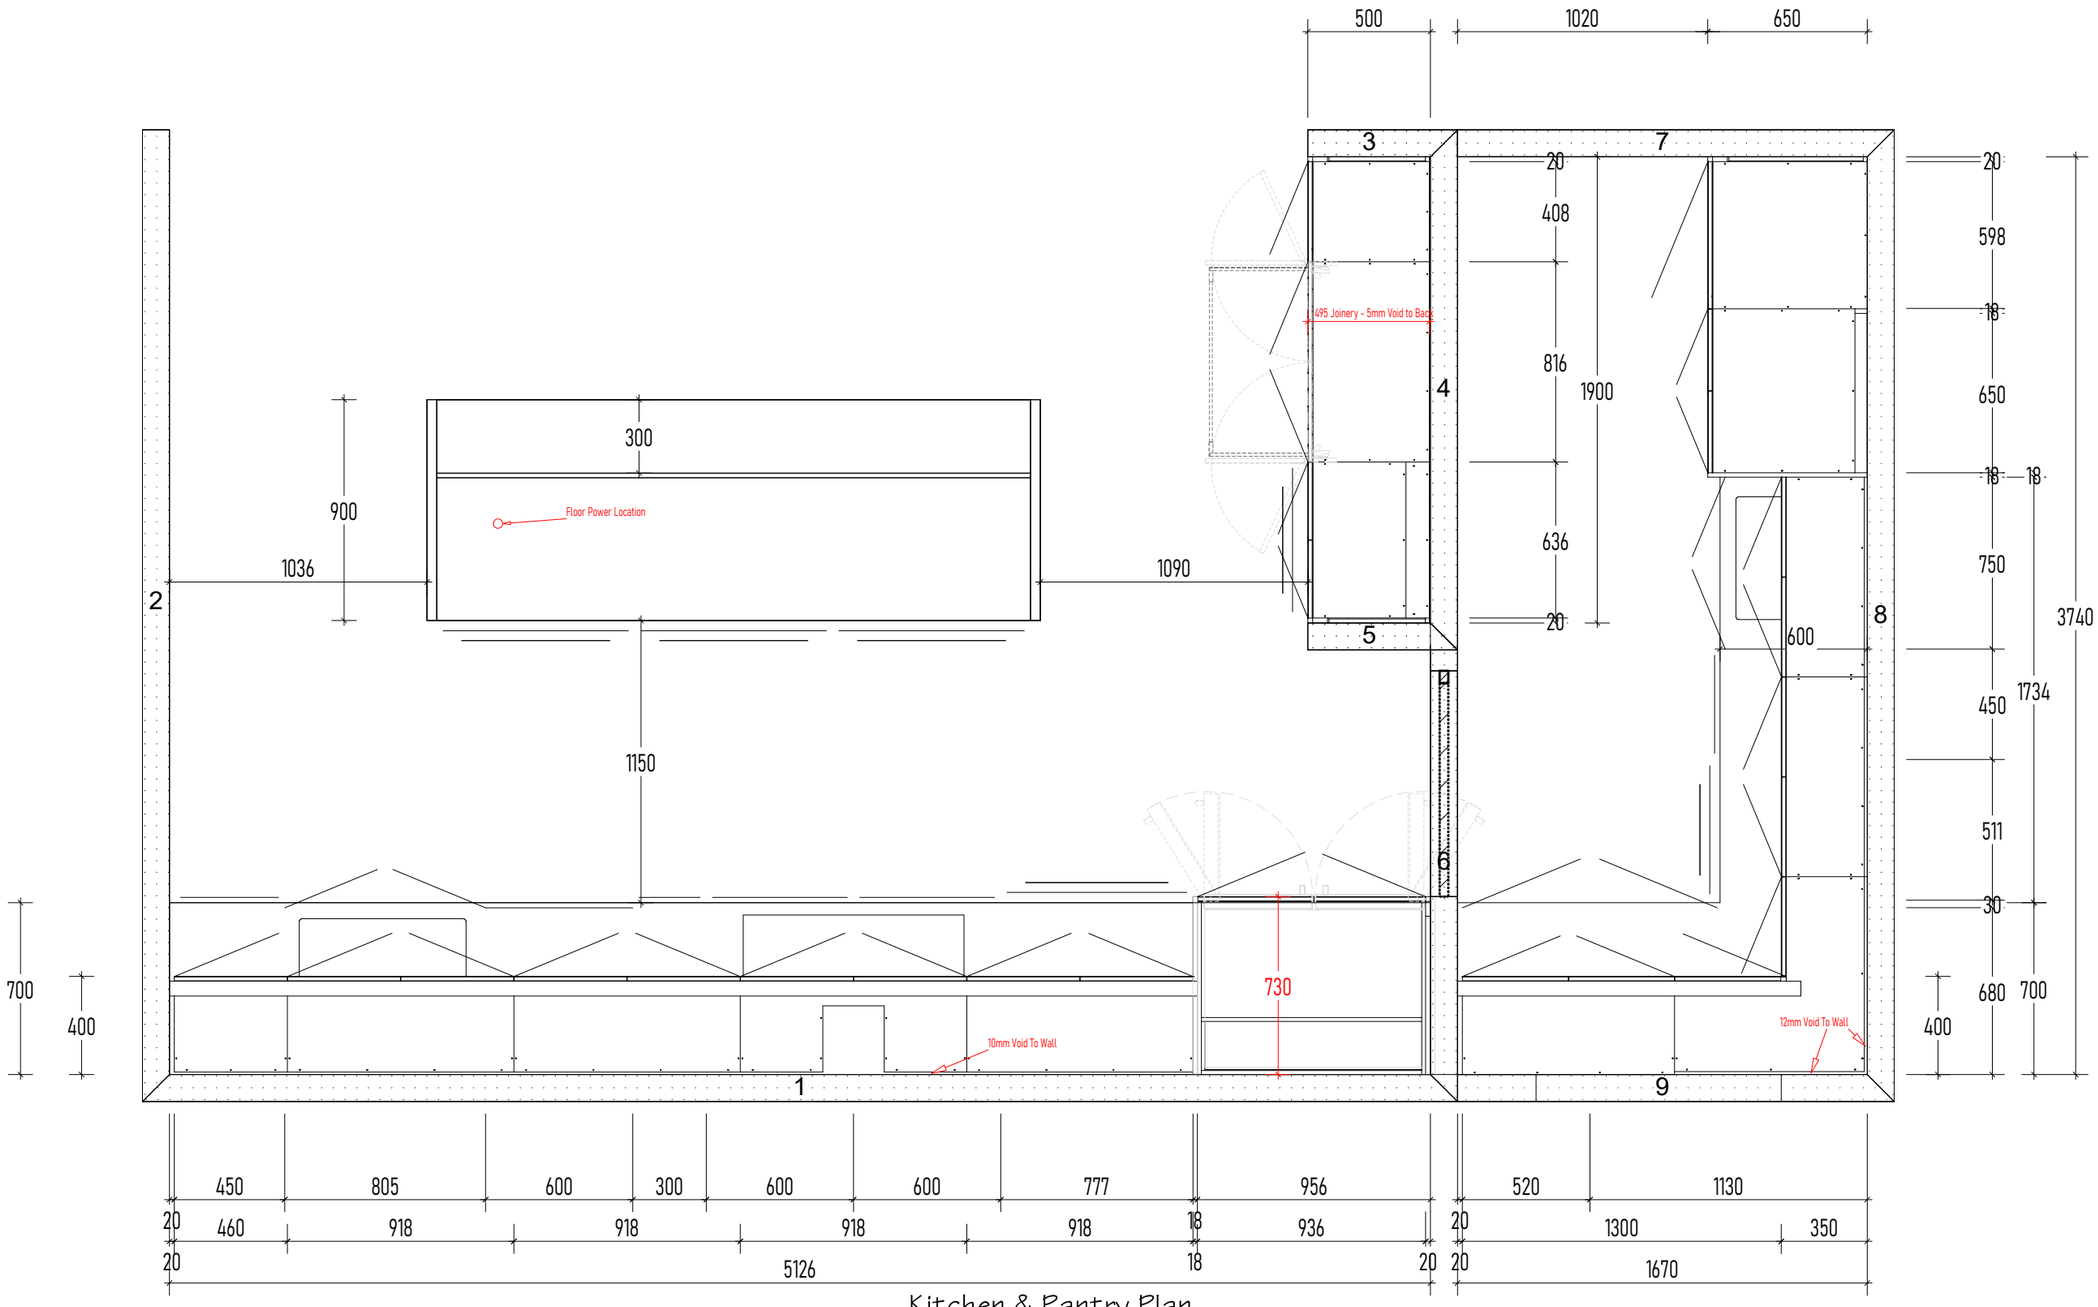



Kitchen & Pantry Plan

Scale: 1 : 25

CN FITOUTS PTY LTD
CUSTOM MADE JOINERY

P 03 9761 6994
E info@cnfitouts.com.au
www.cnfitouts.com.au

6 Stephenson rd.
Bayswater North 3153

| CODE | DESCRIPTION |
|---|---|
| PF-1 | 2PAC PAINTED - SUSSEX ROUTE - COLOUR MATCH TO POLYTEC AMARO - 30% SATIN |
| LAM-1 | POLYTEC FLORENTINE WALNUT WOODMATT |
| ST-1 | 12MM ENVIRO SURFACES - COVE |
| DWR | BLUM LEGRABOX SOFTCLOSE DRAWER |
| ADJ | ADJUSTABLE SHELF |
| FXD | FIXED SHELF |
| LED | REBATE AND EXTRUSION ONLY |

**ALL JOINERY**

ALL CARCASSES TO BE MADE FROM 16mm HMR White - 1mm Edge

ALL ADJ SHELF HOLES 5X 5MM HOLES 32MM SPACINGS

ALL DRAWERS TO BE Blum Legrabox Drawer


ALL HINGES TO BE 110° BLUM SOFTCLOSE

ALL HANDLES 160mm Kethy - B682 - Titanium

| | |
|---|---|
| Name: Veronica & Param | Phone: |
| Address: 62 Florizel Street | Sheet # 1 of 16 |
| City: Glen Iris | Date: 28/09/26 |
| J1093 - 62 Florizel Street - Kitchen & Pantry | DRAWN MH |

Fillers set Set back 20mm - Shadowline

J1093 - 62 Florizel Street - Kitchen & Pantry

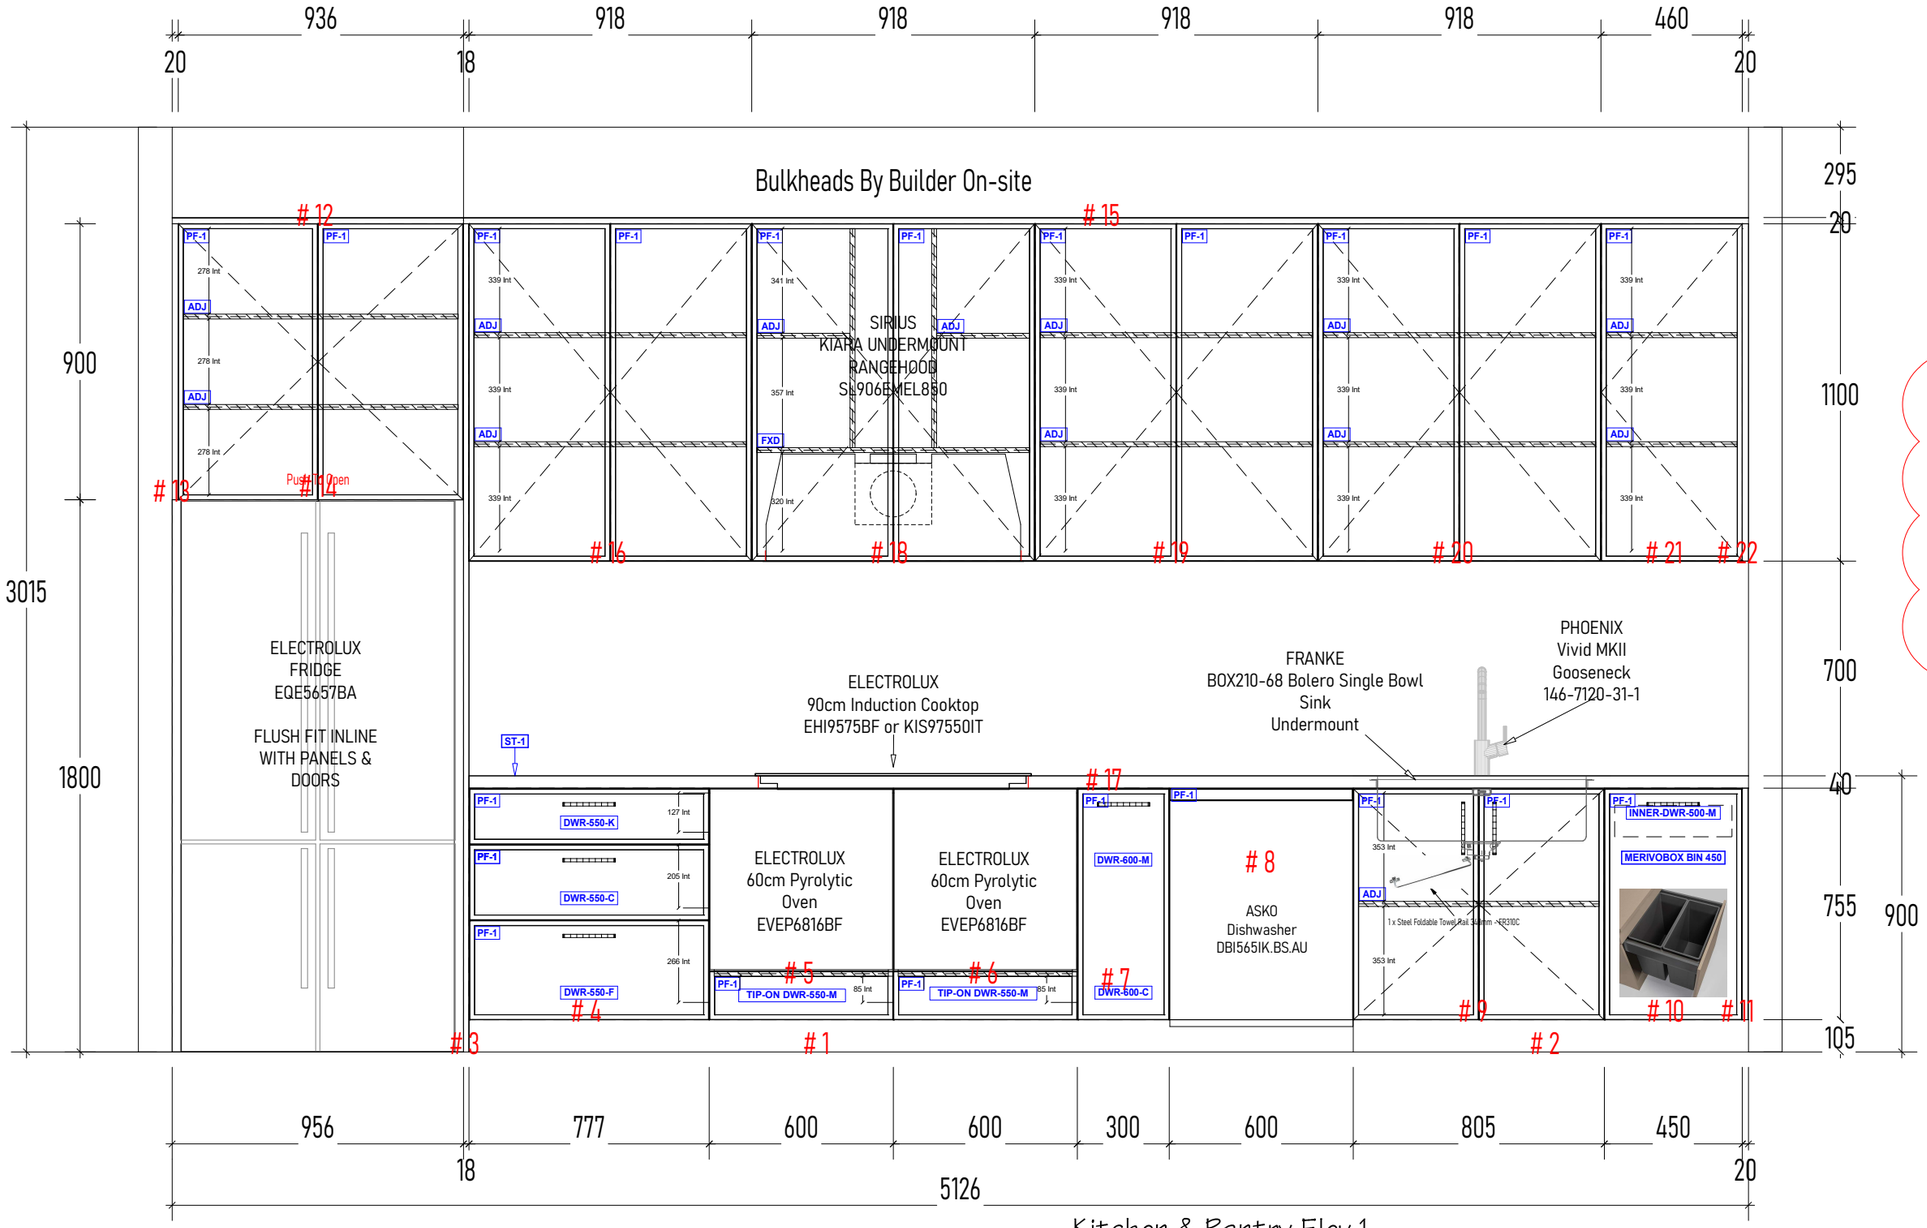


Kitchen & Pantry Elev 1

Scale: 1 : 20

Kicker height increased from 100mm to 105mm to align bottom of the dishwasher with bottom of joinery doors


CN FITOUTS PTY LTD
CUSTOM MADE JOINERY

P 03 9761 6994
E info@cnfitouts.com.au
www.cnfitouts.com.au

6 Stephenson rd.
Bayswater North 3153


| CODE | DESCRIPTION |
|---|---|
| PF-1 | 2PAC PAINTED - SUSSEX ROUTE - COLOUR MATCH TO POLYTEC AMARO - 30% SATIN |
| LAM-1 | POLYTEC FLORENTINE WALNUT WOODMATT |
| ST-1 | 12MM ENVIRO SURFACES - COVE |
| DWR | BLUM LEGRABOX SOFTCLOSE DRAWER |
| ADJ | ADJUSTABLE SHELF |
| FXD | FIXED SHELF |
| LED | REBATE AND EXTRUSION ONLY |

**ALL JOINERY**

ALL CARCASSES TO BE MADE FROM 16mm HMR White - 1mm Edge

ALL ADJ SHELF HOLES 5X 5MM HOLES 32MM SPACINGS

ALL DRAWERS TO BE Blum Legrabox Drawer


ALL HINGES TO BE 110° BLUM SOFTCLOSE

ALL HANDLES 160mm Kethy - B682 - Titanium

| | |
|---|---|
| Name: Veronica & Param | Phone: |
| Address: 62 Florizel Street | Sheet # 2 of 16 |
| City: Glen Iris | Date: 28/09/26 |
| J1093 - 62 Florizel Street - Kitchen & Pantry | DRAWN MH |


# Fillers set Set back 20mm - Shadowline

J1093 - 62 Florizel Street - Kitchen & Pantry

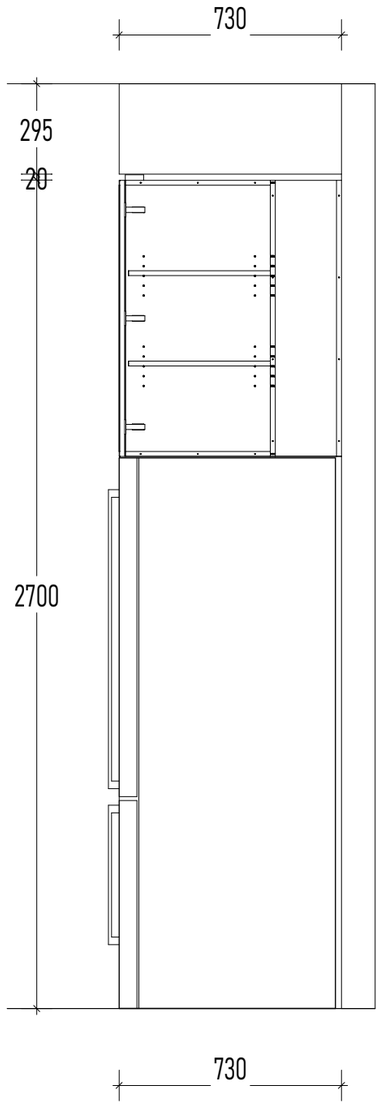



Kitchen Fridge X-Sec

Scale: 1 : 20

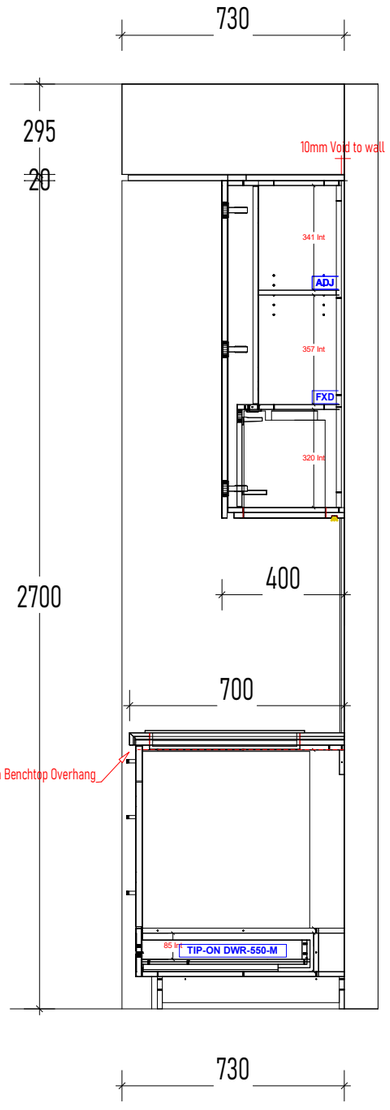



Kitchen Oven /Rhood X-Sec

Scale: 1 : 20

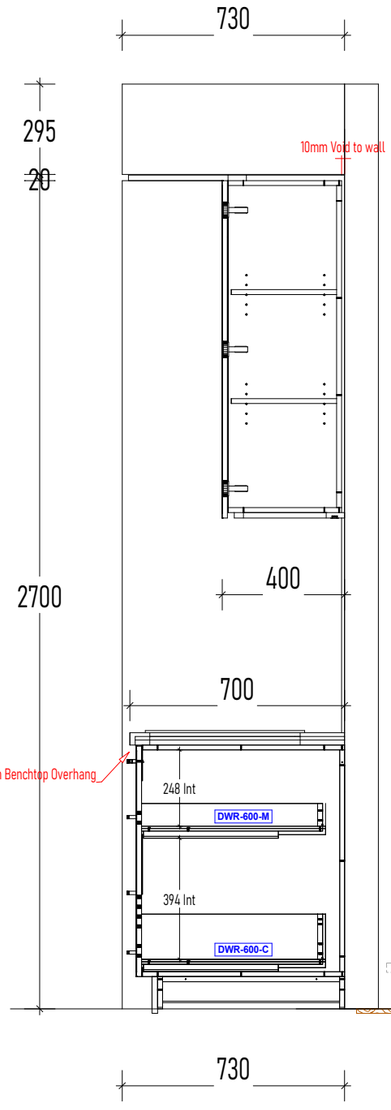



Kitchen Oil X-Sec

Scale: 1 : 20

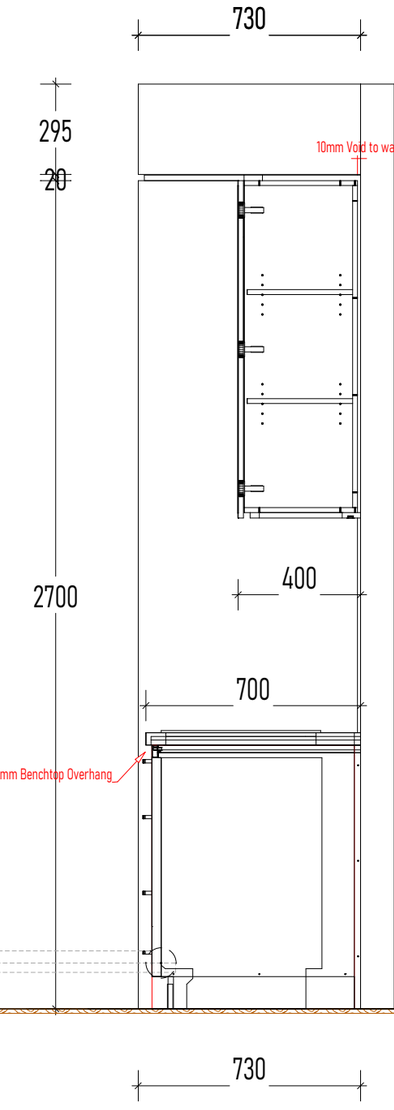



Kitchen DW X-Sec

Scale: 1 : 20

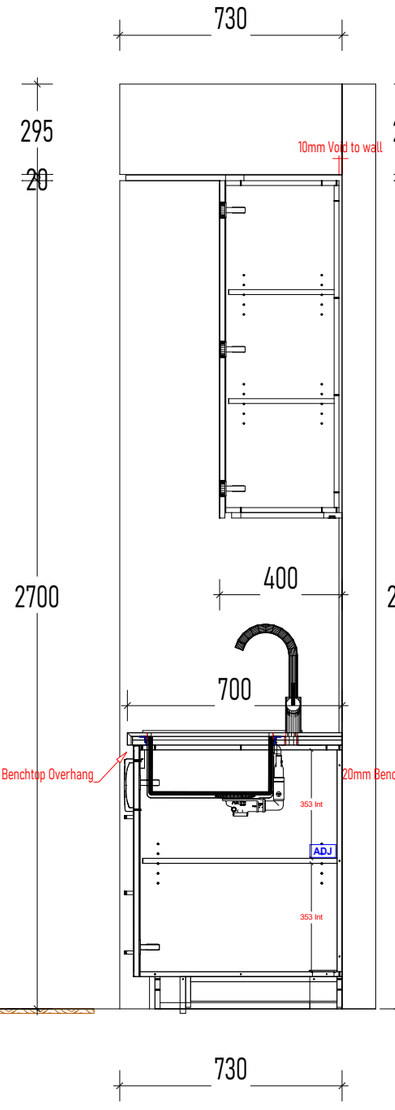


Kitchen Sink X-Sec

Scale: 1 : 20

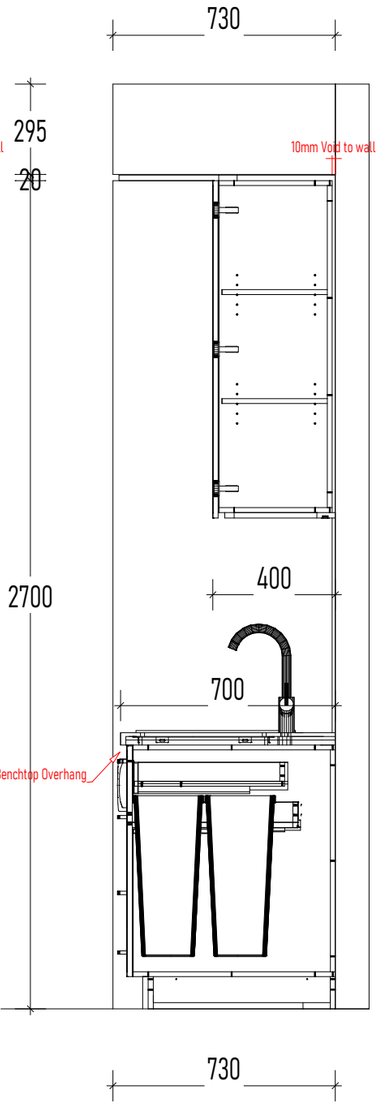


Kitchen Bin X-Sec

Scale: 1 : 20


CN FITOUTS PTY LTD
CUSTOM MADE JOINERY

P 03 9761 6994
E info@cnfitouts.com.au
www.cnfitouts.com.au

6 Stephenson rd.
Bayswater North 3153


| CODE | DESCRIPTION |
|---|---|
| PF-1 | 2PAC PAINTED - SUSSEX ROUTE - COLOUR MATCH TO POLYTEC AMARO - 30% SATIN |
| LAM-1 | POLYTEC FLORENTINE WALNUT WOODMATT |
| ST-1 | 12MM ENVIRO SURFACES - COVE |
| DWR | BLUM LEGRABOX SOFTCLOSE DRAWER |
| ADJ | ADJUSTABLE SHELF |
| FXD | FIXED SHELF |
| LED | REBATE AND EXTRUSION ONLY |

**ALL JOINERY**

ALL CARCASSES TO BE MADE FROM 16mm HMR White - 1mm Edge

ALL ADJ SHELF HOLES 5X 5MM HOLES 32MM SPACINGS

ALL DRAWERS TO BE Blum Legrabox Drawer


ALL HINGES TO BE 110° BLUM SOFTCLOSE

ALL HANDLES 160mm Kethy - B682 - Titanium

| | |
|---|---|
| Name: Veronica & Param | Phone: |
| Address: 62 Florizel Street | Sheet # 3 of 16 |
| City: Glen Iris | Date: 28/09/26 |
| J1093 - 62 Florizel Street - Kitchen & Pantry | DRAWN MH |


# Fillers set Set back 20mm - Shadowline

J1093 - 62 Florizel Street - Kitchen & Pantry

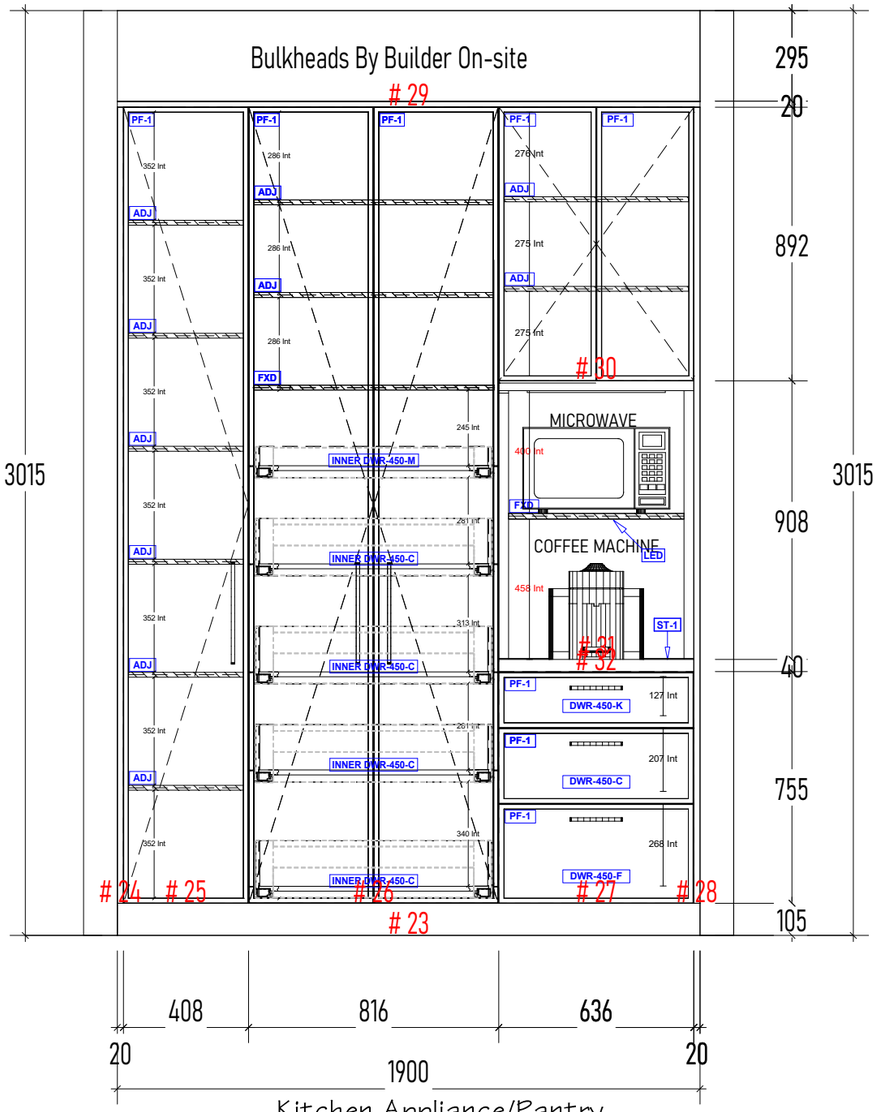



Kitchen Appliance/Pantry

Scale: 1 : 20

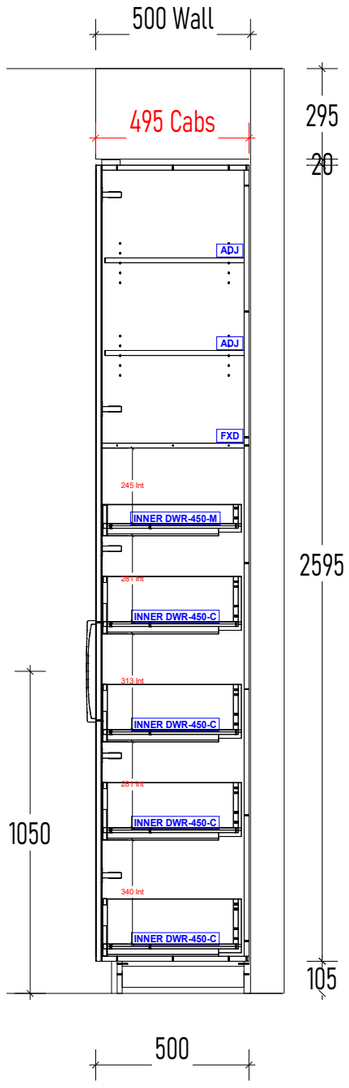


Kitchen Appliance/Pantry X-Sec

Scale: 1 : 20

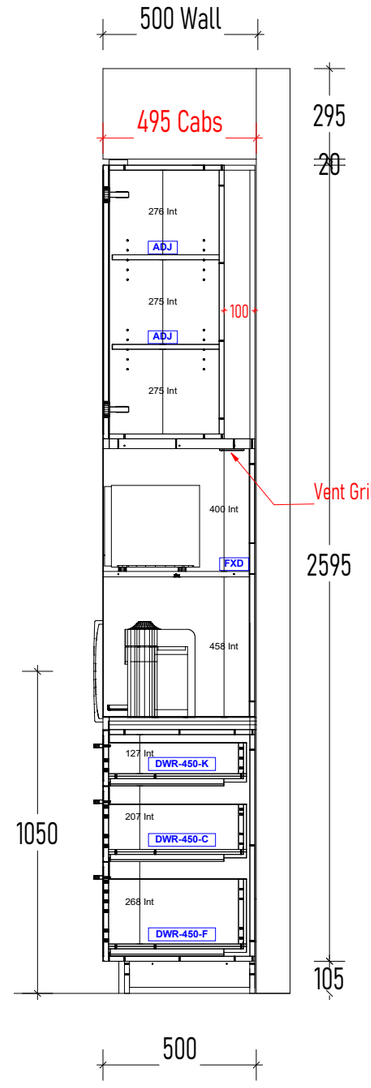


Kitchen Appliance/Pantry X-Sec

Scale: 1 : 20


CN FITOUTS PTY LTD
CUSTOM MADE JOINERY

P 03 9761 6994
E info@cnfitouts.com.au
www.cnfitouts.com.au

6 Stephenson rd.
Bayswater North 3153


| CODE | DESCRIPTION |
|---|---|
| PF-1 | 2PAC PAINTED - SUSSEX ROUTE - COLOUR MATCH TO POLYTEC AMARO - 30% SATIN |
| LAM-1 | POLYTEC FLORENTINE WALNUT WOODMATT |
| ST-1 | 12MM ENVIRO SURFACES - COVE |
| DWR | BLUM LEGRABOX SOFTCLOSE DRAWER |
| ADJ | ADJUSTABLE SHELF |
| FXD | FIXED SHELF |
| LED | REBATE AND EXTRUSION ONLY |

**ALL JOINERY**

ALL CARCASSES TO BE MADE FROM 16mm HMR White - 1mm Edge

ALL ADJ SHELF HOLES 5X 5MM HOLES 32MM SPACINGS

ALL DRAWERS TO BE Blum Legrabox Drawer


ALL HINGES TO BE 110° BLUM SOFTCLOSE

ALL HANDLES 160mm Kethy - B682 - Titanium


| | |
|---|---|
| Name: Veronica & Param | Phone: |
| Address: 62 Florizel Street | Sheet # 4 of 16 |
| City: Glen Iris | Date: 28/09/26 |
| J1093 - 62 Florizel Street - Kitchen & Pantry | DRAWN MH |

# Fillers set Set back 20mm - Shadowline



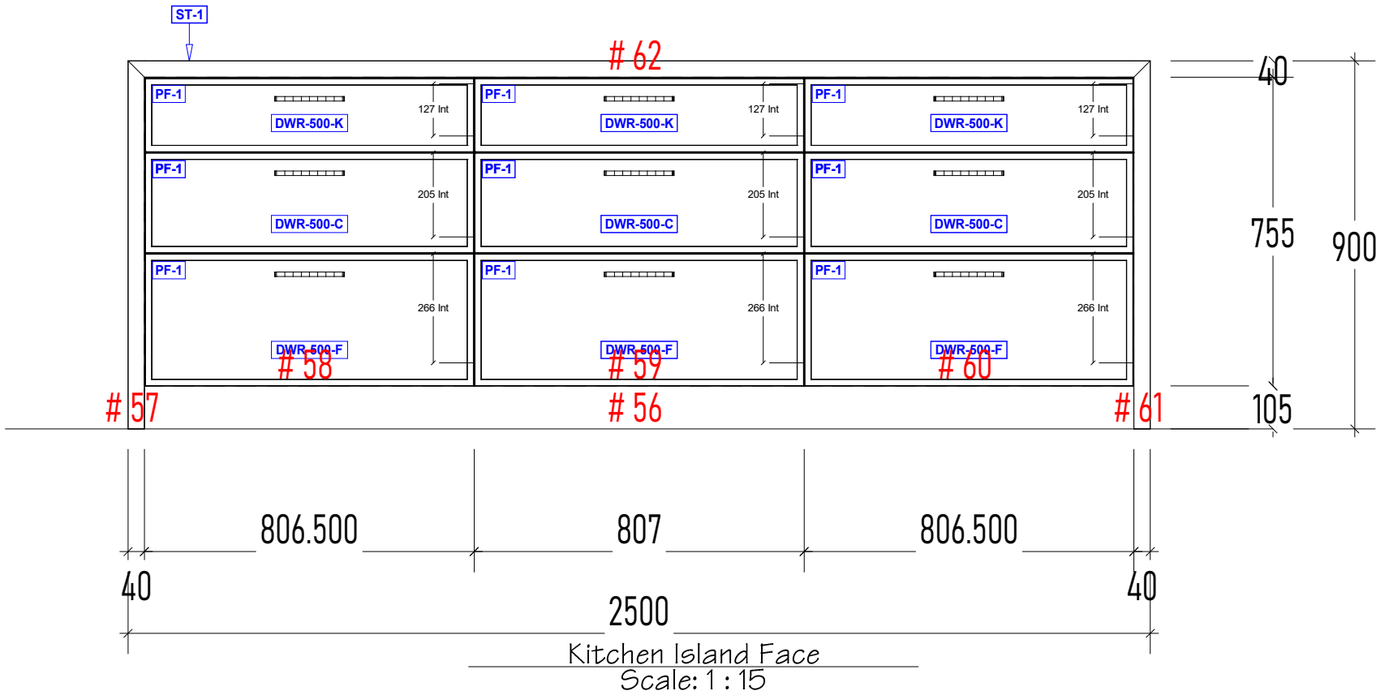



Kitchen Island Face
Scale: 1 : 15

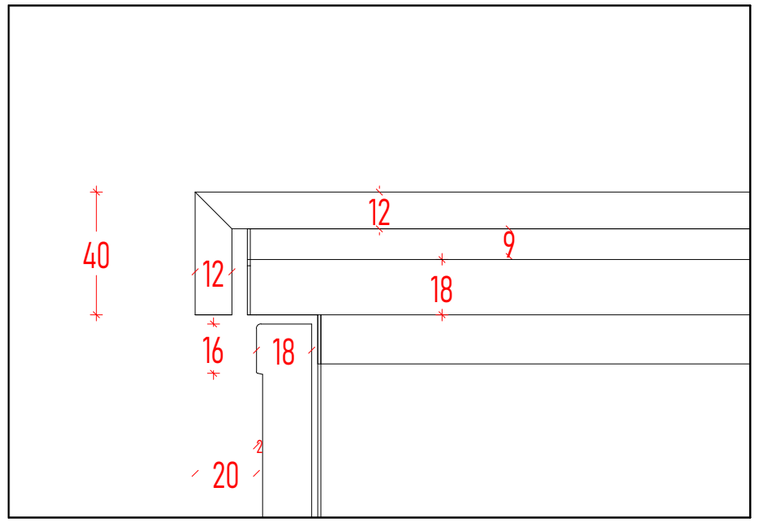



20mm O/Hang Benchtop Detail

Scale: 1 : 2

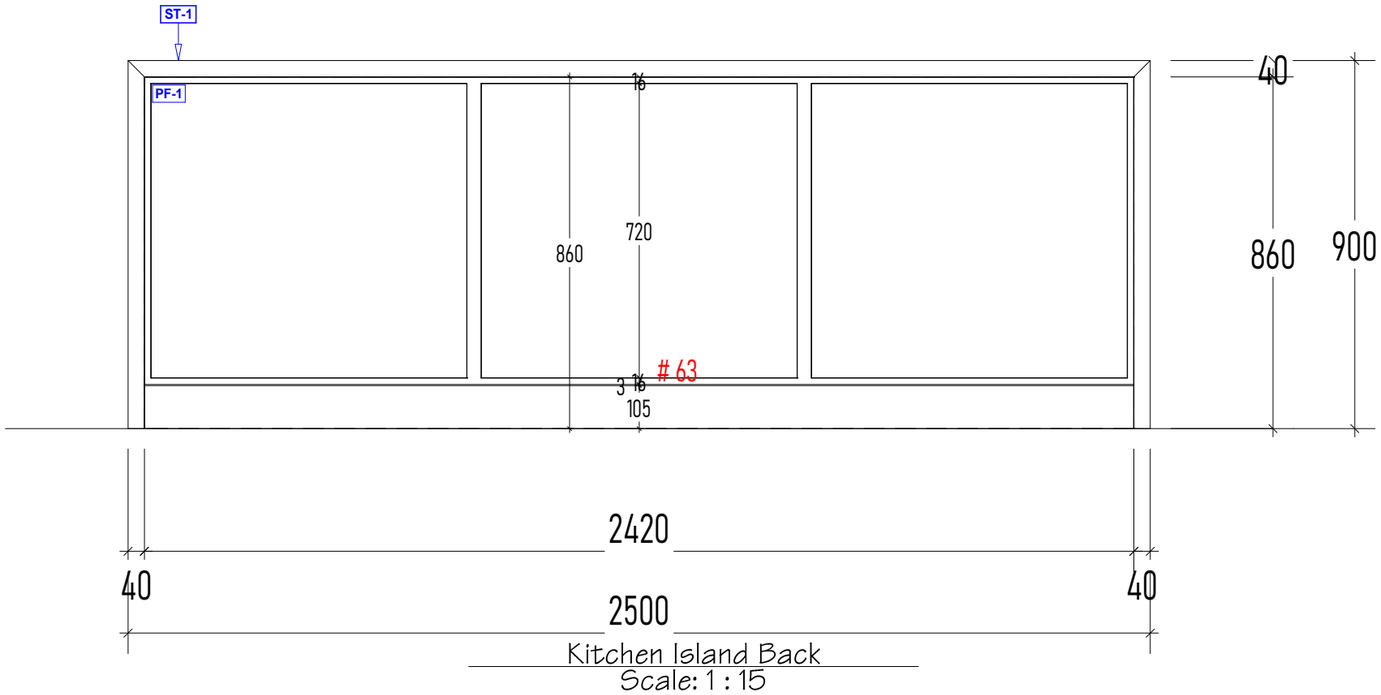


Kitchen Island Back
Scale: 1 : 15

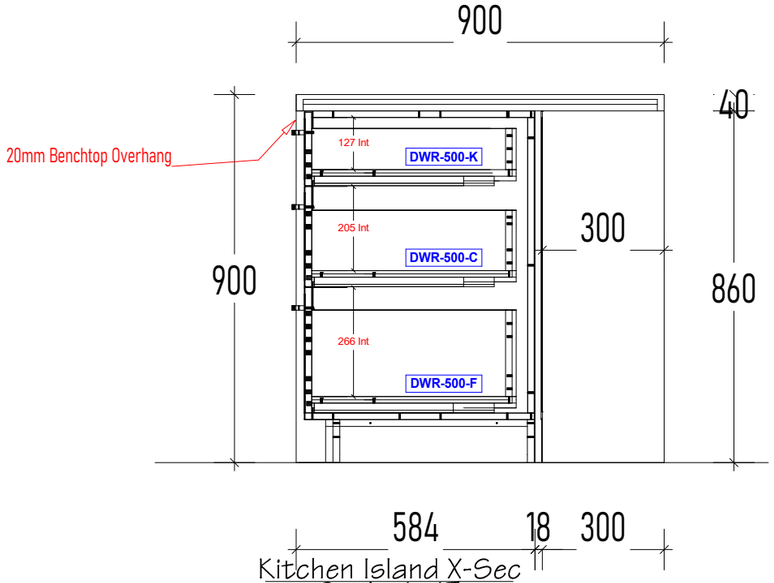



Kitchen Island X-Sec
Scale: 1 : 15

CN FITOUTS PTY LTD
CUSTOM MADE JOINERY

P 03 9761 6994
E info@cnfitouts.com.au
www.cnfitouts.com.au

6 Stephenson rd.
Bayswater North 3153

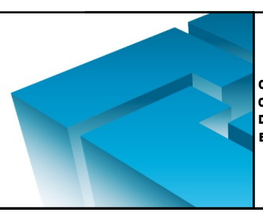

| CODE | DESCRIPTION |
|---|---|
| PF-1 | 2PAC PAINTED - SUSSEX ROUTE - COLOUR MATCH TO POLYTEC AMARO - 30% SATIN |
| LAM-1 | POLYTEC FLORENTINE WALNUT WOODMATT |
| ST-1 | 12MM ENVIRO SURFACES - COVE |
| DWR | BLUM LEGRABOX SOFTCLOSE DRAWER |
| ADJ | ADJUSTABLE SHELF |
| FXD | FIXED SHELF |
| LED | REBATE AND EXTRUSION ONLY |

**ALL JOINERY**

ALL CARCASSES TO BE MADE FROM 16mm HMR White - 1mm Edge

ALL ADJ SHELF HOLES 5X 5MM HOLES 32MM SPACINGS

ALL DRAWERS TO BE Blum Legrabox Drawer


ALL HINGES TO BE 110° BLUM SOFTCLOSE

ALL HANDLES 160mm Kethy - B682 - Titanium

| | |
|---|---|
| Name: Veronica & Param | Phone: |
| Address: 62 Florizel Street | Sheet # 5 of 16 |
| City: Glen Iris | Date: 28/09/26 |
| J1093 - 62 Florizel Street - Kitchen & Pantry | DRAWN MH |


# Fillers set Set back 20mm - Shadowline

J1093 - 62 Florizel Street - Kitchen & Pantry

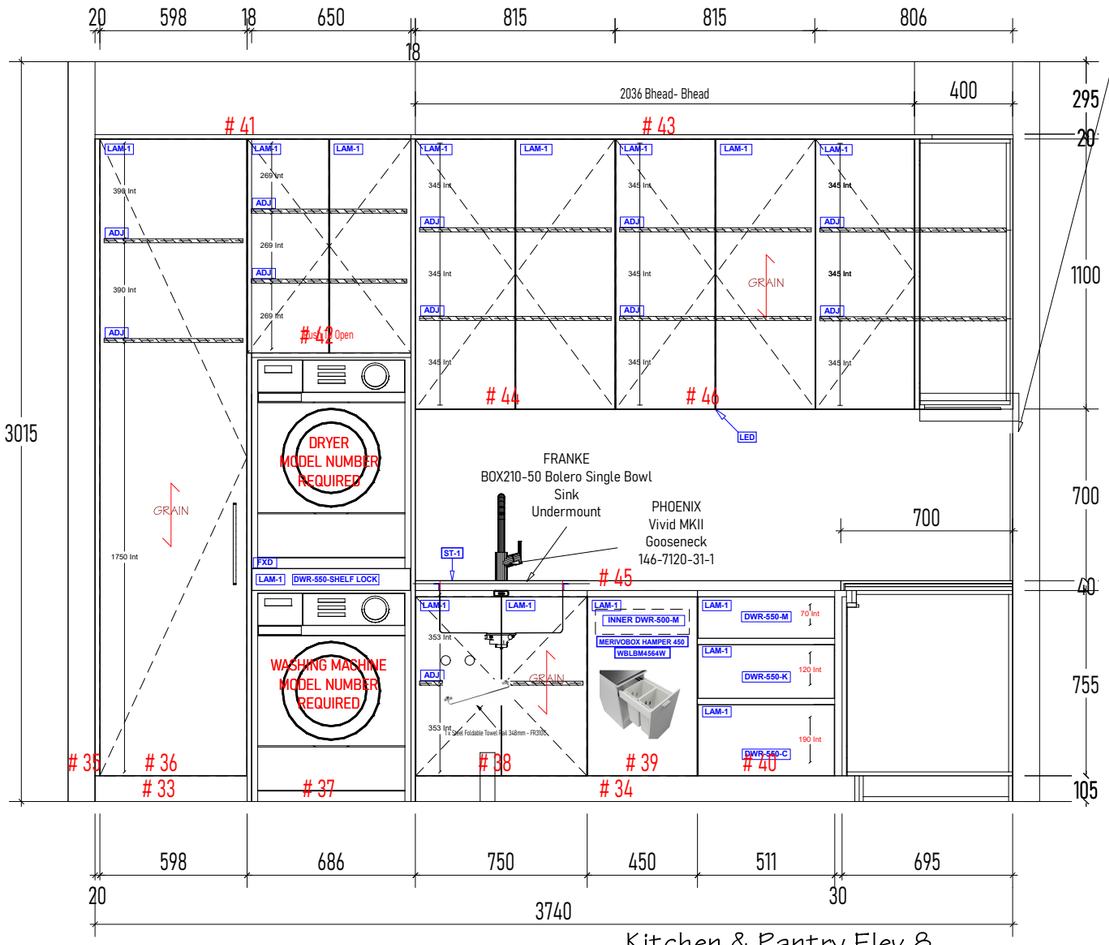



Kitchen & Pantry Elev 8

Scale: 1 : 25

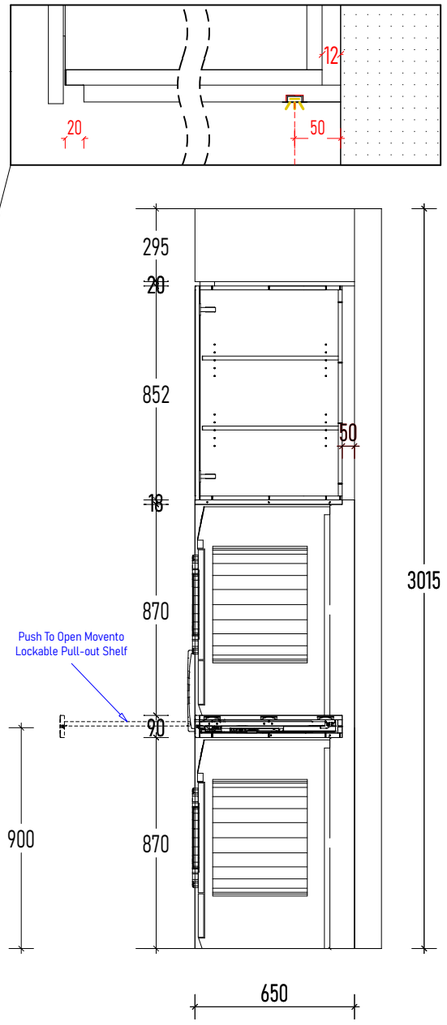



Washer/Dryer X-Sec

Scale: 1 : 25

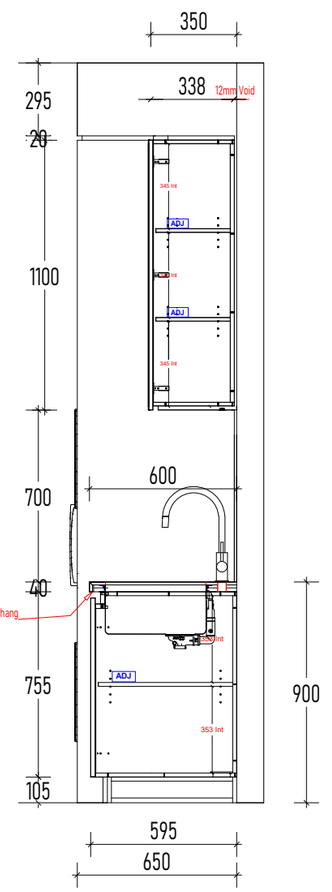


Sink X-Sec

Scale: 1 : 25

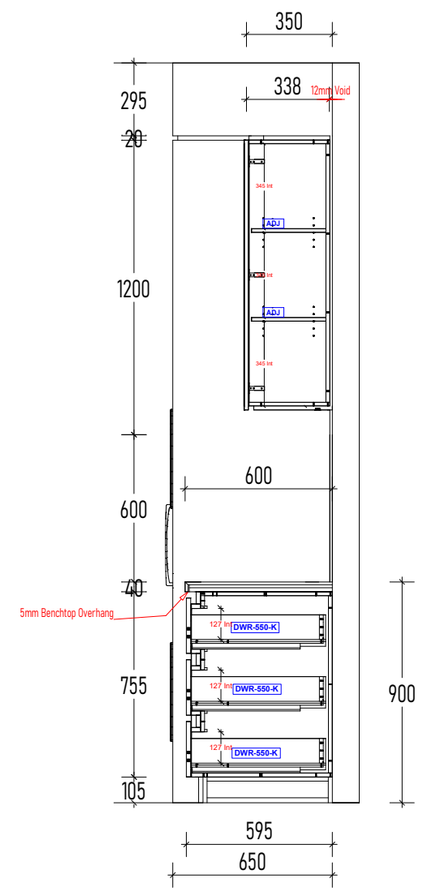


Drawer Bank X-Sec

Scale: 1 : 25


CN FITOUTS PTY LTD
CUSTOM MADE JOINERY

P 03 9761 6994
E info@cnfitouts.com.au
www.cnfitouts.com.au

6 Stephenson rd.
Bayswater North 3153


| CODE | DESCRIPTION |
|---|---|
| PF-1 | 2PAC PAINTED - SUSSEX ROUTE - COLOUR MATCH TO POLYTEC AMARO - 30% SATIN |
| LAM-1 | POLYTEC FLORENTINE WALNUT WOODMATT |
| ST-1 | 12MM ENVIRO SURFACES - COVE |
| DWR | BLUM LEGRABOX SOFTCLOSE DRAWER |
| ADJ | ADJUSTABLE SHELF |
| FXD | FIXED SHELF |
| LED | REBATE AND EXTRUSION ONLY |

**ALL JOINERY**

ALL CARCASSES TO BE MADE FROM 16mm HMR White - 1mm Edge

ALL ADJ SHELF HOLES 5X 5MM HOLES 32MM SPACINGS

ALL DRAWERS TO BE Blum Legrabox Drawer


ALL HINGES TO BE 110° BLUM SOFTCLOSE


ALL HANDLES 160mm Kethy - B682 - Titanium

| | |
|---|---|
| Name: Veronica & Param | Phone: |
| Address: 62 Florizel Street | Sheet # 6 of 16 |
| City: Glen Iris | Date: 28/09/26 |
| J1093 - 62 Florizel Street - Kitchen & Pantry | DRAWN MH |


# Fillers set Set back 20mm - Shadowline



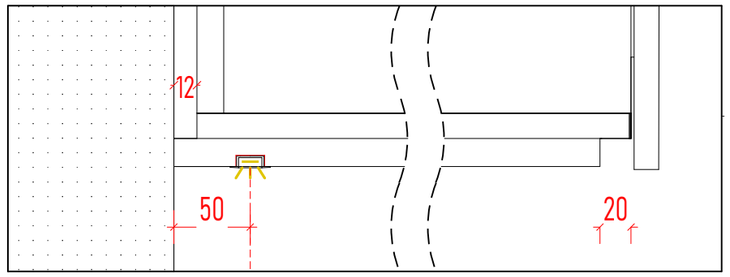


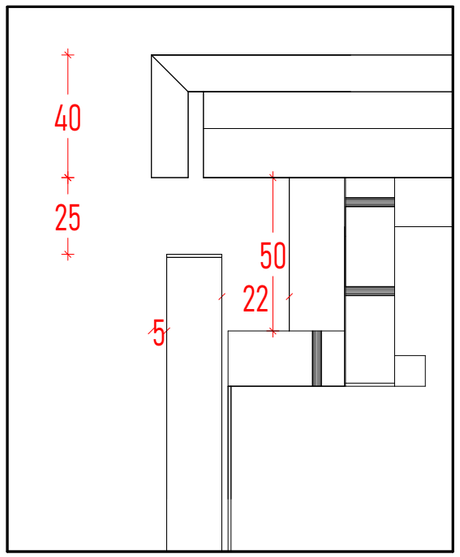
## L SHAPE RAIL DETAIL

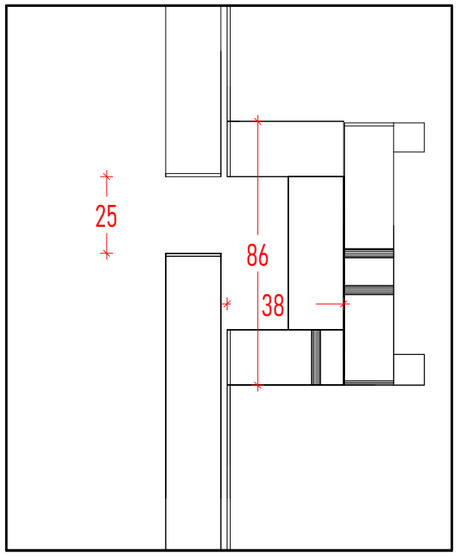



## C SHAPE RAIL DETAIL

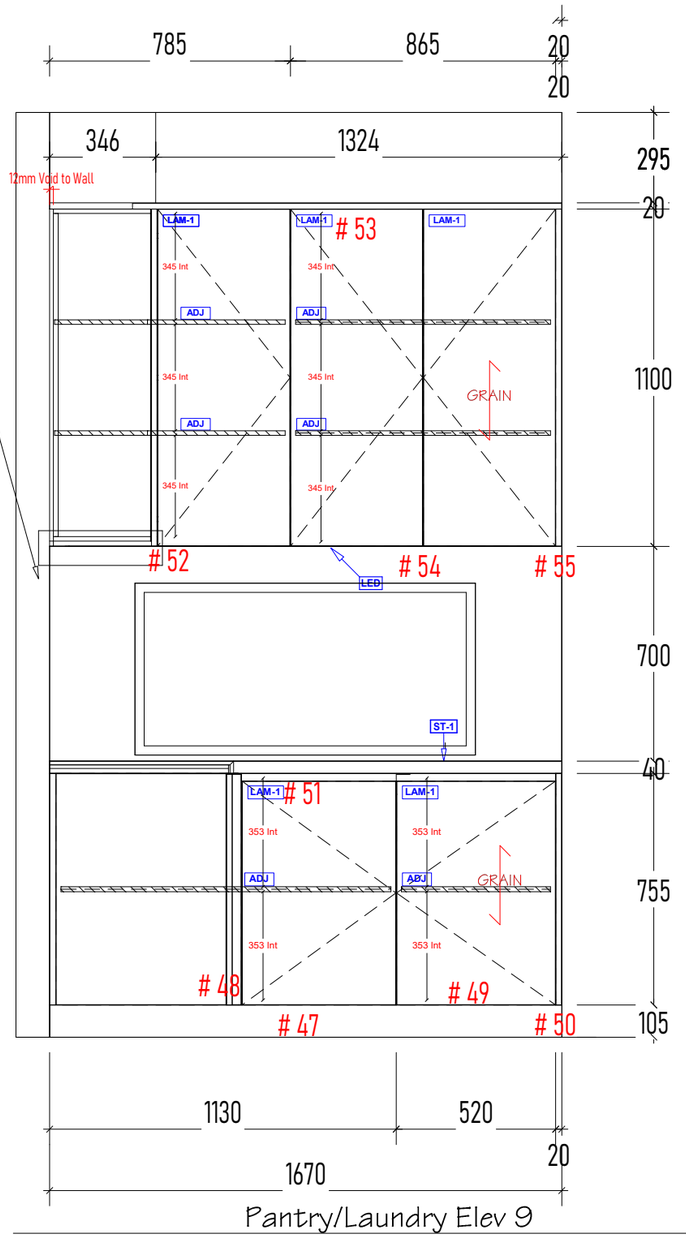


Pantry/Laundry Elev 9

Scale: 1 : 20

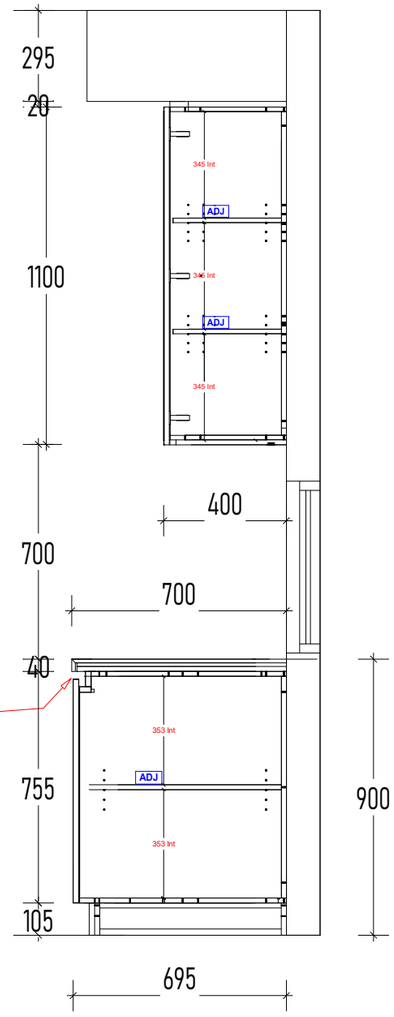


Pantry/Window X-Sec

Scale: 1 : 20

CN FITOUTS PTY LTD
CUSTOM MADE JOINERY

P 03 9761 6994
E info@cnfitouts.com.au
www.cnfitouts.com.au

6 Stephenson rd.
Bayswater North 3153

| CODE | DESCRIPTION |
|---|---|
| PF-1 | 2PAC PAINTED - SUSSEX ROUTE - COLOUR MATCH TO POLYTEC AMARO - 30% SATIN |
| LAM-1 | POLYTEC FLORENTINE WALNUT WOODMATT |
| ST-1 | 12MM ENVIRO SURFACES - COVE |
| DWR | BLUM LEGRABOX SOFTCLOSE DRAWER |
| ADJ | ADJUSTABLE SHELF |
| FXD | FIXED SHELF |
| LED | REBATE AND EXTRUSION ONLY |

**ALL JOINERY**

ALL CARCASSES TO BE MADE FROM 16mm HMR White - 1mm Edge

ALL ADJ SHELF HOLES 5X 5MM HOLES 32MM SPACINGS

ALL DRAWERS TO BE Blum Legrabox Drawer

ALL HINGES TO BE 110° BLUM SOFTCLOSE

ALL HANDLES 160mm Kethy - B682 - Titanium

| | |
|---|---|
| Name: Veronica & Param | Phone: |
| Address: 62 Florizel Street | Sheet # 7 of 16 |
| City: Glen Iris | Date: 28/09/26 |
| J1093 - 62 Florizel Street - Kitchen & Pantry | DRAWN MH |

Fillers set Set back 20mm - Shadowline

J1093 - 62 Florizel Street - Kitchen & Pantry




CN FITOUTS PTY LTD
CUSTOM MADE JOINERY

P 03 9761 6994
E info@cnfitouts.com.au
www.cnfitouts.com.au

6 Stephenson rd.
Bayswater North 3153


| CODE | DESCRIPTION |
|---|---|
| PF-1 | 2PAC PAINTED - SUSSEX ROUTE - COLOUR MATCH TO POLYTEC AMARO - 30% SATIN |
| LAM-1 | POLYTEC FLORENTINE WALNUT WOODMATT |
| ST-1 | 12MM ENVIRO SURFACES - COVE |
| DWR | BLUM LEGRABOX SOFTCLOSE DRAWER |
| ADJ | ADJUSTABLE SHELF |
| FXD | FIXED SHELF |
| LED | REBATE AND EXTRUSION ONLY |

**ALL JOINERY**

ALL CARCASSES TO BE MADE FROM 16mm HMR White - 1mm Edge

ALL ADJ SHELF HOLES 5X 5MM HOLES 32MM SPACINGS

ALL DRAWERS TO BE Blum Legrabox Drawer

ALL HINGES TO BE 110° BLUM SOFTCLOSE

ALL HANDLES 160mm Kethy - B682 - Titanium

Name: Veronica & Param

Phone:

Address: 62 Florizel Street

Sheet # 8 of 16

City: Glen Iris

Date: 28/09/26

J1093 - 62 Florizel Street - Kitchen & Pantry

DRAWN MH

Fillers set Set back 20mm - Shadowline







CN FITOUTS PTY LTD
CUSTOM MADE JOINERY

P 03 9761 6994
E info@cnfitouts.com.au
www.cnfitouts.com.au

6 Stephenson rd.
Bayswater North 3153

| CODE | DESCRIPTION |
|---|---|
| PF-1 | 2PAC PAINTED - SUSSEX ROUTE - COLOUR MATCH TO POLYTEC AMARO - 30% SATIN |
| LAM-1 | POLYTEC FLORENTINE WALNUT WOODMATT |
| ST-1 | 12MM ENVIRO SURFACES - COVE |
| DWR | BLUM LEGRABOX SOFTCLOSE DRAWER |
| ADJ | ADJUSTABLE SHELF |
| FXD | FIXED SHELF |
| LED | REBATE AND EXTRUSION ONLY |

**ALL JOINERY**

ALL CARCASSES TO BE MADE FROM 16mm HMR White - 1mm Edge

ALL ADJ SHELF HOLES 5X 5MM HOLES 32MM SPACINGS

ALL DRAWERS TO BE Blum Legrabox Drawer

ALL HINGES TO BE 110° BLUM SOFTCLOSE

ALL HANDLES 160mm Kethy - B682 - Titanium

Name: Veronica & Param | Phone:

Address: 62 Florizel Street | Sheet # 9 of 16

City: Glen Iris | Date: 28/09/26

J1093 - 62 Florizel Street - Kitchen & Pantry | DRAWN MH

Fillers set Set back 20mm - Shadowline

J1093 - 62 Florizel Street - Kitchen & Pantry




CN FITOUTS PTY LTD
CUSTOM MADE JOINERY

P 03 9761 6994
E info@cnfitouts.com.au
www.cnfitouts.com.au

6 Stephenson rd.
Bayswater North 3153


| CODE | DESCRIPTION |
|---|---|
| PF-1 | 2PAC PAINTED - SUSSEX ROUTE - COLOUR MATCH TO POLYTEC AMARO - 30% SATIN |
| LAM-1 | POLYTEC FLORENTINE WALNUT WOODMATT |
| ST-1 | 12MM ENVIRO SURFACES - COVE |
| DWR | BLUM LEGRABOX SOFTCLOSE DRAWER |
| ADJ | ADJUSTABLE SHELF |
| FXD | FIXED SHELF |
| LED | REBATE AND EXTRUSION ONLY |

**ALL JOINERY**

ALL CARCASSES TO BE MADE FROM 16mm HMR White - 1mm Edge

ALL ADJ SHELF HOLES 5X 5MM HOLES 32MM SPACINGS

ALL DRAWERS TO BE Blum Legrabox Drawer

ALL HINGES TO BE 110° BLUM SOFTCLOSE

ALL HANDLES 160mm Kethy - B682 - Titanium

Name: Veronica & Param | Phone:

Address: 62 Florizel Street | Sheet #10 of 16

City: Glen Iris | Date: 28/09/26

J1093 - 62 Florizel Street - Kitchen & Pantry | DRAWN MH

Fillers set Set back 20mm - Shadowline





CN FITOUTS PTY LTD
CUSTOM MADE JOINERY

P 03 9761 6994
E info@cnfitouts.com.au
www.cnfitouts.com.au

6 Stephenson rd.
Bayswater North 3153

| CODE | DESCRIPTION |
|---|---|
| PF-1 | 2PAC PAINTED - SUSSEX ROUTE - COLOUR MATCH TO POLYTEC AMARO - 30% SATIN |
| LAM-1 | POLYTEC FLORENTINE WALNUT WOODMATT |
| ST-1 | 12MM ENVIRO SURFACES - COVE |
| DWR | BLUM LEGRABOX SOFTCLOSE DRAWER |
| ADJ | ADJUSTABLE SHELF |
| FXD | FIXED SHELF |
| LED | REBATE AND EXTRUSION ONLY |

**ALL JOINERY**

ALL CARCASSES TO BE MADE FROM 16mm HMR White - 1mm Edge

ALL ADJ SHELF HOLES 5X 5MM HOLES 32MM SPACINGS

ALL DRAWERS TO BE Blum Legrabox Drawer

ALL HINGES TO BE 110° BLUM SOFTCLOSE

ALL HANDLES 160mm Kethy - B682 - Titanium

Name: Veronica & Param | Phone:

Address: 62 Florizel Street | Sheet # 11 of 16

City: Glen Iris | Date: 28/09/26

J1093 - 62 Florizel Street - Kitchen & Pantry | DRAWN MH

Fillers set Set back 20mm - Shadowline

J1093 - 62 Florizel Street - Kitchen & Pantry



| CODE | DESCRIPTION |
|---|---|
| PF-1 | 2PAC PAINTED - SUSSEX ROUTE - COLOUR MATCH TO POLYTEC AMARO - 30% SATIN |
| LAM-1 | POLYTEC FLORENTINE WALNUT WOODMATT |
| ST-1 | 12MM ENVIRO SURFACES - COVE |
| DWR | BLUM LEGRABOX SOFTCLOSE DRAWER |
| ADJ | ADJUSTABLE SHELF |
| FXD | FIXED SHELF |
| LED | REBATE AND EXTRUSION ONLY |

**ALL JOINERY**

ALL CARCASSES TO BE MADE FROM 16mm HMR White - 1mm Edge

ALL ADJ SHELF HOLES 5X 5MM HOLES 32MM SPACINGS

ALL DRAWERS TO BE Blum Legrabox Drawer

ALL HINGES TO BE 110° BLUM SOFTCLOSE

ALL HANDLES 160mm Kethy - B682 - Titanium

CN FITOUTS PTY LTD
CUSTOM MADE JOINERY

P 03 9761 6994
E info@cnfitouts.com.au
www.cnfitouts.com.au

6 Stephenson rd.
Bayswater North 3153

Name: Veronica & Param | Phone:

Address: 62 Florizel Street | Sheet #12 of 16

City: Glen Iris | Date: 28/09/26

J1093 - 62 Florizel Street - Kitchen & Pantry | DRAWN MH

Fillers set Set back 20mm - Shadowline

J1093 - 62 Florizel Street - Kitchen & Pantry




CN FITOUTS PTY LTD
CUSTOM MADE JOINERY

P 03 9761 6994
E info@cnfitouts.com.au
www.cnfitouts.com.au

6 Stephenson rd.
Bayswater North 3153


| CODE | DESCRIPTION |
|---|---|
| PF-1 | 2PAC PAINTED - SUSSEX ROUTE - COLOUR MATCH TO POLYTEC AMARO - 30% SATIN |
| LAM-1 | POLYTEC FLORENTINE WALNUT WOODMATT |
| ST-1 | 12MM ENVIRO SURFACES - COVE |
| DWR | BLUM LEGRABOX SOFTCLOSE DRAWER |
| ADJ | ADJUSTABLE SHELF |
| FXD | FIXED SHELF |
| LED | REBATE AND EXTRUSION ONLY |

**ALL JOINERY**

ALL CARCASSES TO BE MADE FROM 16mm HMR White - 1mm Edge

ALL ADJ SHELF HOLES 5X 5MM HOLES 32MM SPACINGS

ALL DRAWERS TO BE Blum Legrabox Drawer

ALL HINGES TO BE 110° BLUM SOFTCLOSE

ALL HANDLES 160mm Kethy - B682 - Titanium

Name: Veronica & Param

Phone:

Address: 62 Florizel Street

Sheet #13 of 16

City: Glen Iris


Date: 28/09/26

J1093 - 62 Florizel Street - Kitchen & Pantry

DRAWN MH

# Fillers set Set back 20mm - Shadowline

J1093 - 62 Florizel Street - Kitchen & Pantry

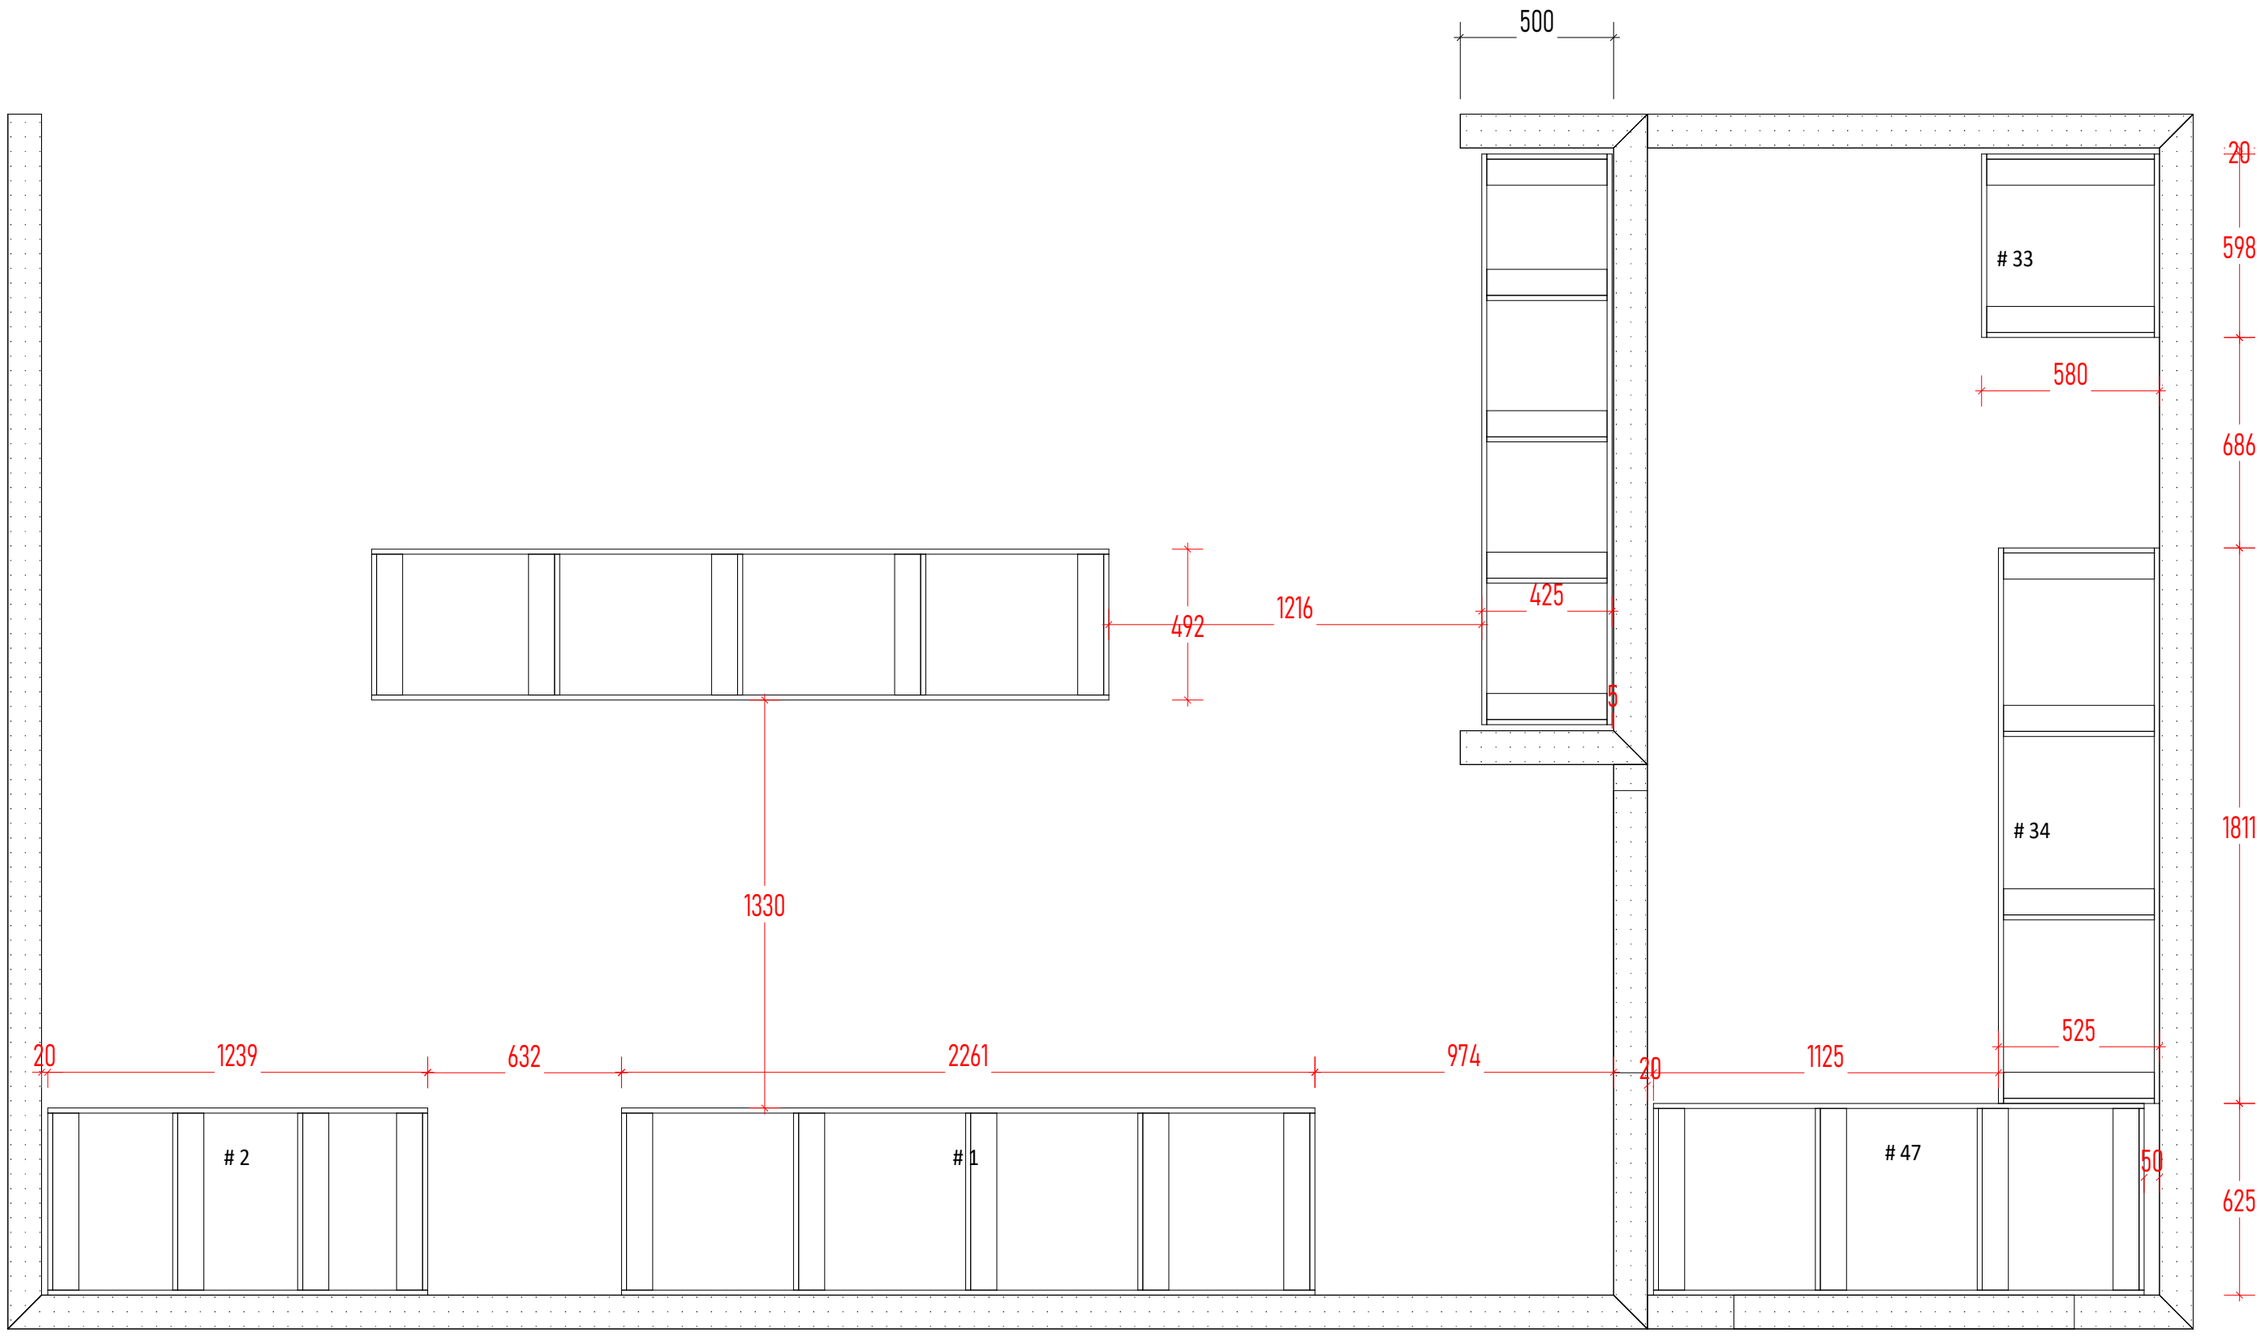



CN FITOUTS PTY LTD
CUSTOM MADE JOINERY

P 03 9761 6994
E info@cnfitouts.com.au
www.cnfitouts.com.au

6 Stephenson rd.
Bayswater North 3153


| CODE | DESCRIPTION |
|---|---|
| PF-1 | 2PAC PAINTED - SUSSEX ROUTE - COLOUR MATCH TO POLYTEC AMARO - 30% SATIN |
| LAM-1 | POLYTEC FLORENTINE WALNUT WOODMATT |
| ST-1 | 12MM ENVIRO SURFACES - COVE |
| DWR | BLUM LEGRABOX SOFTCLOSE DRAWER |
| ADJ | ADJUSTABLE SHELF |
| FXD | FIXED SHELF |
| LED | REBATE AND EXTRUSION ONLY |

**ALL JOINERY**

ALL CARCASSES TO BE MADE FROM 16mm HMR White - 1mm Edge

ALL ADJ SHELF HOLES 5X 5MM HOLES 32MM SPACINGS

ALL DRAWERS TO BE Blum Legrabox Drawer

ALL HINGES TO BE 110° BLUM SOFTCLOSE

ALL HANDLES 160mm Kethy - B682 - Titanium

Name: Veronica & Param

Phone:

Address: 62 Florizel Street

City: Glen Iris

Sheet # 14 of 16


Date: 28/09/26

J1093 - 62 Florizel Street - Kitchen & Pantry

DRAWN MH


# Fillers set Set back 20mm - Shadowline

J1093 - 62 Florizel Street - Kitchen & Pantry

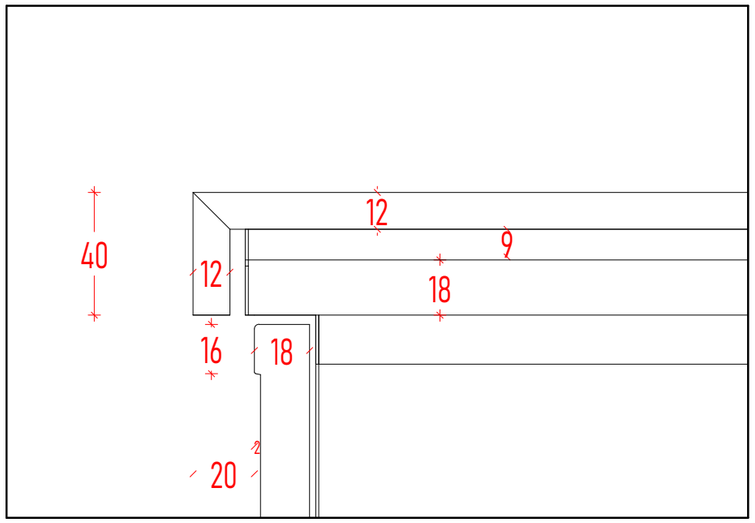



20mm O/Hang Benchtop Detail


Scale: 1 : 2

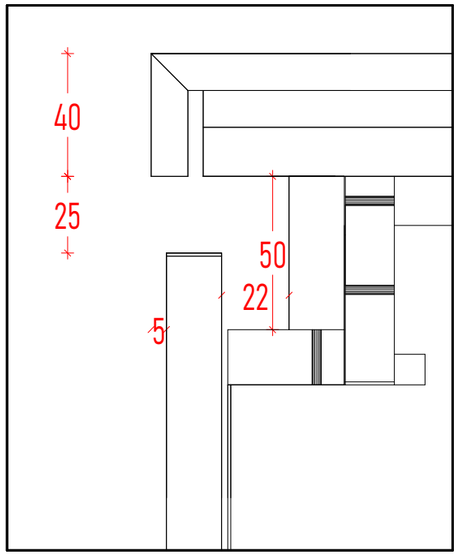


## L SHAPE RAIL DETAIL

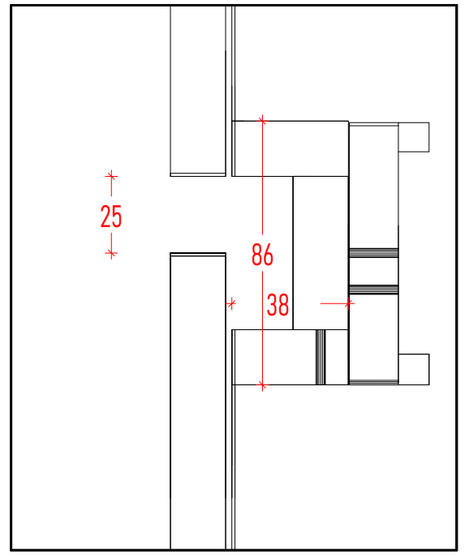



## C SHAPE RAIL DETAIL

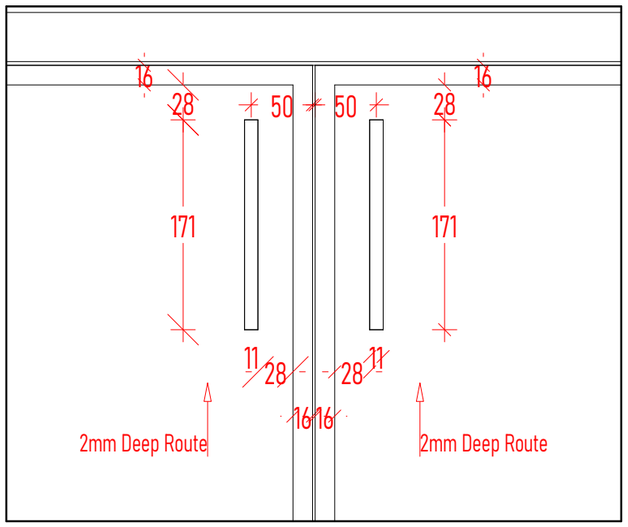


Typical Door Detail

Scale: 1 : 5

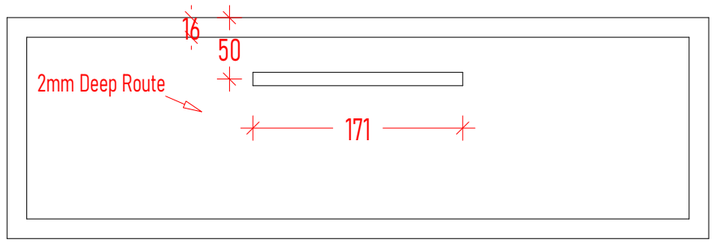


Typical Drawer Detail

Scale: 1 : 5

Fingerpull Benchtop Detail

Scale: 1 : 2


CN FITOUTS PTY LTD
CUSTOM MADE JOINERY

P 03 9761 6994
E info@cnfitouts.com.au
www.cnfitouts.com.au

6 Stephenson rd.
Bayswater North 3153


| CODE | DESCRIPTION |
|---|---|
| PF-1 | 2PAC PAINTED - SUSSEX ROUTE - COLOUR MATCH TO POLYTEC AMARO - 30% SATIN |
| LAM-1 | POLYTEC FLORENTINE WALNUT WOODMATT |
| ST-1 | 12MM ENVIRO SURFACES - COVE |
| DWR | BLUM LEGRABOX SOFTCLOSE DRAWER |
| ADJ | ADJUSTABLE SHELF |
| FXD | FIXED SHELF |
| LED | REBATE AND EXTRUSION ONLY |

**ALL JOINERY**

ALL CARCASSES TO BE MADE FROM 16mm HMR White - 1mm Edge

ALL ADJ SHELF HOLES 5X 5MM HOLES 32MM SPACINGS

ALL DRAWERS TO BE Blum Legrabox Drawer

ALL HINGES TO BE 110° BLUM SOFTCLOSE

ALL HANDLES 160mm Kethy - B682 - Titanium

Name: Veronica & Param | Phone:


Address: 62 Florizel Street | Sheet # 15 of 16

City: Glen Iris | Date: 28/09/26

J1093 - 62 Florizel Street - Kitchen & Pantry | DRAWN MH

# Fillers set Set back 20mm - Shadowline

J1093 - 62 Florizel Street - Kitchen & Pantry

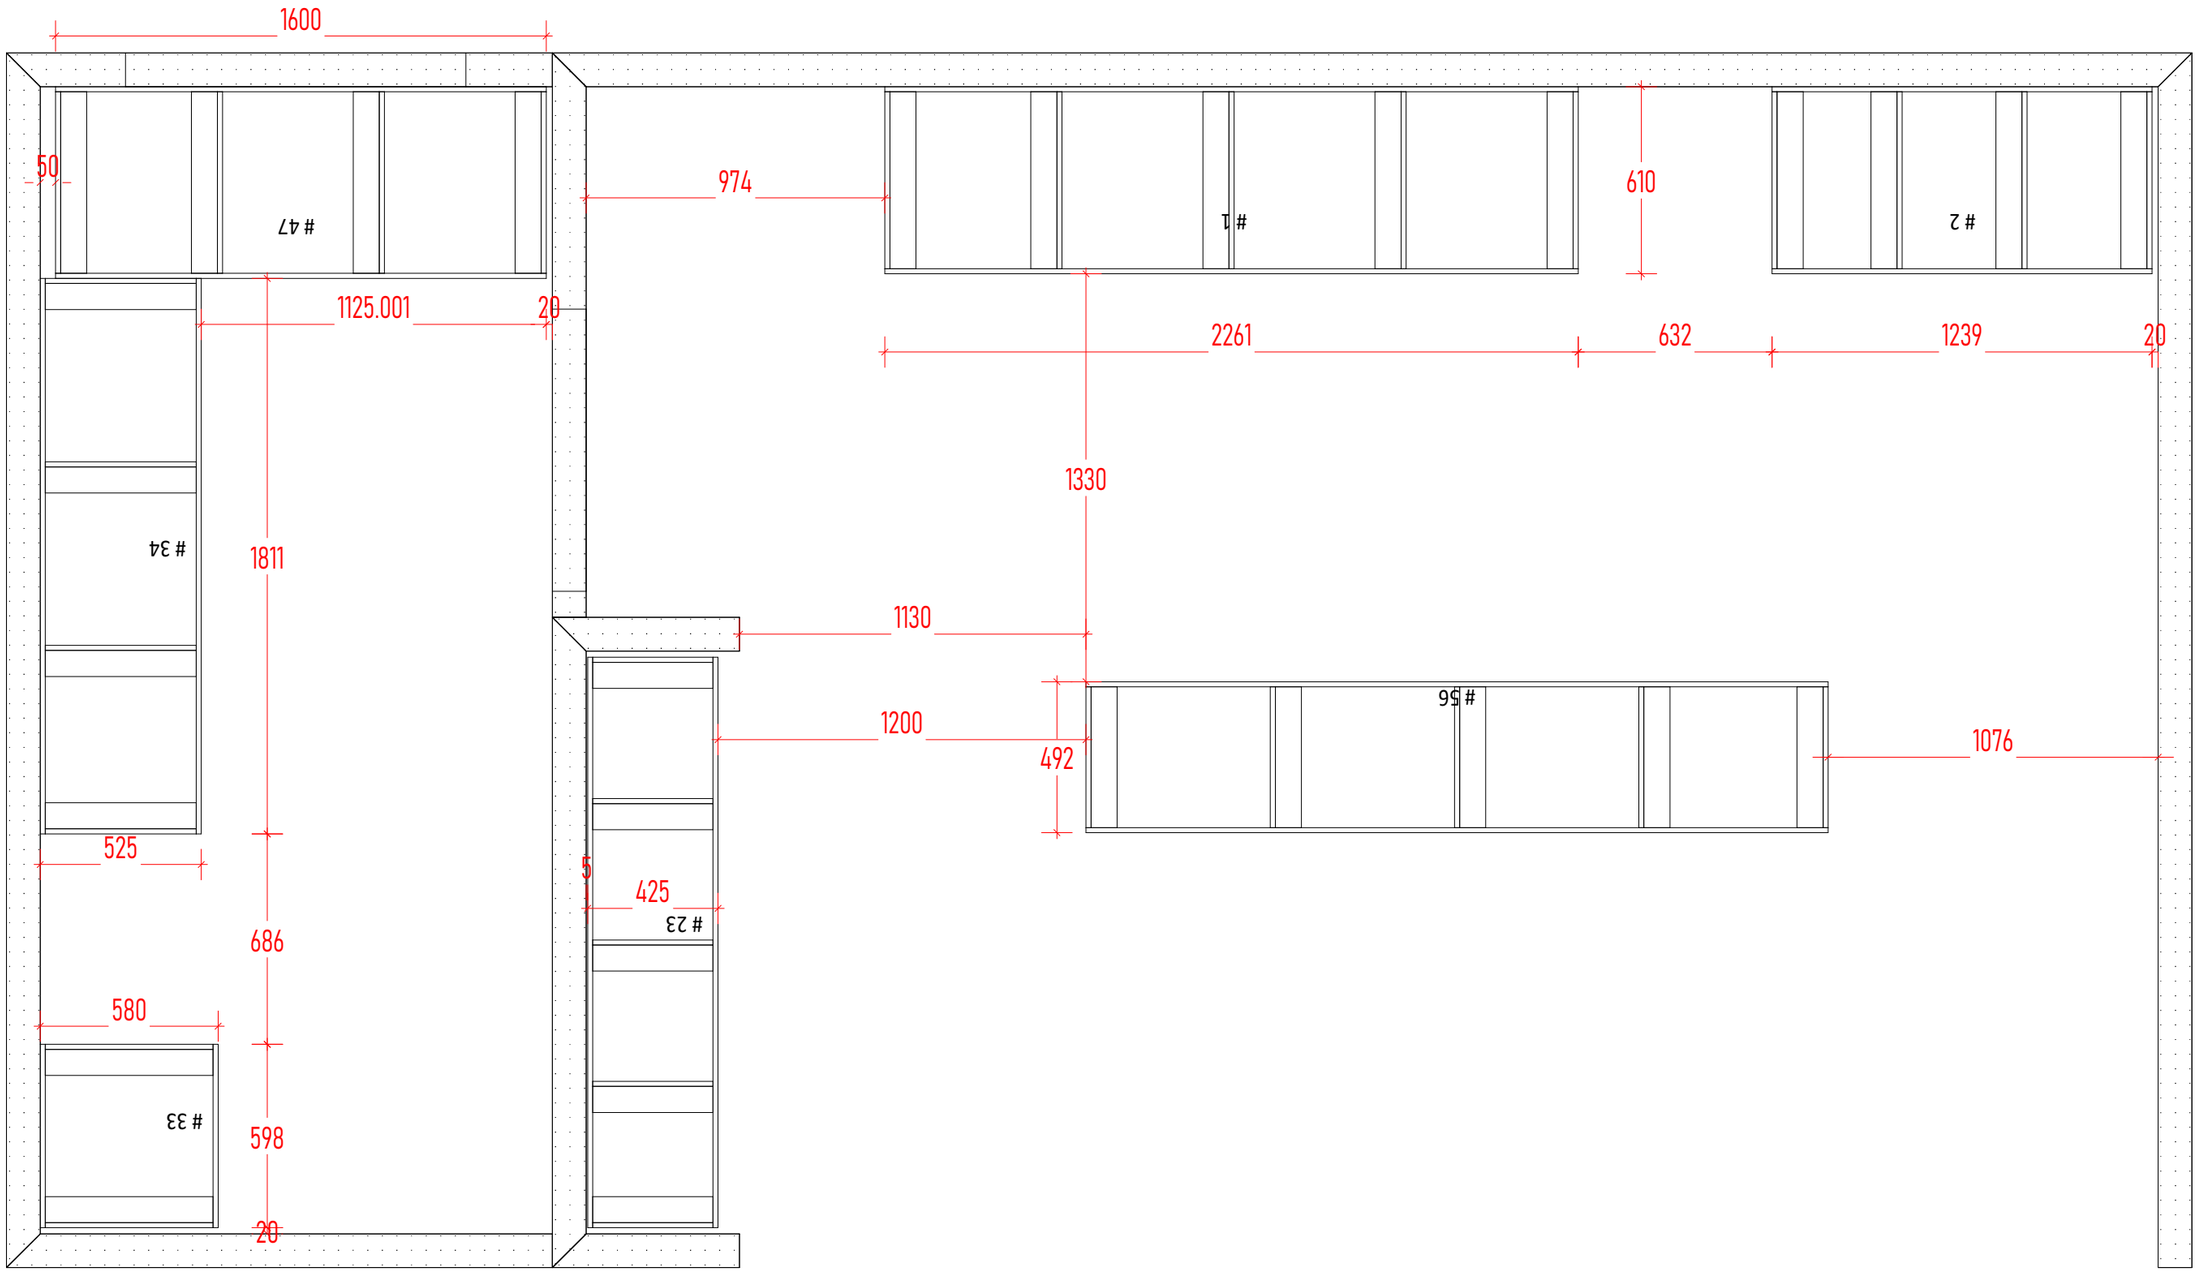



P 03 9761 6994
E info@cnfitouts.com.au
www.cnfitouts.com.au

6 Stephenson rd.
Bayswater North 3153


| CODE | DESCRIPTION |
|---|---|
| PF-1 | 2PAC PAINTED - SUSSEX ROUTE - COLOUR MATCH TO POLYTEC AMARO - 30% SATIN |
| LAM-1 | POLYTEC FLORENTINE WALNUT WOODMATT |
| ST-1 | 12MM ENVIRO SURFACES - COVE |
| DWR | BLUM LEGRABOX SOFTCLOSE DRAWER |
| ADJ | ADJUSTABLE SHELF |
| FXD | FIXED SHELF |
| LED | REBATE AND EXTRUSION ONLY |

**ALL JOINERY**

ALL CARCASSES TO BE MADE FROM 16mm HMR White - 1mm Edge

ALL ADJ SHELF HOLES 5X 5MM HOLES 32MM SPACINGS

ALL DRAWERS TO BE Blum Legrabox Drawer

ALL HINGES TO BE 110° BLUM SOFTCLOSE

ALL HANDLES 160mm Kethy - B682 - Titanium

Name: Veronica & Param

Phone:

Address: 62 Florizel Street

Sheet #16 of 16

City: Glen Iris

Date: 28/09/26

J1093 - 62 Florizel Street - Kitchen & Pantry

DRAWN MH