
Fillers set flush with doors

J974 - Cathy & John Bain

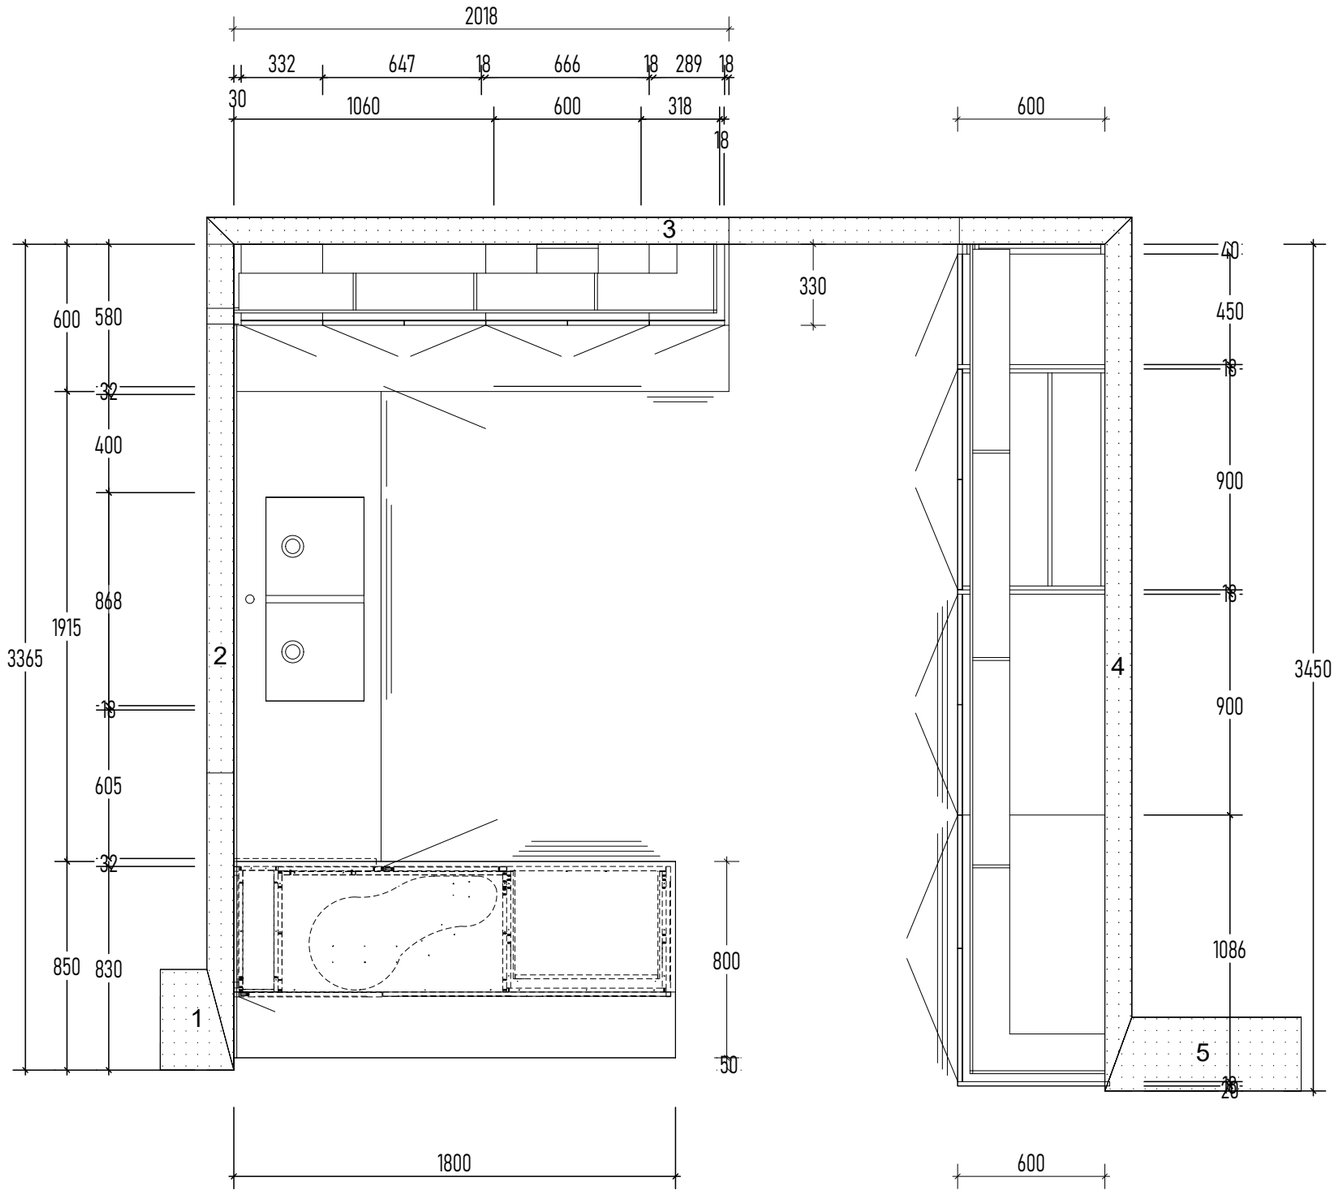


Kitchen Plan

Scale: 1 : 25

CN FITOUTS PTY LTD
CUSTOM MADE JOINERY

P 03 9761 6994
E info@cnfitouts.com.au
www.cnfitouts.com.au

6 Stephenson rd.
Bayswater North 3153

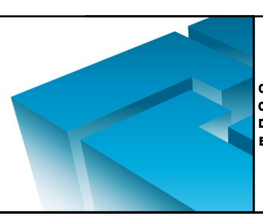

CODE	DESCRIPTION
PF-1	2PAC PAINTED SHAKER 45 DOORS - 3MM DEEP ROUTE - DULUX NATURAL WHITE SATIN 30%
ST-1	40MM STONE BENCHTOP W MITRED EDGE - Venatino Statuario
DWR	BLUM LEGRABOX SOFTCLOSE DRAWER
ADJ	ADJUSTABLE SHELF
FXD	FIXED SHELF

ALL JOINERY

ALL CARCASSES TO BE MADE FROM 16mm HMR White - 1mm Edge

ALL ADJ SHELF HOLES 5X 5MM HOLES 32MM SPACINGS

ALL DRAWERS TO BE Blum Legrabox Drawer


ALL HINGES TO BE 110° BLUM SOFTCLOSE

ALL HANDLES 160mm x 8mm Livorno - Brushed Stainless

Name: 10 Morris Rd	Phone:
Address:	Sheet # 1 of 9
City: Upper Beaconsfield	Date: 18/09/26
J974 - Cathy & John Bain	DRAWN MH


Fillers set flush with doors

J974 - Cathy & John Bain

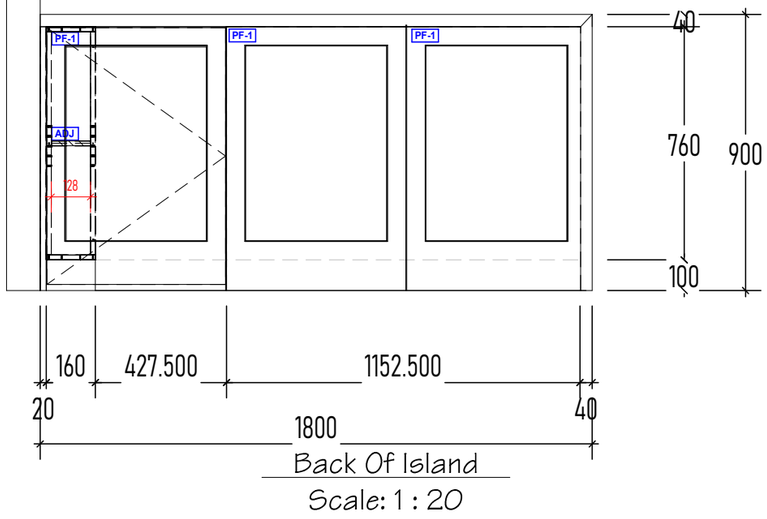


Back Of Island

Scale: 1 : 20

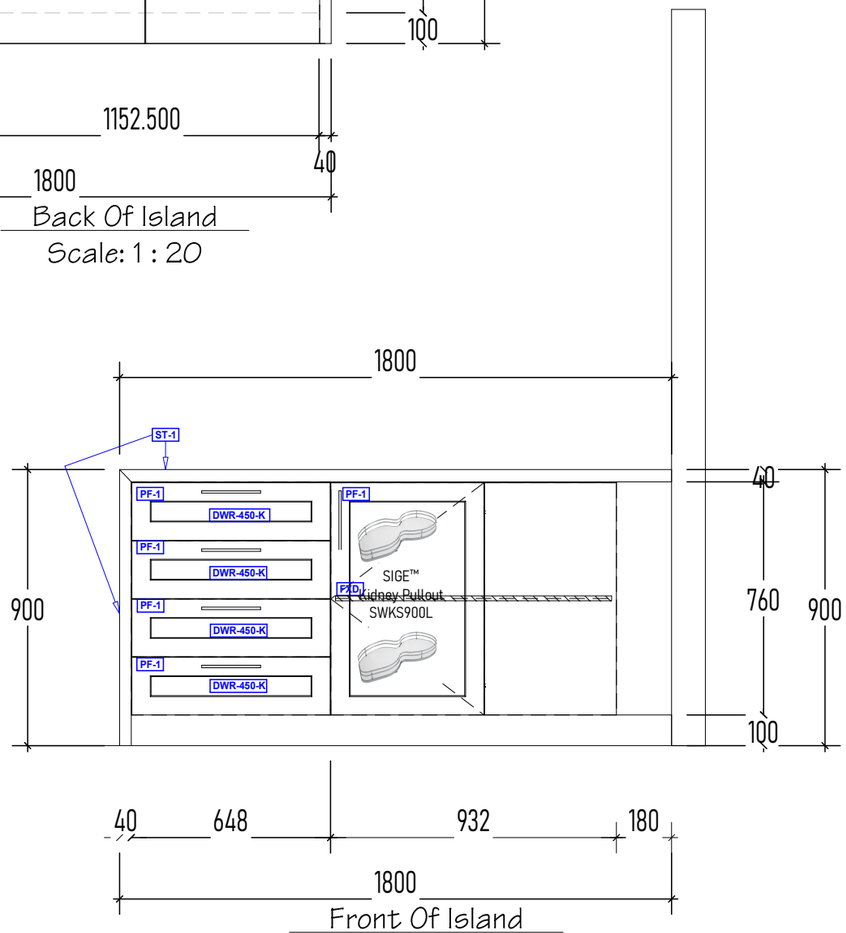

Front Of Island

Scale: 1 : 20

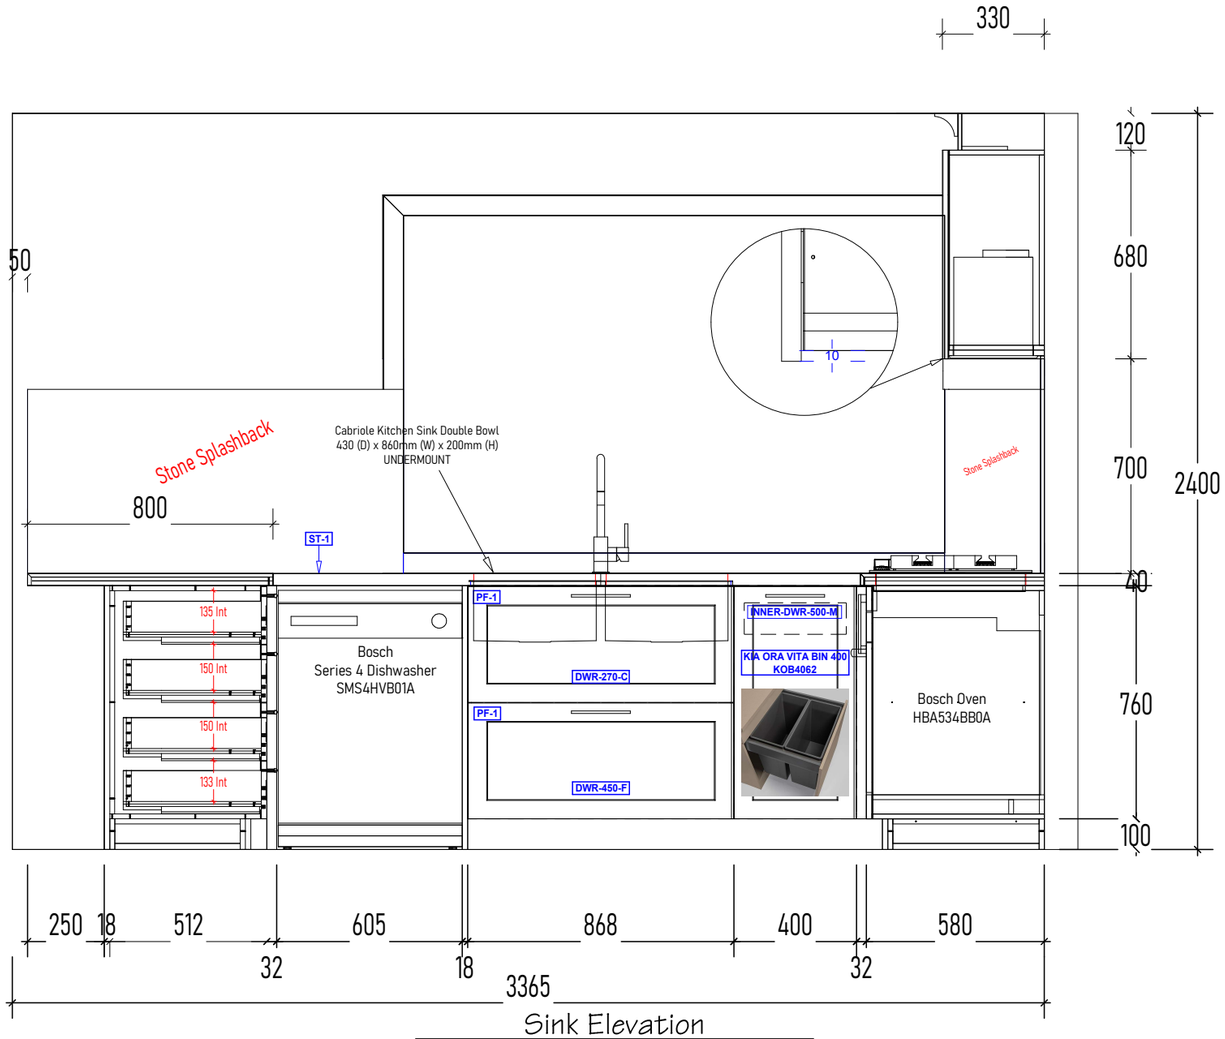

Sink Elevation

Scale: 1 : 20

CN FITOUTS PTY LTD
CUSTOM MADE JOINERY

P 03 9761 6994
E info@cnfitouts.com.au
www.cnfitouts.com.au

6 Stephenson rd.
Bayswater North 3153

CODE	DESCRIPTION
PF-1	2PAC PAINTED SHAKER 45 DOORS - 3MM DEEP ROUTE - DULUX NATURAL WHITE SATIN 30%
ST-1	40MM STONE BENCHTOP W MITRED EDGE - Venatino Statuario
DWR	BLUM LEGRABOX SOFTCLOSE DRAWER
ADJ	ADJUSTABLE SHELF
FXD	FIXED SHELF

ALL JOINERY

ALL CARCASSES TO BE MADE FROM 16mm HMR White - 1mm Edge

ALL ADJ SHELF HOLES 5X 5MM HOLES 32MM SPACINGS

ALL DRAWERS TO BE Blum Legrabox Drawer


ALL HINGES TO BE 110° BLUM SOFTCLOSE

ALL HANDLES 160mm x 8mm Livorno - Brushed Stainless

Name: 10 Morris Rd	Phone:
Address:	Sheet # 2 of 9
City: Upper Beaconsfield	Date: 18/09/26
J974 - Cathy & John Bain	DRAWN MH

Fillers set flush with doors

J974 - Cathy & John Bain

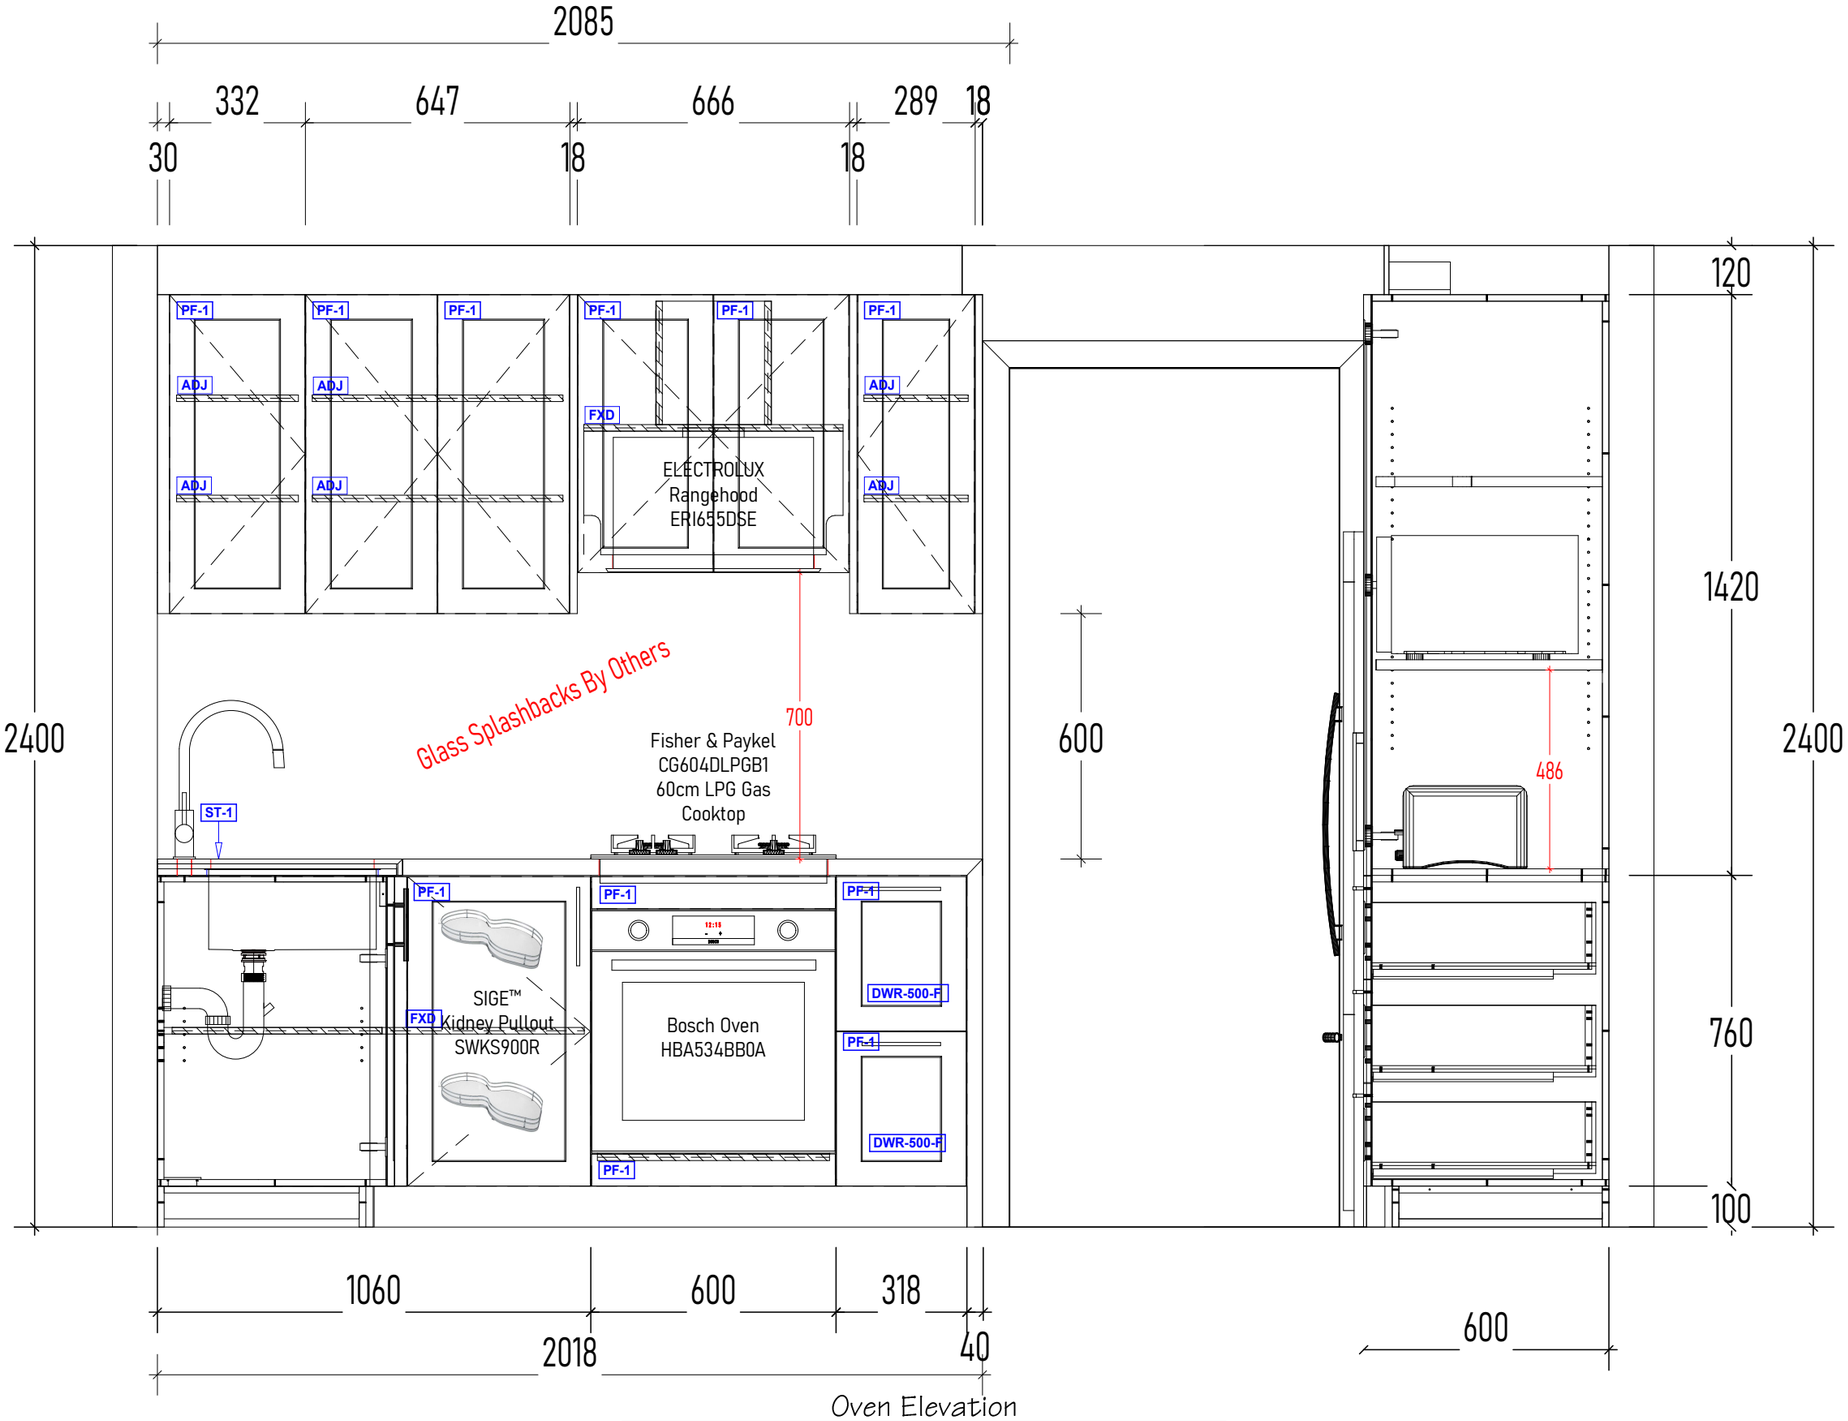

Oven Elevation

Scale: 1 : 15

CN FITOUTS PTY LTD
CUSTOM MADE JOINERY

P 03 9761 6994
E info@cnfitouts.com.au
www.cnfitouts.com.au

6 Stephenson rd.
Bayswater North 3153

CODE	DESCRIPTION
PF-1	2PAC PAINTED SHAKER 45 DOORS - 3MM DEEP ROUTE - DULUX NATURAL WHITE SATIN 30%
ST-1	40MM STONE BENCHTOP W MITRED EDGE - Venatino Statuario
DWR	BLUM LEGRABOX SOFTCLOSE DRAWER
ADJ	ADJUSTABLE SHELF
FXD	FIXED SHELF

ALL JOINERY

ALL CARCASSES TO BE MADE FROM 16mm HMR White - 1mm Edge

ALL ADJ SHELF HOLES 5X 5MM HOLES 32MM SPACINGS

ALL DRAWERS TO BE Blum Legrabox Drawer

ALL HINGES TO BE 110° BLUM SOFTCLOSE


ALL HANDLES 160mm x 8mm Livorno - Brushed Stainless

Name: 10 Morris Rd	Phone:
Address:	Sheet # 3 of 9
City: Upper Beaconsfield	Date: 18/09/26
J974 - Cathy & John Bain	DRAWN MH

Fillers set flush with doors

J974 - Cathy & John Bain



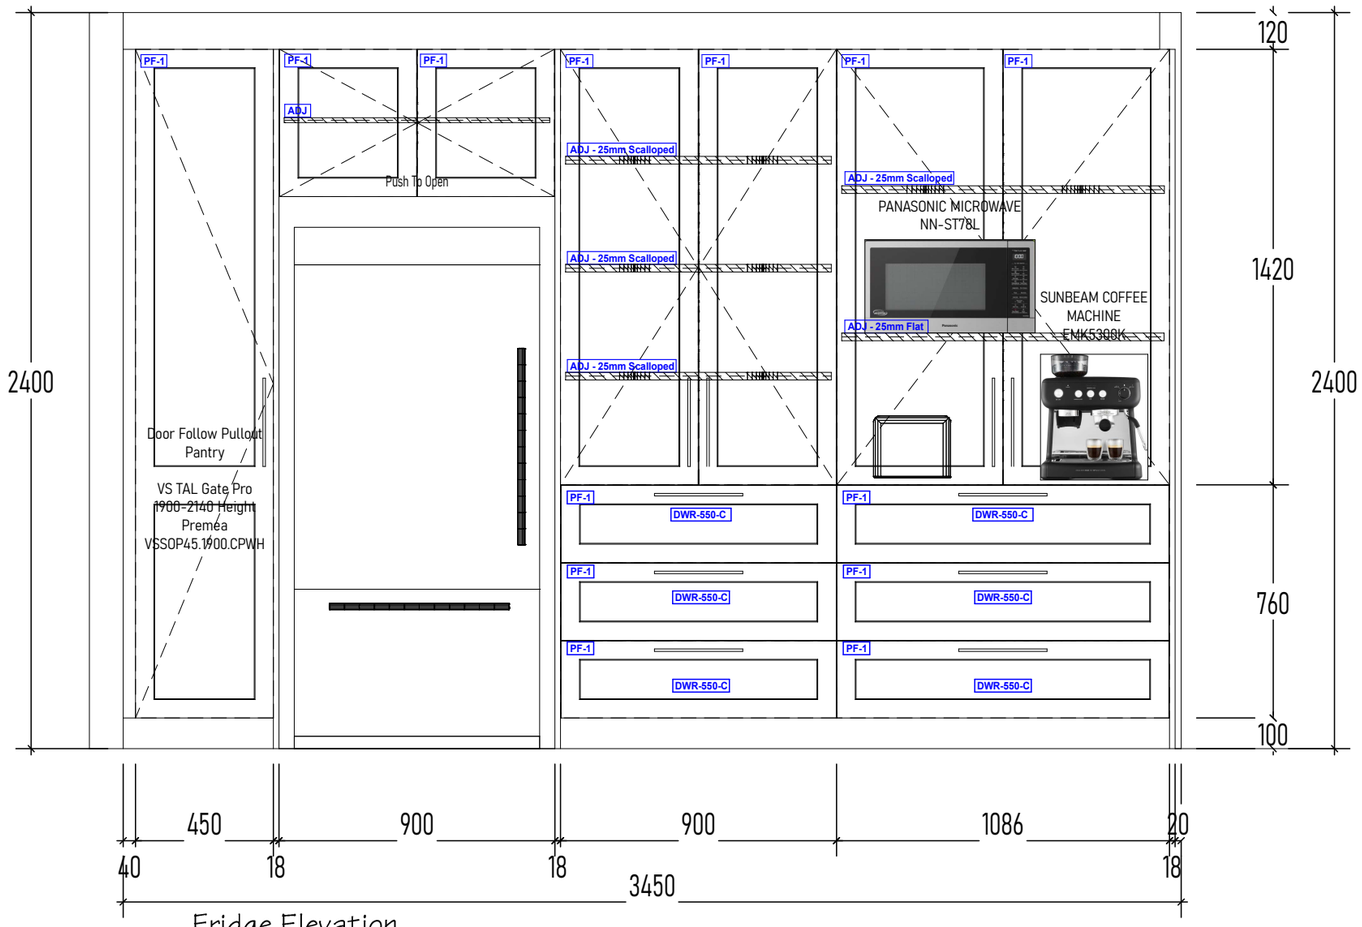

Fridge Elevation

Scale: 1 : 20

CN FITOUTS PTY LTD
CUSTOM MADE JOINERY

P 03 9761 6994
E info@cnfitouts.com.au
www.cnfitouts.com.au

6 Stephenson rd.
Bayswater North 3153

CODE	DESCRIPTION
PF-1	2PAC PAINTED SHAKER 45 DOORS - 3MM DEEP ROUTE - DULUX NATURAL WHITE SATIN 30%
ST-1	40MM STONE BENCHTOP W MITRED EDGE - Venatino Statuario
DWR	BLUM LEGRABOX SOFTCLOSE DRAWER
ADJ	ADJUSTABLE SHELF
FXD	FIXED SHELF

ALL JOINERY

ALL CARCASSES TO BE MADE FROM 16mm HMR White - 1mm Edge

ALL ADJ SHELF HOLES 5X 5MM HOLES 32MM SPACINGS

ALL DRAWERS TO BE Blum Legrabox Drawer

ALL HINGES TO BE 110° BLUM SOFTCLOSE

ALL HANDLES 160mm x 8mm Livorno - Brushed Stainless

Name: 10 Morris Rd	Phone:
Address:	Sheet # 4 of 9
City: Upper Beaconsfield	Date: 18/09/26
J974 - Cathy & John Bain	DRAWN MH

Fillers set flush with doors

J974 - Cathy & John Bain



CN FITOUTS PTY LTD
CUSTOM MADE JOINERY

P 03 9761 6994
E info@cnfitouts.com.au
www.cnfitouts.com.au

6 Stephenson rd.
Bayswater North 3153

CODE	DESCRIPTION
PF-1	2PAC PAINTED SHAKER 45 DOORS - 3MM DEEP ROUTE - DULUX NATURAL WHITE SATIN 30%
ST-1	40MM STONE BENCHTOP W MITRED EDGE - Venatino Statuario
DWR	BLUM LEGRABOX SOFTCLOSE DRAWER
ADJ	ADJUSTABLE SHELF
FXD	FIXED SHELF

ALL JOINERY

ALL CARCASSES TO BE MADE FROM 16mm HMR White - 1mm Edge

ALL ADJ SHELF HOLES 5X 5MM HOLES 32MM SPACINGS

ALL DRAWERS TO BE Blum Legrabox Drawer

ALL HINGES TO BE 110° BLUM SOFTCLOSE

ALL HANDLES 160mm x 8mm Livorno - Brushed Stainless

Name: 10 Morris Rd

Phone:

Address:

City: Upper Beaconsfield

Sheet # 5 of 9

Date: 18/09/26

J974 - Cathy & John Bain

DRAWN MH

Fillers set flush with doors

J974 - Cathy & John Bain



CN FITOUTS PTY LTD
CUSTOM MADE JOINERY

P 03 9761 6994
E info@cnfitouts.com.au
www.cnfitouts.com.au

6 Stephenson rd.
Bayswater North 3153

CODE	DESCRIPTION
PF-1	2PAC PAINTED SHAKER 45 DOORS - 3MM DEEP ROUTE - DULUX NATURAL WHITE SATIN 30%
ST-1	40MM STONE BENCHTOP W MITRED EDGE - Venatino Statuario
DWR	BLUM LEGRABOX SOFTCLOSE DRAWER
ADJ	ADJUSTABLE SHELF
FXD	FIXED SHELF

ALL JOINERY

ALL CARCASSES TO BE MADE FROM 16mm HMR White - 1mm Edge

ALL ADJ SHELF HOLES 5X 5MM HOLES 32MM SPACINGS

ALL DRAWERS TO BE Blum Legrabox Drawer

ALL HINGES TO BE 110° BLUM SOFTCLOSE

ALL HANDLES 160mm x 8mm Livorno - Brushed Stainless

Name: 10 Morris Rd

Phone:

Address:

Sheet # 6 of 9

City: Upper Beaconsfield

Date: 18/09/26

J974 - Cathy & John Bain

DRAWN MH

Fillers set flush with doors

J974 - Cathy & John Bain



CN FITOUTS PTY LTD
CUSTOM MADE JOINERY

P 03 9761 6994
E info@cnfitouts.com.au
www.cnfitouts.com.au

6 Stephenson rd.
Bayswater North 3153

CODE	DESCRIPTION
PF-1	2PAC PAINTED SHAKER 45 DOORS - 3MM DEEP ROUTE - DULUX NATURAL WHITE SATIN 30%
ST-1	40MM STONE BENCHTOP W MITRED EDGE - Venatino Statuario
DWR	BLUM LEGRABOX SOFTCLOSE DRAWER
ADJ	ADJUSTABLE SHELF
FXD	FIXED SHELF

ALL JOINERY

ALL CARCASSES TO BE MADE FROM 16mm HMR White - 1mm Edge

ALL ADJ SHELF HOLES 5X 5MM HOLES 32MM SPACINGS

ALL DRAWERS TO BE Blum Legrabox Drawer

ALL HINGES TO BE 110° BLUM SOFTCLOSE

ALL HANDLES 160mm x 8mm Livorno - Brushed Stainless

Name: 10 Morris Rd

Phone:

Address:

Sheet # 7 of 9

City: Upper Beaconsfield

Date: 18/09/26

J974 - Cathy & John Bain

DRAWN MH

Fillers set flush with doors

J974 - Cathy & John Bain



CN FITOUTS PTY LTD
CUSTOM MADE JOINERY

P 03 9761 6994
E info@cnfitouts.com.au
www.cnfitouts.com.au

6 Stephenson rd.
Bayswater North 3153

CODE	DESCRIPTION
PF-1	2PAC PAINTED SHAKER 45 DOORS - 3MM DEEP ROUTE - DULUX NATURAL WHITE SATIN 30%
ST-1	40MM STONE BENCHTOP W MITRED EDGE - Venatino Statuario
DWR	BLUM LEGRABOX SOFTCLOSE DRAWER
ADJ	ADJUSTABLE SHELF
FXD	FIXED SHELF

ALL JOINERY

ALL CARCASSES TO BE MADE FROM 16mm HMR White - 1mm Edge

ALL ADJ SHELF HOLES 5X 5MM HOLES 32MM SPACINGS

ALL DRAWERS TO BE Blum Legrabox Drawer

ALL HINGES TO BE 110° BLUM SOFTCLOSE

ALL HANDLES 160mm x 8mm Livorno - Brushed Stainless

Name: 10 Morris Rd	Phone:
Address:	Sheet # 8 of 9
City: Upper Beaconsfield	Date: 18/09/26
J974 - Cathy & John Bain	DRAWN MH

Fillers set flush with doors

J974 - Cathy & John Bain





CN FITOUTS PTY LTD
CUSTOM MADE JOINERY

P 03 9761 6994
E info@cnfitouts.com.au
www.cnfitouts.com.au

6 Stephenson rd.
Bayswater North 3153

CODE	DESCRIPTION
PF-1	2PAC PAINTED SHAKER 45 DOORS - 3MM DEEP ROUTE - DULUX NATURAL WHITE SATIN 30%
ST-1	40MM STONE BENCHTOP W MITRED EDGE - Venatino Statuario
DWR	BLUM LEGRABOX SOFTCLOSE DRAWER
ADJ	ADJUSTABLE SHELF
FXD	FIXED SHELF

ALL JOINERY

ALL CARCASSES TO BE MADE FROM 16mm HMR White - 1mm Edge

ALL ADJ SHELF HOLES 5X 5MM HOLES 32MM SPACINGS

ALL DRAWERS TO BE Blum Legrabox Drawer

ALL HINGES TO BE 110° BLUM SOFTCLOSE

ALL HANDLES 160mm x 8mm Livorno - Brushed Stainless

Name: 10 Morris Rd

Phone:

Address:

Sheet # 9 of 9

City: Upper Beaconsfield

Date: 18/09/26

J974 - Cathy & John Bain

DRAWN MH