

Approved CN Drawings Supersede All Other Drawings and Specs

CODE	DESCRIPTION
HN01	32mm Touch Handles Circ Semi Circle Pull 'Dull Brushed Nickel CIRC32.DBR'
HN02	192mm Touch Handles OVA Semi Oval Pull Handle 'Dull Brushed Nickel, OVA192.DBR'
HN03	40mm Touch Handles Veda Knob 'Brushed Nickel V35.40.BRN'
PT01	18mm 2Pac Dulux White Beach Quarter Satin - Sussex Profile
PT03	18mm 2Pac to match Polytec Topiary
ST01	20mm Caesarstone '5031 Statuario Maximus'
TM01	18mm George Fethers Veneer w/ 2Pac ' Blok, LOB 67.03'

Name: A and D Building

Address:
9 Moorehouse St
Camberwell

Sheet # 15 of 22

Date: 21/10/26

Drawn By: AF

JOB STANDARD MATERIALS

UNLESS STATED OTHERWISE
INTERNAL CARCASSES TO BE:
* 16mm White - 1mm
ALL ADJ SHELF HOLES 5X 5MM HOLES 32MM SPACINGS
ALL DRAWERS TO BE *Blum Legrabox Drawer
ALL HINGES TO BE 110* BLUM SOFTCLOSE


CN FITOUTS PTY LTD
CUSTOM MADE JOINERY


P 03 9761 6994
E info@cnfitouts.com.au
www.cnfitouts.com.au

6 Stephenson rd.
Bayswater North 3153


Dining Plans

J1022 Moorehouse

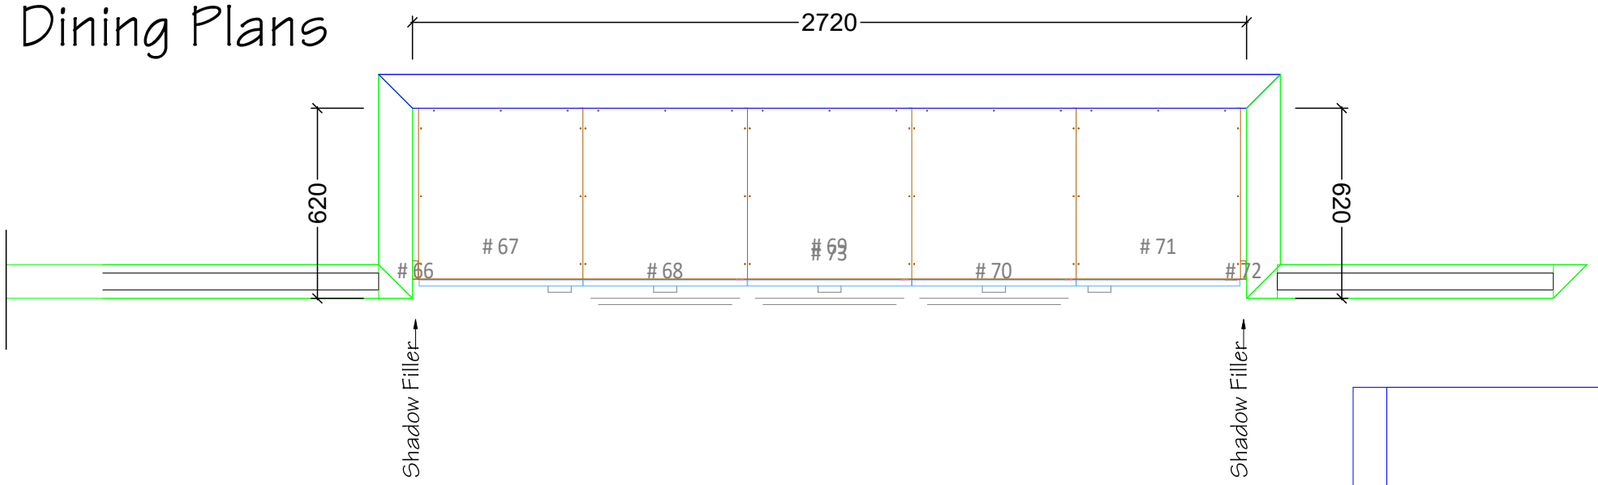


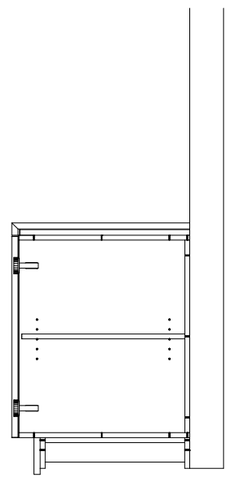

Q/3 Section - Dining
Scale: 1:20

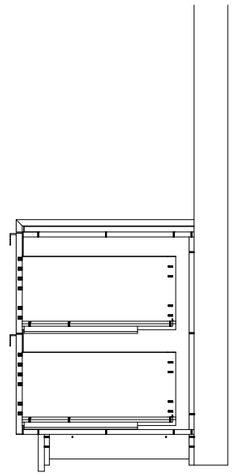

R/3 Section - Dining
Scale: 1:20

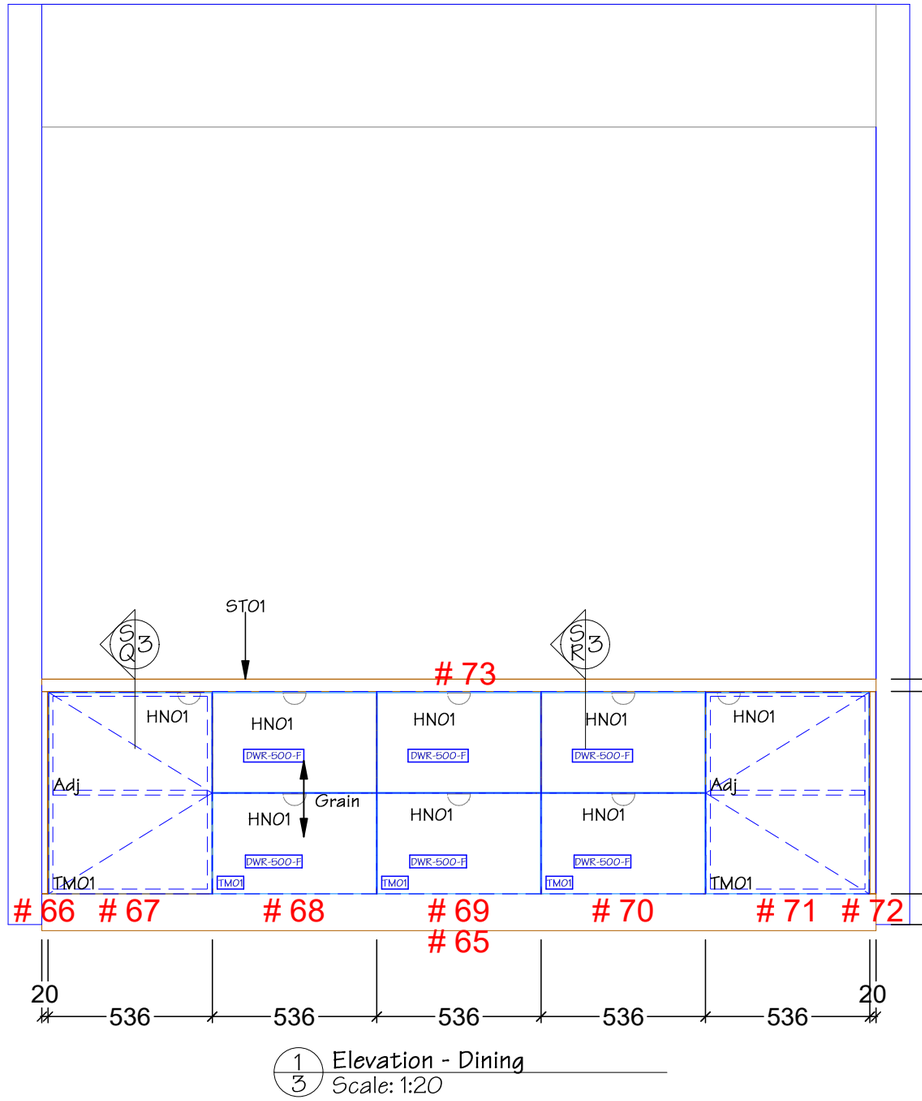

1/3 Elevation - Dining
Scale: 1:20

Approved CN Drawings Supersede All Other Drawings and Specs

CODE	DESCRIPTION
HNO1	32mm Touch Handles Circ Semi Circle Pull 'Dull Brushed Nickel CIRC32.DBR'
HNO2	192mm Touch Handles OVA Semi Oval Pull Handle 'Dull Brushed Nickel, OVA192.DBR'
HNO3	40mm Touch Handles Veda Knob 'Brushed Nickel V35.40.BRN'
PT01	18mm 2Pac Dulux White Beach Quarter Satin - Sussex Profile
PT03	18mm 2Pac to match Polytec Topiary
ST01	20mm Caesarstone '5031 Statuario Maximus'
TM01	18mm George Fethers Veneer w/ 2Pac ' Blok, LOB 67.03'

Name: A and D Building

Address:

9 Moorehouse St

Camberwell

Sheet # 16 of 22

Date: 21/10/26

Drawn By: AF

JOB STANDARD MATERIALS

UNLESS STATED OTHERWISE
INTERNAL CARCASSES TO BE:
* 16mm White - 1mm
ALL ADJ SHELF HOLES 5X 5MM HOLES 32MM SPACINGS
ALL DRAWERS TO BE *Blum Legrabox Drawer
ALL HINGES TO BE 110* BLUM SOFTCLOSE

CN FITOUTS PTY LTD
CUSTOM MADE JOINERY

P 03 9761 6994
E info@cnfitouts.com.au
www.cnfitouts.com.au

6 Stephenson rd.
Bayswater North 3153



Approved CN Drawings Supersede All Other Drawings and Specs

CODE	DESCRIPTION
HN01	32mm Touch Handles Circ Semi Circle Pull 'Dull Brushed Nickel CIRC32.DBR'
HN02	192mm Touch Handles OVA Semi Oval Pull Handle 'Dull Brushed Nickel, OVA192.DBR'
HN03	40mm Touch Handles Veda Knob 'Brushed Nickel V35.40.BRN'
PT01	18mm 2Pac Dulux White Beach Quarter Satin - Sussex Profile
PT03	18mm 2Pac to match Polytec Topiary
ST01	20mm Caesarstone '5031 Statuario Maximus'
TM01	18mm George Fethers Veneer w/ 2Pac ' Blok, LOB 67.03'

Name: A and D Building

Address:
9 Moorehouse St
Camberwell

Sheet # 17 of 22

Date: 21/10/26

Drawn By: AF

JOB STANDARD MATERIALS

UNLESS STATED OTHERWISE
INTERNAL CARCASSES TO BE:
* 16mm White - 1mm
ALL ADJ SHELF HOLES 5X 5MM HOLES 32MM SPACINGS
ALL DRAWERS TO BE *Blum Legrabox Drawer
ALL HINGES TO BE 110* BLUM SOFTCLOSE


CN FITOUTS PTY LTD
CUSTOM MADE JOINERY


P 03 9761 6994
E info@cnfitouts.com.au
www.cnfitouts.com.au

6 Stephenson rd.
Bayswater North 3153


Family Plans

J1022 Moorehouse

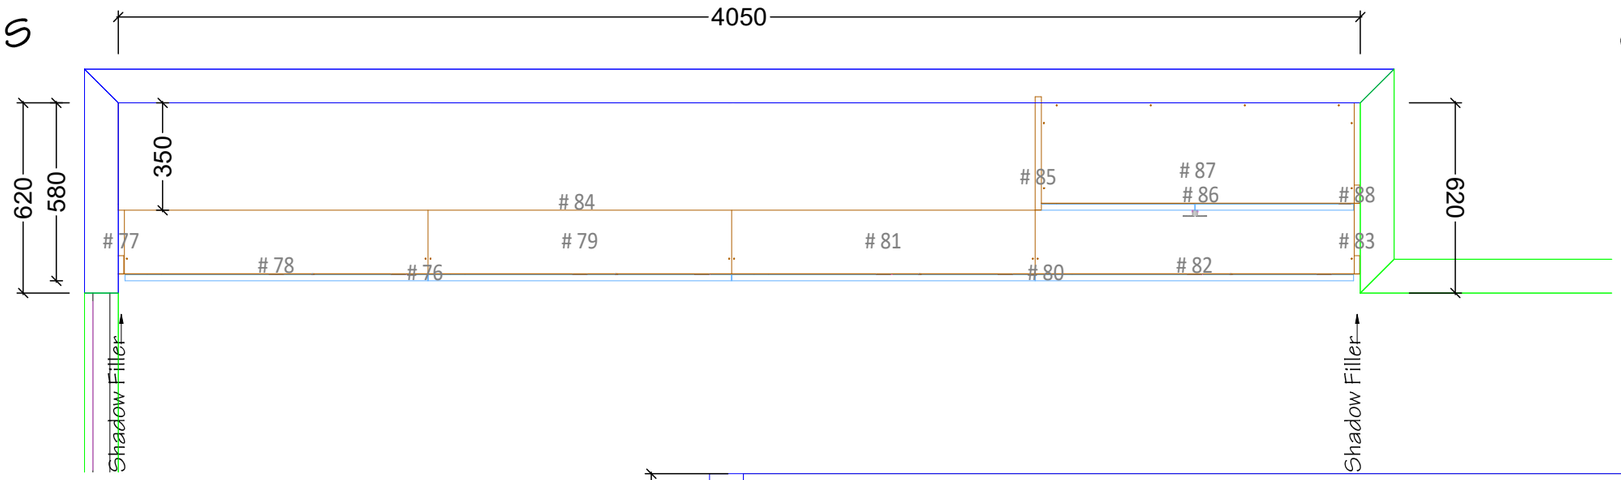


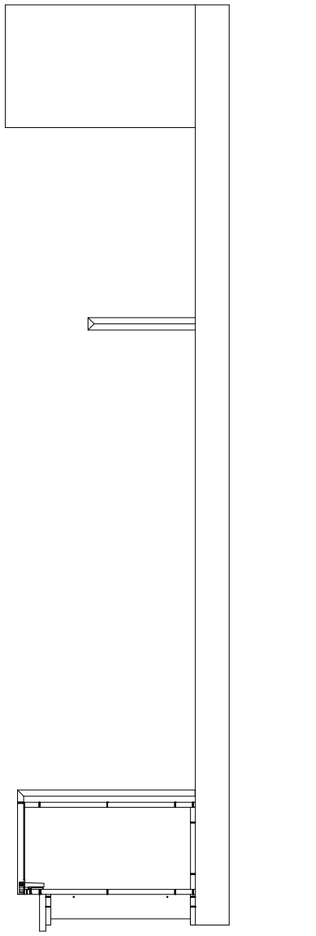

S3 Section - Family
Scale: 1:20

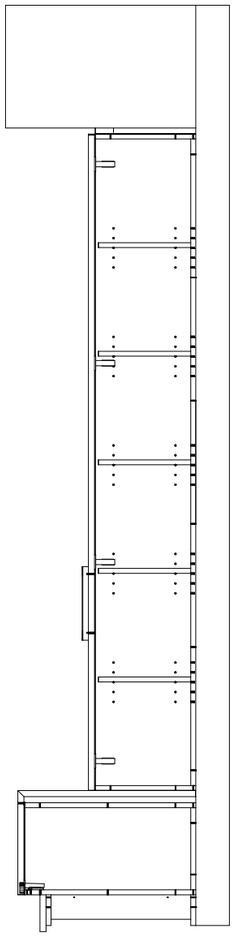

T3 Section - Family
Scale: 1:20

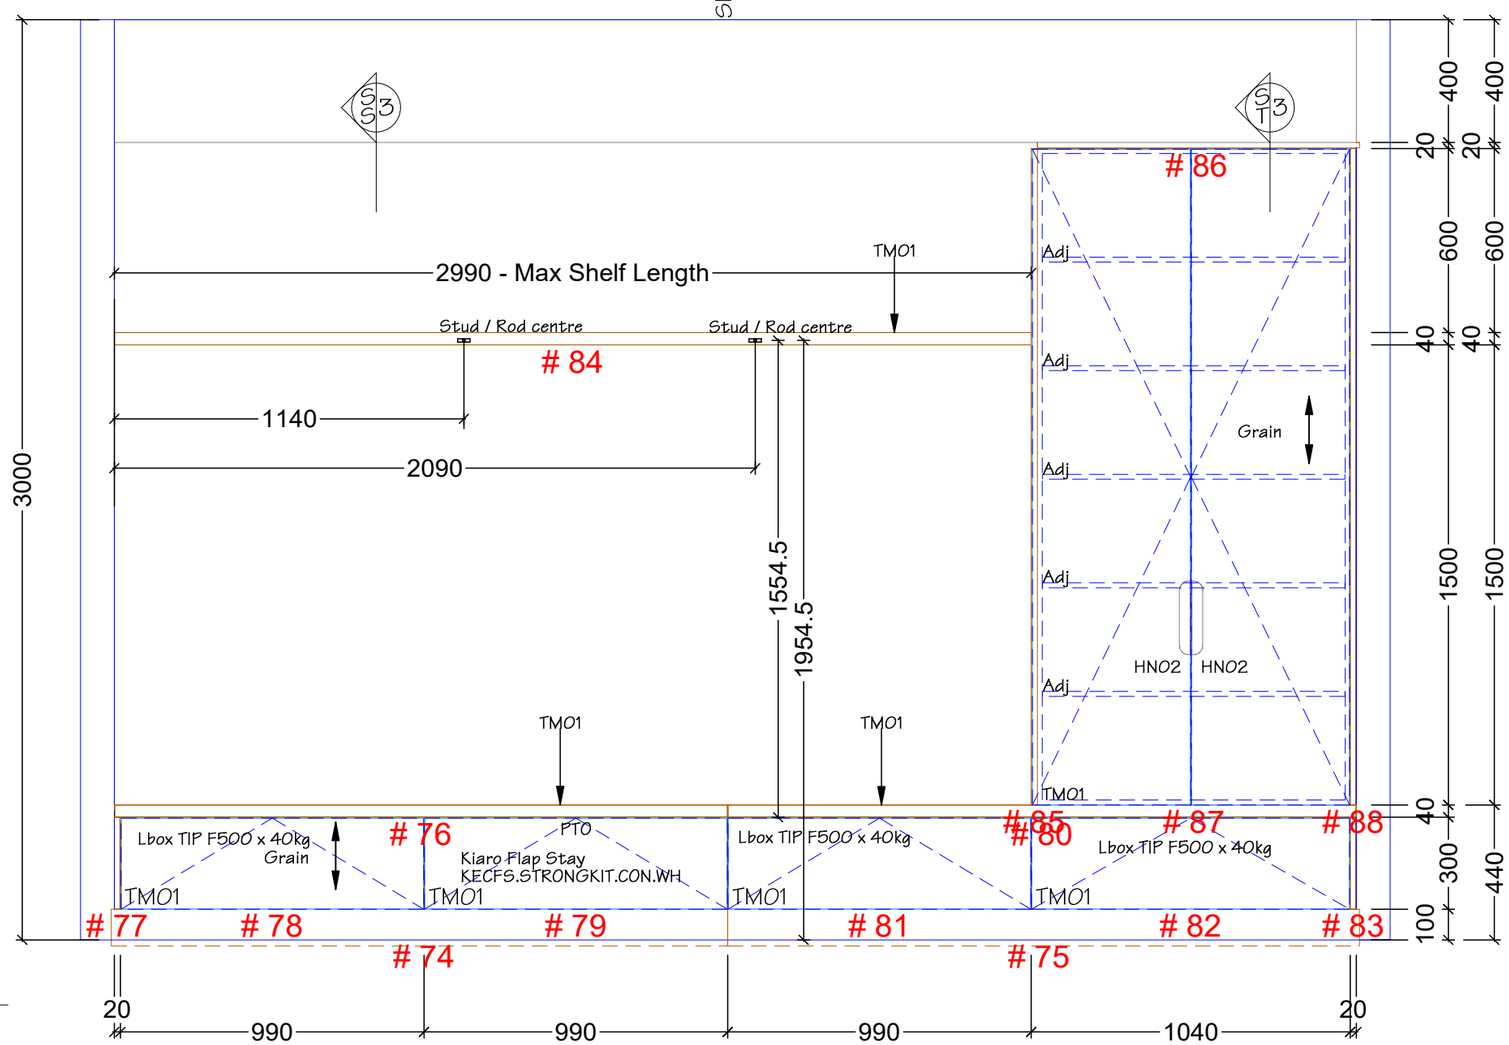

2 Elevation - Family
3 Scale: 1:20

Approved CN Drawings Supersede All Other Drawings and Specs

CODE	DESCRIPTION
HNO1	32mm Touch Handles Circ Semi Circle Pull 'Dull Brushed Nickel CIRC32.DBR'
HNO2	192mm Touch Handles OVA Semi Oval Pull Handle 'Dull Brushed Nickel, OVA192.DBR'
HNO3	40mm Touch Handles Veda Knob 'Brushed Nickel V35.40.BRN'
PTO1	18mm 2Pac Dulux White Beach Quarter Satin - Sussex Profile
PTO3	18mm 2Pac to match Polytec Topiary
STO1	20mm Caesarstone '5031 Statuario Maximus'
TMO1	18mm George Fethers Veneer w/ 2Pac ' Blok, LOB 67.03'

Name: A and D Building

Address:
9 Moorehouse St
Camberwell

Sheet # 18 of 22

Date: 21/10/26

Drawn By: AF

JOB STANDARD MATERIALS

UNLESS STATED OTHERWISE
INTERNAL CARCASSES TO BE:
* 16mm White - 1mm
ALL ADJ SHELF HOLES 5X 5MM HOLES 32MM SPACINGS
ALL DRAWERS TO BE *Blum Legrabox Drawer
ALL HINGES TO BE 110* BLUM SOFTCLOSE

CN FITOUTS PTY LTD
CUSTOM MADE JOINERY

P 03 9761 6994
E info@cnfitouts.com.au
www.cnfitouts.com.au

6 Stephenson rd.
Bayswater North 3153